

Register výkresov a otvorených bodov

VÝKRESOVÁ SADA · REGISTER VYDANIA

Táto sada zachováva hotový pôdorys C/B/B a oddeľuje presnú modelovú geometriu od konštrukcii, ktoré treba nanovo navrhnuť. Požadovaná realizačná úplnosť zatiaľ nie je dosiahnutá.

Líst	Obsah
D1.1.002-C-RE	Existujúci pôdorys · stopy rezov
D1.1.PO-01	Južná (uličná) fasáda
D1.1.PO-02	Východná fasáda
D1.1.PO-03	Záhradná (severná) fasáda
D1.1.PO-04	Západný štít garáže
D1.1.PO-05	Západná stena krídla
D1.1.PO-06	Štít krídla · portál krytej terasy
D1.1.PO-07	Krytá terasa · zasklená stena
D1.1.PO-08	Lodžia · zadná stena garáže
D1.1.RE-01	A-A · Pozdĺžny rez krídlom
D1.1.RE-02	B-B · Pričný rez katedrálovým stropom
D1.1.RE-03	C-C · Pričný rez hlavným traktom
D1.1.ZA-01	Základy · nosné línie a ťažké priečky
D1.1.ZA-02	Monolitické založenie · rozmery a väzby
D1.1.ZA-03	Základy · priestorový pohľad na pásy a rebrá
D1.1.ST-01	Pôdorys strechy
C.SI-01	Situácia osadenia · ulica
C.SI-02	Situácia osadenia · záhrada
C.UP-01	Kontrola územného plánu
D1.1.OT-01	Výpis okien a vonkajších dverí
D1.1.OT-02	Výpis vnútorných dverí
D1.1.SK-01	Skladby konštrukcií · register
D1.1.DT-01	Akustické steny H200 / SA30
D1.1.TZ-01	Podlahové vykurovanie a rozsah povaly

R01 · Nový nosný systém

Výpočet aktuálneho C/B/B, zafarženie a reakcie, základy, doska, preklady, vence, oceľové rámy, krov a všetky spoje. Staré D1/D2 sú podľa stavebníka iba archiv.

R02 · Monolit a založenie

Podľa stavebníka je doska vylíata aj s lodžiou a krytou terasou. Horný pás zadany 350 × 600 mm. Zamerať skutočný rozsah, výšky, hrúbku a výstuž; uzavrieť podopretie a nové rebrá.

R03 · Nová podlaha s rozvodmi

Rozvody vody a odpadu nad nosnou doskou; žiadne dodatočné vrty do dosky. Určiť horné líce dosky, kompletnú skladbu, priemery, spády, križovania a vývod cez obvod.

R04 · Drevený strop a skladovacia povala

Povala iba na odkladanie, mimo obývačky. Drevené stropy bez betónovej dosky/nadbetónávky. Určiť skladovacie a bodové zafarženia, prierezy a spoje; krov s falcovaným plechom bez presahov.

R05 · Spoločná nula a vstup

R0 = 184,200 m pri ulici. Podlahu navrhne projekt podľa nivelácie hotového pásu a terénu; aspoň jeden vstupný stupeň. Návrh podesty pri D2 na SI-01. Potvrdiť Bpv a bod XY.

R06 · Sokel, ETICS, otvory

Nové detaily hydroizolácie a sokla, založenia ETICS, parapetov, prahov, nadpraží a napojenia tesniacich vrstiev. Výpis otvorov nie je výrobný rozmer rámu.

R07 · Akustické priečky

Vlastná hmotnosť AK-01/02/03 a jej prenos do základov, stabilita plášťov, kotvy a obvodové spoje. SA30 zafaržuje dosku aj ako nenosná priečka. Strecha a strop potrebujú samostatné nosné riešenie.

R08 · Dymovody a odvodnenie

Systémový návrh a odstupy dymovodu obývačky; kotoľňa B končí v modeli rezervou pod stropom, vonkajšia trasa nie je určená. Návrh žľabov, zvodov a dažďovej kanalizácie.

R09 · Dodávateľský výpis otvorov

Profily, zasklenie, bezpečnostné/tepelné/akustické vlastnosti, montážne škáry, kovanie a prahy. Trojuholníkový svetlík doplnený O11 bez prečíslovania O1-O10/D1-D16.

PODMIENKA VYDANIA: uzavreté R01-R09 + koordinácia všetkých profesií + kontrola všetkých listov.

KONTROLA TLAČE 100 % - 1 000 mm ≈ 20 mm na papieri

1 : 50 - vypnúť „prispôbiť strane“

NOVOSTAVBA RD BŘEZÍ U MIKULOVA

PARCELA 6012/26 · HLAVNÝ NÁVRH C / B / B

Register výkresov a otvorených bodov

R0 = 184,200 m · M0 = PODLAHA MODELU · ΔFFL = M0 – R0 ZATIAĽ NEURČENÉ

Požiadavka stavebníka 14.09.2026: nový projekt od začiatku; pôvodná statika orientačná. Pôdorys a hlavný návrh C/B/B bez zmeny.

STAV


NEVYDANÉ NA REALIZÁCIU

Chýbajúci návrh sa nesmie nahradiť mierkou výkresu.

VYPRACOVAL: digitálne dvojča · bez autorizačnej pečiatky

DÁTUM 2026-09-14 FORMÁT A1 841 × 594 mm MIERKA register

ZDROJ 6c4bce82841b · úplné odtlačky v model-snapshot.json

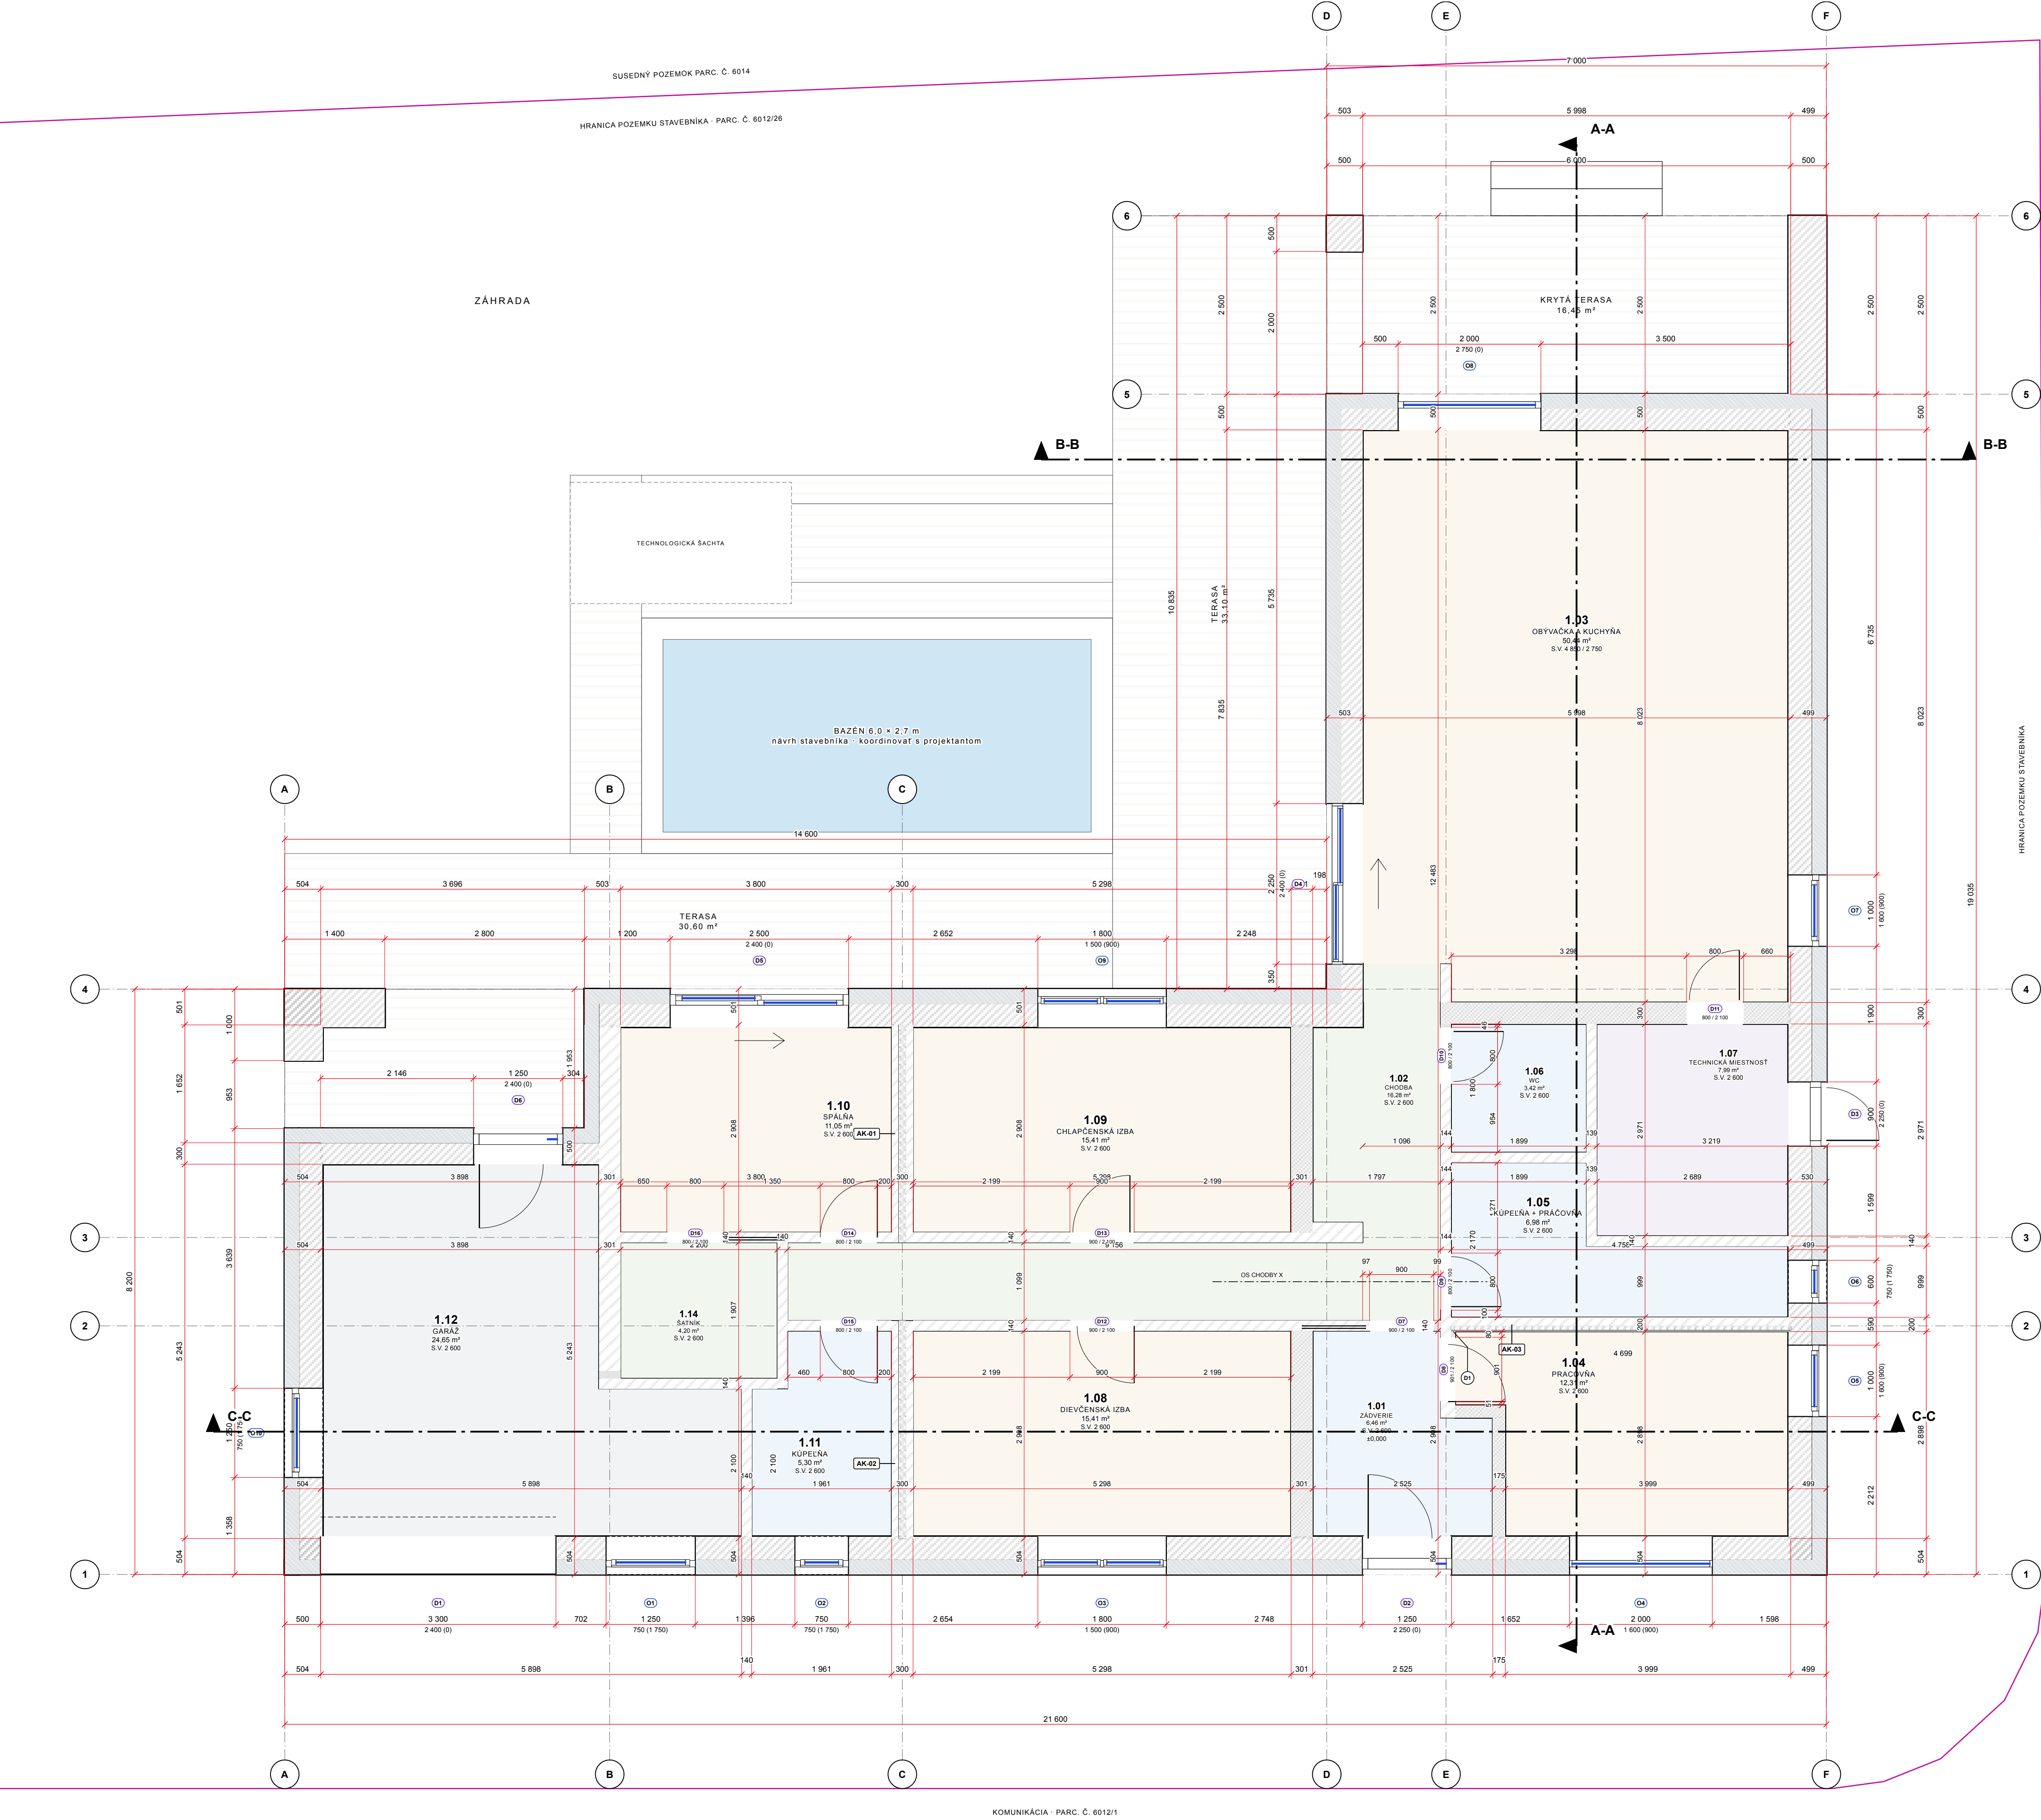

LEGENDA

KÓTY A OSI

Radý pri fasáde: 1. otvor – šírka nad čiarou, výška (parapet) pod čiarou - 2. líce priľahlých stien - 3. celkový rozmer

Refazce cez miestnosti: svetlé šírky a hrúbky stien za sebou - červené čísla pri stenách = svetlé rozmery miestnosti

Poloha dverí: odstupy stavebného otvoru od stien miestnosti, do ktorej sa krídlo otvára

Modulové osi: písmená A–F po šírke (→), čísla 1–6 po hĺbke (↑); C–D / 1–2 = pole medzi osami – jednoznačná poloha aj v čiernobielej tlači

Kóty v mm podľa 3D modelu, spravidla bez omietok a obkladov: AK-03 / H200: 200 mm vrátane 2 × 15 mm

PŮVODNÉ ±0,000 TOHTO LISTU = M0 PODLAHY; R0 ULICE = 184,200 m; ROZDIEL ΔFFL ZATIAŤ NEURČENÝ.

DOPLNENÉ STOPY A-A, B-B, C-C - geometria a kódy bez zmeny - nové konštrukcie NEVYDANÉ NA REALIZÁCIU

MIESTNOSTI

1.03 - číselo - účel - plocha čistej podlahy - S.V. = svetlá výška

Obytné miestnosti

Hygienické zázemie

Komunikácie a šatník

Technická miestnosť

Garáž

drevená terasa 1.13 (80,15 m²) - bazén a šachta = návrh stavebníka, nie je súčasťou D1

POZNÁMKY

Výkres je exportom aktívneho 3D modelu variantu C (revízia C-2026-09-07) v konvenciách D1.1.002. Obvodová stena 500 mm, líce podtlah v modeli 499-504 mm od vonkajšieho líca. Nejde o geometrické zameranie; statiku, TZB, komín a podlažné riešenie potvrdí projektant.

LEGENDA MIESTNOSTÍ 1. NP

OZN.	ÚČEL MIESTNOSTI	PLOCHA m²	S.V. mm	PODLAHA	STENY	STROP	OSI
1.01	ZÁDVERIE	6.46	2 600	KERAMICKÁ DLAŽBA	VÁPENOCEM. OMÍETKA	SDK PODHEAD	D-E / 1-2
1.02	CHODBA	16.28	2 600	VINYL	VÁPENOCEM. OMÍETKA	SDK PODHEAD	C-D / 3-4
1.03	OBYVACIA A KUCHYŇA	50.44	4 850 / 2 750	VINYL	VÁPENOCEM. OMÍETKA	SDK PODHEAD - ŠIKMÝ	E-F / 4-5
1.04	PRACOVŇA	12.31	2 600	VINYL	VÁPENOCEM. OMÍETKA	SDK PODHEAD	E-F / 1-2
1.05	KUPEĽNA + PRACOVŇA	6.98	2 600	KERAMICKÁ DLAŽBA	KER. OBKLAD v. 2 100	SDK PODHEAD - VĽHKÉ PR.	E-F / 3
1.06	WC	3.42	2 600	KERAMICKÁ DLAŽBA	KER. OBKLAD v. 2 100	SDK PODHEAD - VĽHKÉ PR.	E-F / 3-4
1.07	TECHNICKÁ MIESTNOSŤ	7.99	2 600	EPOXIDOVÁ STIERKA	KER. OBKLAD v. 2 100	SDK PODHEAD - VĽHKÉ PR.	E-F / 3-4
1.08	DIEVČENSKÁ IZBA	15.41	2 600	VINYL	VÁPENOCEM. OMÍETKA	SDK PODHEAD	C-D / 1-2
1.09	CHLAPEČSKÁ IZBA	15.41	2 600	VINYL	VÁPENOCEM. OMÍETKA	SDK PODHEAD	C-D / 3-4
1.10	SPÁLŇA	11.05	2 600	VINYL	VÁPENOCEM. OMÍETKA	SDK PODHEAD	B-C / 3-4
1.11	KUPEĽNA	5.30	2 600	KERAMICKÁ DLAŽBA	KER. OBKLAD v. 2 100	SDK PODHEAD - VĽHKÉ PR.	B-C / 1-2
1.12	GARAŽ	24.65	2 600	EPOXIDOVÁ STIERKA	VÁPENOCEM. OMÍETKA	SDK PODHEAD	A-B / 1-2
1.14	ŠATNÍK	4.20	2 600	VINYL	VÁPENOCEM. OMÍETKA	SDK PODHEAD	B-C / 2
1.13	TERASA (3 ČASTI)	80.15	—	DREVENÁ TERASOVÁ PODLAHA	—	—	A-D / 4-6
2.	ČISTÁ PODLAHA 13 MIESTNOSTÍ	179.87	—	—	—	—	—

LEGENDA MATERIÁLOV

SO30, SO50 - Nosné obvodové múrivo z keramických tvaroviek hr. 300 mm, na systémovú murovaciu maltu; obvodová stena celkom 500 mm. Murované piliere a voľné úseky stien na terasách a v lodži (SO50) sú plné múrivo hr. 500 mm bez zateplenia

T120 - Kontaktný zatepľovací systém (ETICS) z minerálnej vlny hr. 200 mm na vonkajšom líci obvodového múriva, s tenkovrstvovou omietkou

SN30, SN20 - Nosné vnútorné múrivo z keramických tvaroviek hr. 300 / 200 mm, na systémovú murovaciu maltu

SP30, SP20, SP14 - Nenosné priečkové múrivo z keramických tvaroviek hr. 300 / 200 / 140 mm, na systémovú murovaciu maltu (vrátane puzdra posuvných dverí)

SP10, SP6 - Sadrokartónové systémové priečky a predsteny hr. 100 / 60 mm, napr. Rigips W112, s výplňou z minerálnej vlny

SA30 - AK-01 spáľňa / chlapčenská izba; AK-02 kúpeľňa / dievčenská izba. LeierPLAN 10 P10 100 + minerálna vata 100 + LeierPLAN 10 P10 100 mm. Celkom 300 mm bez omietok a obkladov. Statika a akustické napojenia na posúdenie; Rw zostavý nedoložené.

H200 - AK-03 pracovňa / sprcha. Od sprchy: VC omietka 15 + LeierPLAN 10 100 + omietka 15 + dutina W623 45 (pružné závesy, vata 40) + 2 × 12.5 Silentboard = 200 mm; finálne povrchy navyše. Požiadavka Rw ≥ 51 dB; predbežný výpočet = 58 dB, presnú zostavu a napojenia potvrdí.

ZÁKLADNÉ ÚDAJE

ÚDAJ	HODNOTA
Pódorys	L - hlavné krídlo ulica-záhrada + krídlo s krytou terasou
Vonkajšie rozmery	21 600 × 19 035 mm - hlavné krídlo hĺbka 8 200 - krídlo šírka 7 000
Zastavaná plocha	262,97 m² po vonkajšie líce stien
Otvory v obvodě	10 okien a presklení - 6 dverí, brán a posuvných stien - 10 vnútorných dverí
Výšky	±0,000 = čistá podlaha 1. NP - S.V. 2 600 pod SDK podtlahom - obyvatka 2 750 pri stene, 4 850 pod hrebeňom

TABUĽKA OTVOROV

KÓD	OTVOR	TYP	MIEST.	ŠÍRKA	VÝŠKA	PARAPET	NADPR. / FASÁDA - OSI
D1	Sekčná garážová brána	sekčná brána	1.12	3 300	2 400	0	2 400 S - A-B
O1	Okno FRONT-02	okno	1.12	1 250	750	1 750	2 500 S - A-B
O2	Okno FRONT-03	okno	1.11	750	750	1 750	2 500 S - B-C
O3	Dvojkrižové okno oproti dverám	okno	1.08	1 800	1 500	900	2 400 S - C-D
O2	Hlavné vstupné dvere	dvere	1.01	1 250	2 250	0	2 250 S - D-E
O4	Okno FRONT-07	okno	1.04	2 000	1 600	900	2 500 S - E-F
O5	Bočné okno EAST-01	okno	1.04	1 000	1 600	900	2 500 E - E-F
O6	Bočné okno EAST-02	okno	1.05	600	750	1 750	2 500 E - E-F
O3	Dvere technickej miestnosti	dvere	1.07	900	2 250	0	2 250 E - E-F
O7	Bočné okno EAST-04	okno	1.03	1 000	1 600	900	2 500 E - E-F
O8	Pevné presklenie terasy	pevné presklenie	1.03	2 000	2 750	0	2 750 NN2 - E-F
D4	Terasové posuvné presklenie 2 250	posuvné presklenie	1.03	2 250	2 400	0	2 400 WW - E-F
O9	Dvojkrižové okno oproti dverám	okno	1.09	1 800	1 500	900	2 400 N - C-D
D5	Terasové presklenie 2500	posuvné presklenie	1.10	2 500	2 400	0	2 400 N - B-C
O10	Bočné garážové okno WEST-GARAGE-01	okno	1.12	1 250	750	1 750	2 500 W - A-B
D6	Garáž → krytý zárez	dvere	1.12	1 250	2 400	0	2 400 L - A-B
D7	Zádverie → centrálna chodba	posuvné dvere do puzdra	1.02	900	2 100	0	2 100 int. - C-D
D8	Zádverie → pracovňa	vnútorné dvere	1.04	901	2 100	0	2 100 int. - E-F
D9	Dvere chodba → kúpeľňa 1.05	vnútorné dvere	1.05	800	2 100	0	2 100 int. - E-F
D10	Dvere chodba → WC	vnútorné dvere	1.06	800	2 100	0	2 100 int. - E-F
D11	Dvere obytný priestor → technická miestnosť	vnútorné dvere	1.07	800	2 100	0	2 100 int. - E-F
D12	Chodba → detská izba do ulice	vnútorné dvere	1.08	900	2 100	0	2 100 int. - C-D
D13	Dvere chodba → izba 1.09	vnútorné dvere	1.09	900	2 100	0	2 100 int. - C-D
D14	Spáľňa za novou priečkou	vnútorné dvere	1.10	800	2 100	0	2 100 int. - B-C
D15	Otvorený vstup z chodby → kúpeľňa	vnútorné dvere	1.11	800	2 100	0	2 100 int. - B-C
D16	Spáľňa → šatník	posuvné dvere do puzdra	1.14	800	2 100	0	2 100 int. - B-C

SVETLÉ ROZMERY MIESTNOSTÍ (mm)

OZN.	OBDELNÍKY ČISTEJ PODLAHY - ŠÍRKA × HĽBKA
1.01	1 797 × 2 008 + 728 × 1 691
1.02	6 300 × 1 099 + 1 096 × 4 998 + 701 × 2 768 + 1 460 × 1 099 + ...
1.03	5 998 × 7 485 + 4 758 × 538
1.04	3 999 × 1 866 + 4 699 × 1 032
1.05	1 899 × 2 170 + 2 859 × 999
1.06	1 899 × 1 800
1.07	2 689 × 2 971
1.08	5 298 × 2 008
1.09	5 298 × 2 008
1.10	3 800 × 2 008
1.11	1 961 × 2 100 + 1 460 × 808
1.12	3 898 × 5 245 + 2 000 × 2 100
1.14	2 200 × 1 907

0 1 2 3 4 5 m

1: 50 (A1) 1: 100 (A3)

30,000 = ČISTÁ PODLAHA 1. NP

STAVEBNÍK David Zita, Hana Ivčizová - Dmholtec

PODKLAD D1.1.002 Pódorys 1. NP - DPSZ 04/2026 - Ing. arch. Jiří Bradáč, Ing. arch. Vladimír Muzkař

VYPRACOVANÉ Digitálne dvojča - export z aktívneho 3D modelu variantu C - revízia C-2026-09-07

PODKLAD PRE REALIZÁCIU - EXPORT Z DIGITÁLNEHO DVOJČATA

NÁZOV A Miesto stavby

NOVOSTAVBA RD BŘEZÍ U MIKULOVA

PARC. Č. 6012/26, K.Ú. BŘEZÍ U MIKULOVA, 691 81 BŘEZÍ U MIKULOVA


OBJEKT	FORMÁT	A1 - 841 × 594 mm
RD BŘEZÍ U MIKULOVA - VARIANT C	DATUM	14. 08. 2026
CASŤ	STUPEŇ	DT - L3
D1.1 ARCHITEKTONICKO-STAVEBNÉ RIEŠENIE	REVÍZIA	C-2026-09-07
VÝKRES	MIERKA	1: 50
	VERZIA	F - TB - 15 kW + 800 l
	ČÍSLO PRÍLOHY	

PŮDORYS 1. NP

-C-L3

Južná (uličná) fasáda

ROVINA Y = 3 000 mm · čítanie rastúcich súradníc X

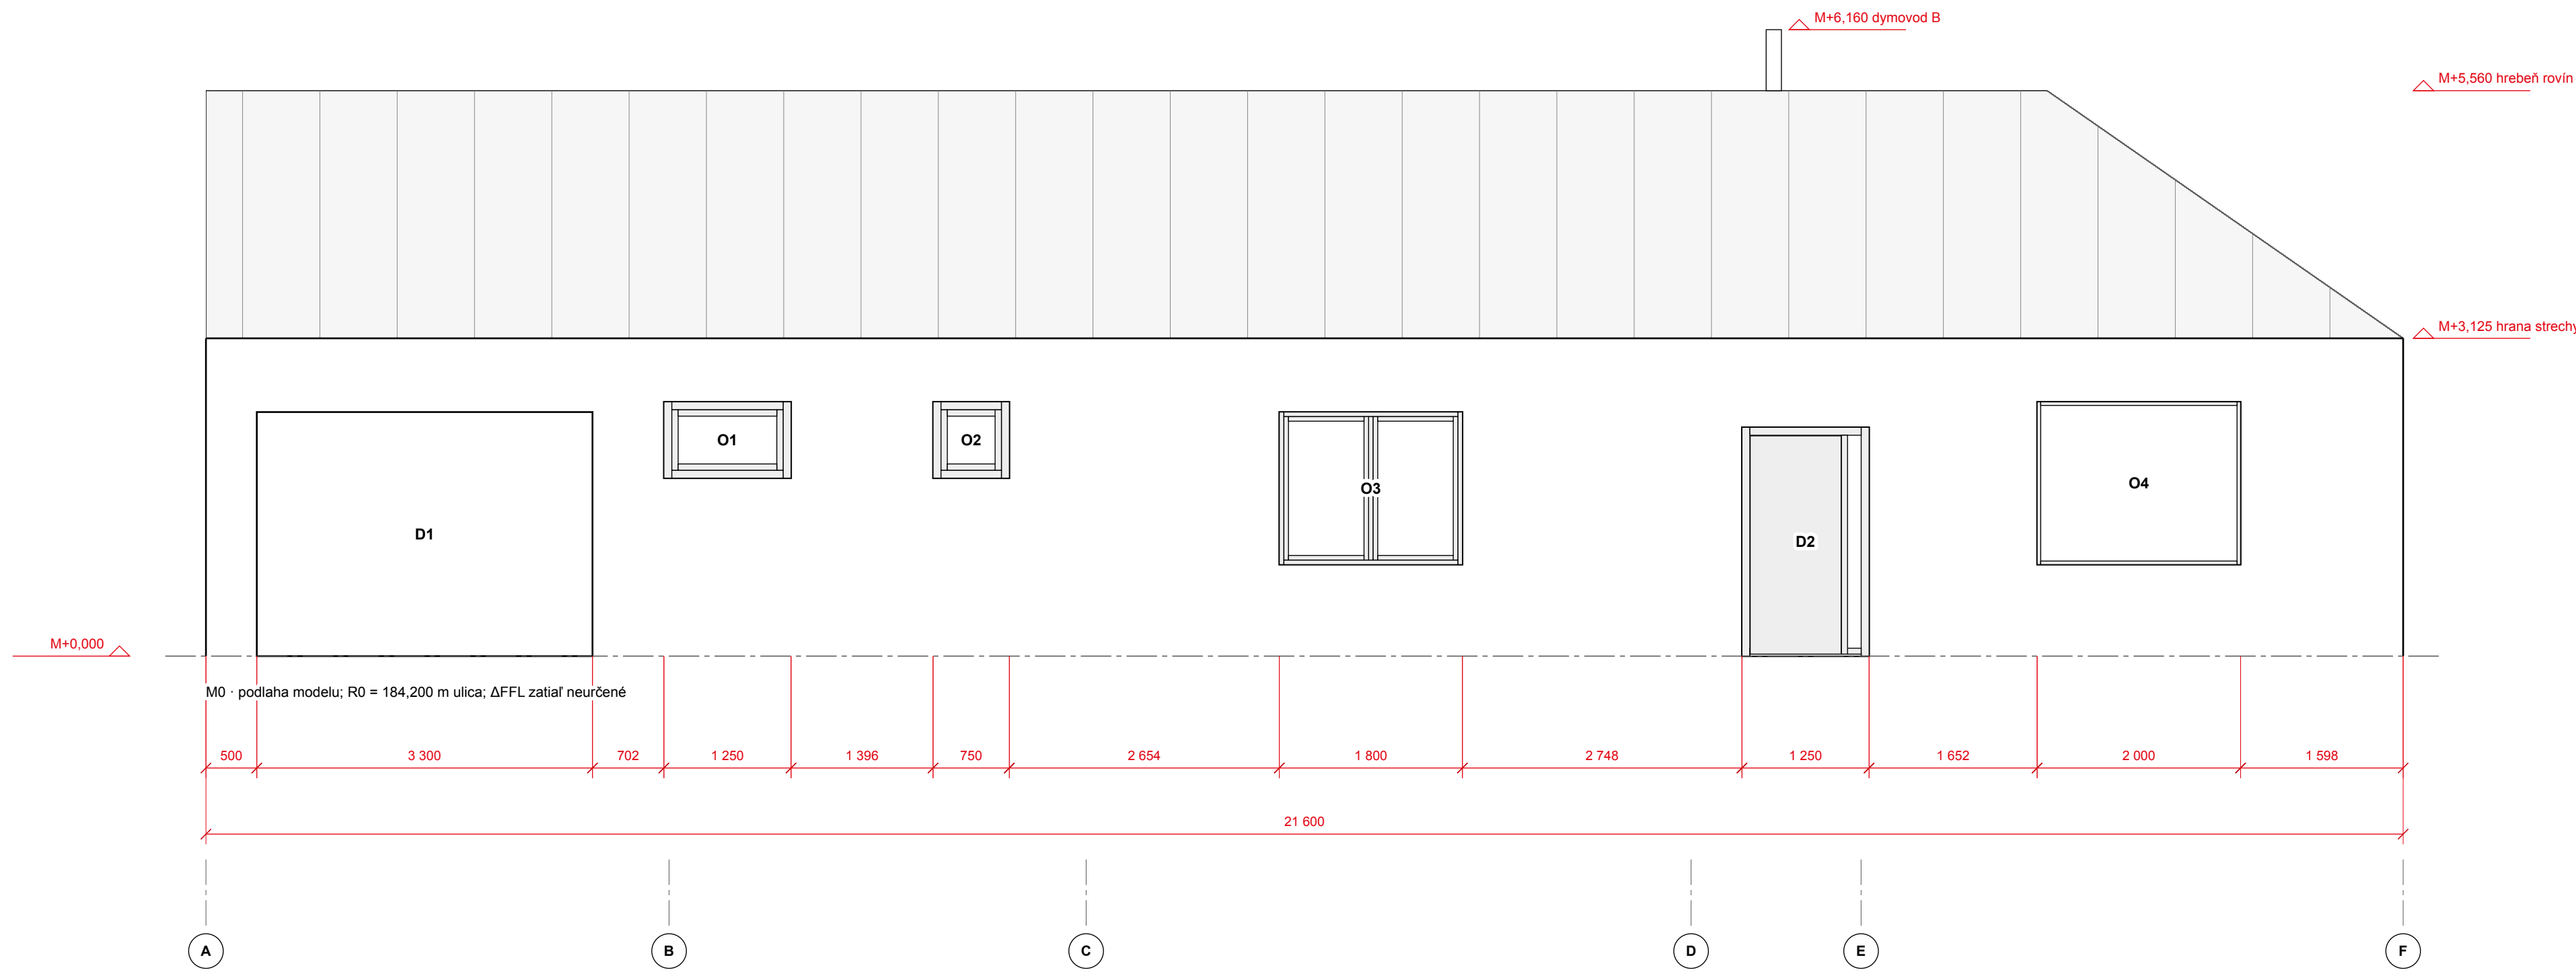

VYTYČOVACIE ÚDAJE OTVOROV TEJTO ROVINY

Kód / identifikátor	Od / do [mm]	Š × V [mm]	Parapet / nadpražie
D1 / GARAGE-DOOR	X 6 940 / 10 240	3 300 × 2 400	0 / 2 400
O1 / Výplň otvoru FRONT-02	X 10 942 / 12 192	1 250 × 750	1 750 / 2 500
O2 / Výplň otvoru FRONT-03	X 13 588 / 14 338	750 × 750	1 750 / 2 500
O3 / Výplň otvoru FRONT-05	X 16 992 / 18 792	1 800 × 1 500	900 / 2 400
D2 / Výplň otvoru FRONT-ENTRY	X 21 540 / 22 790	1 250 × 2 250	0 / 2 250
O4 / Výplň otvoru FRONT-07	X 24 442 / 26 442	2 000 × 1 600	900 / 2 500

ZNAČKY A MATERIÁLY

- Murivo / keramické prvky
ETICS / minerálna vlna
Betón – len ak je určený návrhom
Drevený obklad

Čiarkovane: prerušené / neurčené konštrukcie.

M = výška k podlahe modelu. Dĺžky v mm.

K ulici RO: z = M + ΔFFL. ΔFFL neurčené.

Obvodový plášť SO30 + TI20: nosné murivo 300 mm a ETICS 200 mm. Voľné piliere SO50: 500 mm plné murivo. Skladby a detaily DT/SK.

KONTROLA TLAČE 100 % - 1 000 mm ≈ 20 mm na papieri

1 : 50 - vypnúť „prispôbiť strane“

NOVOSTAVBA RD BŘEZÍ U MIKULOVA

PARCELA 6012/26 · HLAVNÝ NÁVRH C / B / B

Južná (uličná) fasáda

RO = 184,200 m · MO = PODLAHA MODELU · ΔFFL = MO – RO ZATIAĽ NEURČENÉ

Presná modelová projekcia. R05/R06: chýba skutočný terén, sokel, finálne povrchy a realizačné detaily. Rozmery otvorov sú modelové stavebné otvory; výrobný rozmer určí dodávateľ.

STAV

NEVYDANÉ NA REALIZÁCIU

Chýbajúci návrh sa nesmie nahradiť mierkou výkresu.


VYPRACOVAL: digitálne dvojča · bez autorizačnej pečiatky

DÁTUM 2026-09-14 FORMÁT A1 841 × 594 mm MIERKA 1 : 50

ZDROJ 6cd4bc82841b · úplné odtlačky v model-snapshot.json

Východná fasáda

ROVINA X = 28 040 mm · čítanie rastúcich súradníc Y

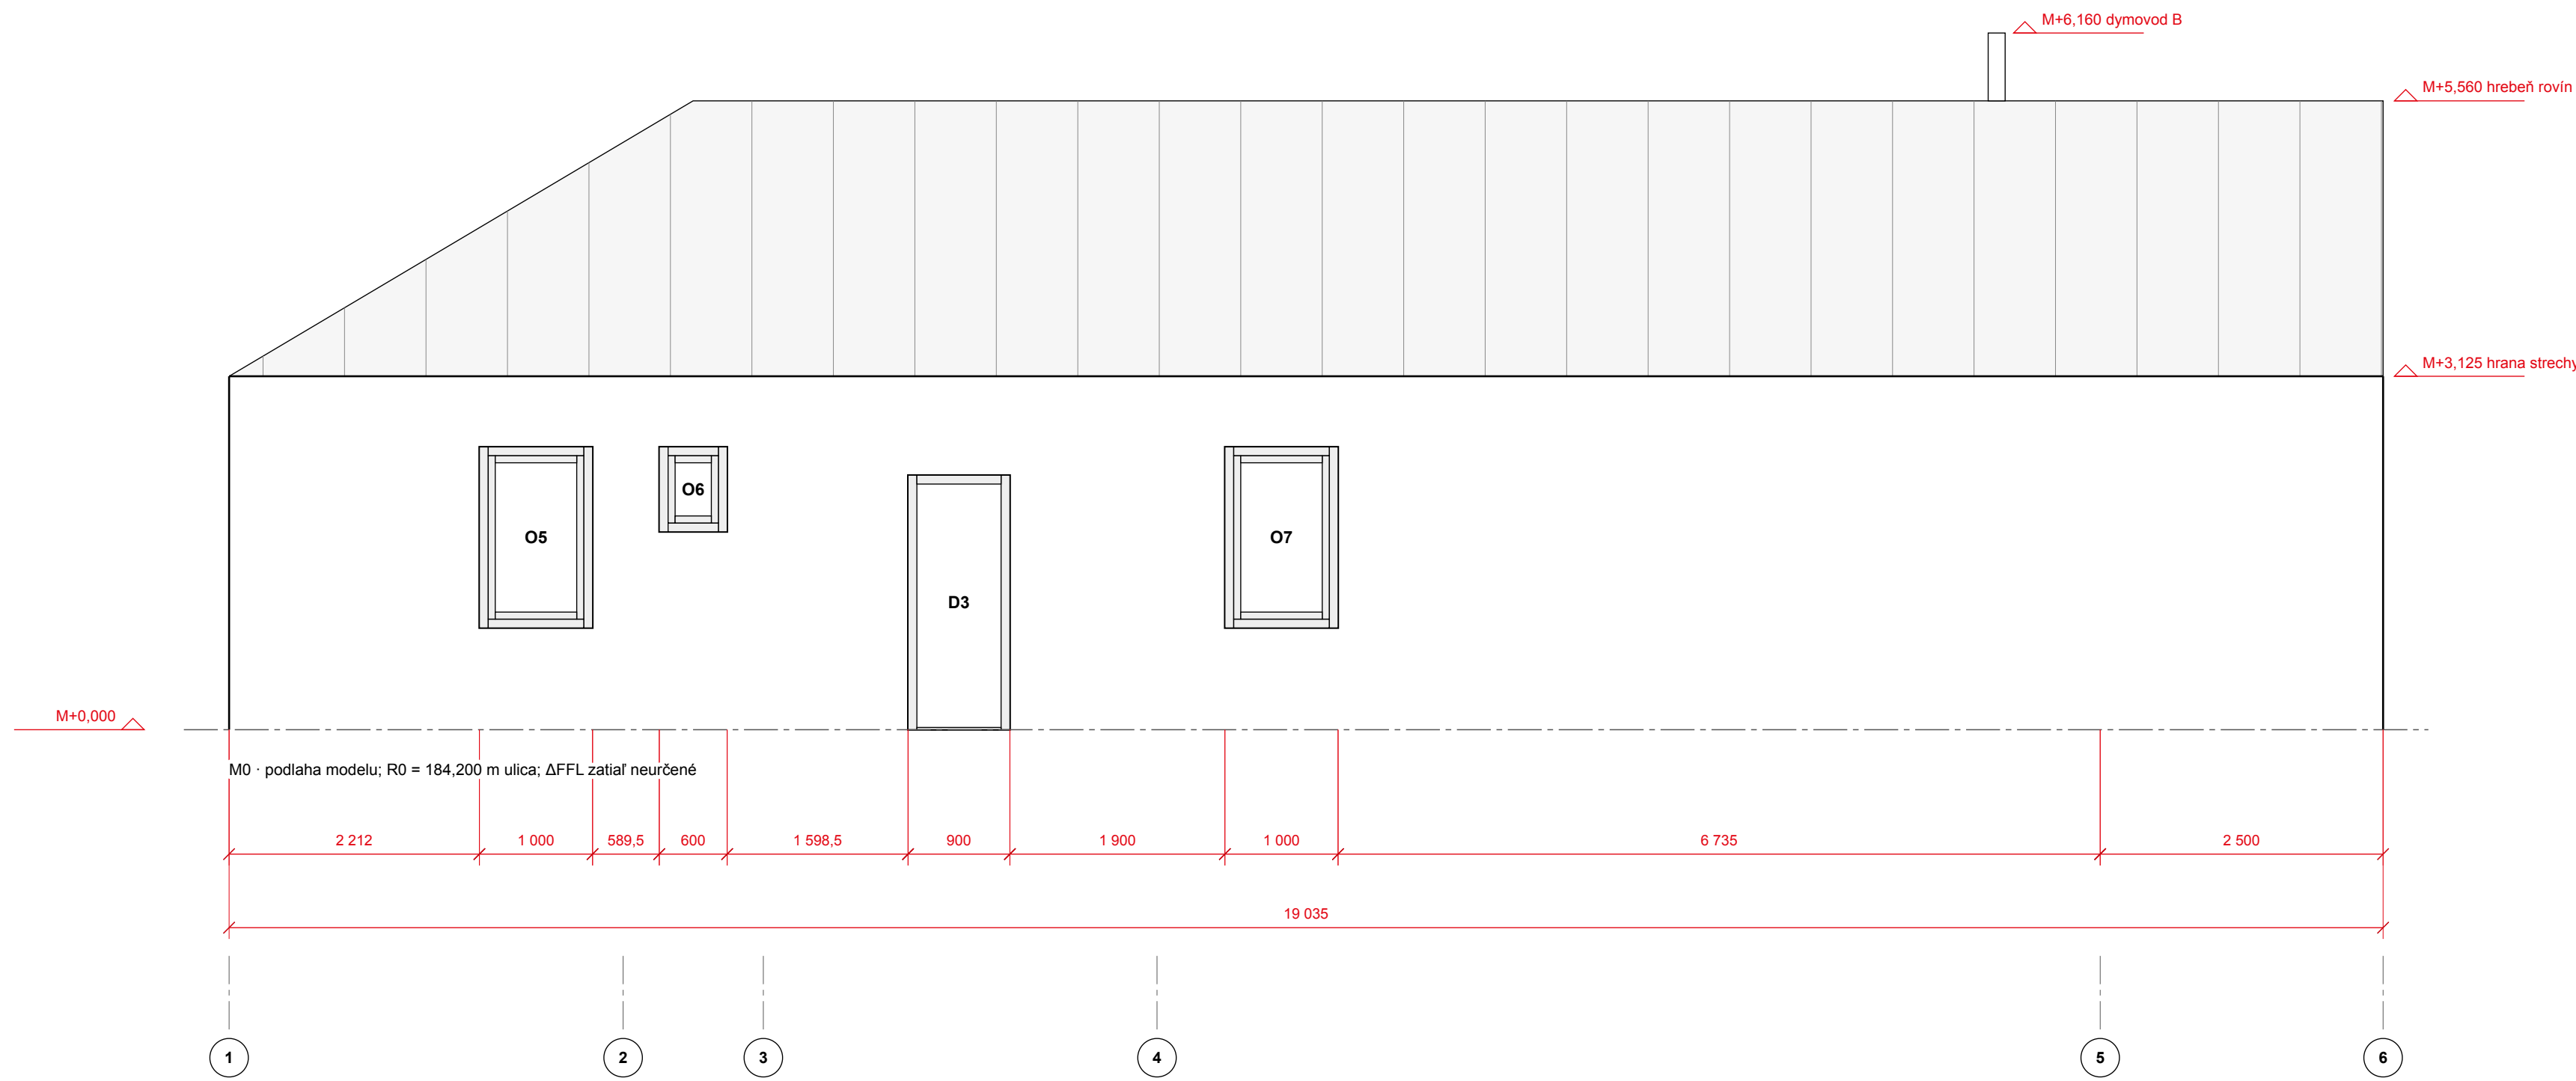

VYTYČOVACIE ÚDAJE OTVOROV TEJTO ROVINY

Kód / identifikátor	Od / do [mm]	Š × V [mm]	Parapet / nadpražie
O5 / Bočná výplň otvoru EAST-01	Y 5 212 / 6 212	1 000 × 1 600	900 / 2 500
O6 / Bočná výplň otvoru EAST-02	Y 6 801,5 / 7 401,5	600 × 750	1 750 / 2 500
D3 / Bočná výplň otvoru EAST-03	Y 9 000 / 9 900	900 × 2 250	0 / 2 250
O7 / Bočná výplň otvoru EAST-04	Y 11 800 / 12 800	1 000 × 1 600	900 / 2 500

ZNAČKY A MATERIÁLY

- Murivo / keramické prvky
- ETICS / minerálna vlna
- Betón – len ak je určený návrhom
- Drevený obklad

Čiarkovane: prerušené / neurčené konštrukcie.

M = výška k podlahe modelu. Dĺžky v mm.

K ulici R0: z = M + ΔFFL. ΔFFL neurčené.

Obvodový plášť SO30 + TI20: nosné murivo 300 mm a ETICS 200 mm. Voľné piliere SO50: 500 mm plné murivo. Skladby a detaily DT/SK.

KONTROLA TLAČE 100 % - 1 000 mm ≈ 20 mm na papieri

1 : 50 - vypnúť „prispôbiť strane“

NOVOSTAVBA RD BŘEZÍ U MIKULOVA

PARCELA 6012/26 · HLAVNÝ NÁVRH C / B / B

Východná fasáda

R0 = 184,200 m · M0 = PODLAHA MODELU · ΔFFL = M0 – R0 ZATIAĽ NEURČENÉ

Presná modelová projekcia. R05/R06: chýba skutočný terén, sokel, finálne povrchy a realizačné detaily. Rozmery otvorov sú modelové stavebné otvory; výrobný rozmer určí dodávateľ.

STAV

NEVYDANÉ NA REALIZÁCIU

Chýbajúci návrh sa nesmie nahradiť mierkou výkresu.


VYPRACOVAL: digitálne dvojča · bez autorizačnej pečiatky

DÁTUM 2026-09-14 FORMÁT A1 841 × 594 mm MIERKA 1 : 50

ZDROJ 6cd4bc82841b · úplné odtlačky v model-snapshot.json

Záhradná (severná) fasáda

ROVINA Y = 11 200 mm - čítanie klesajúcich súradníc X

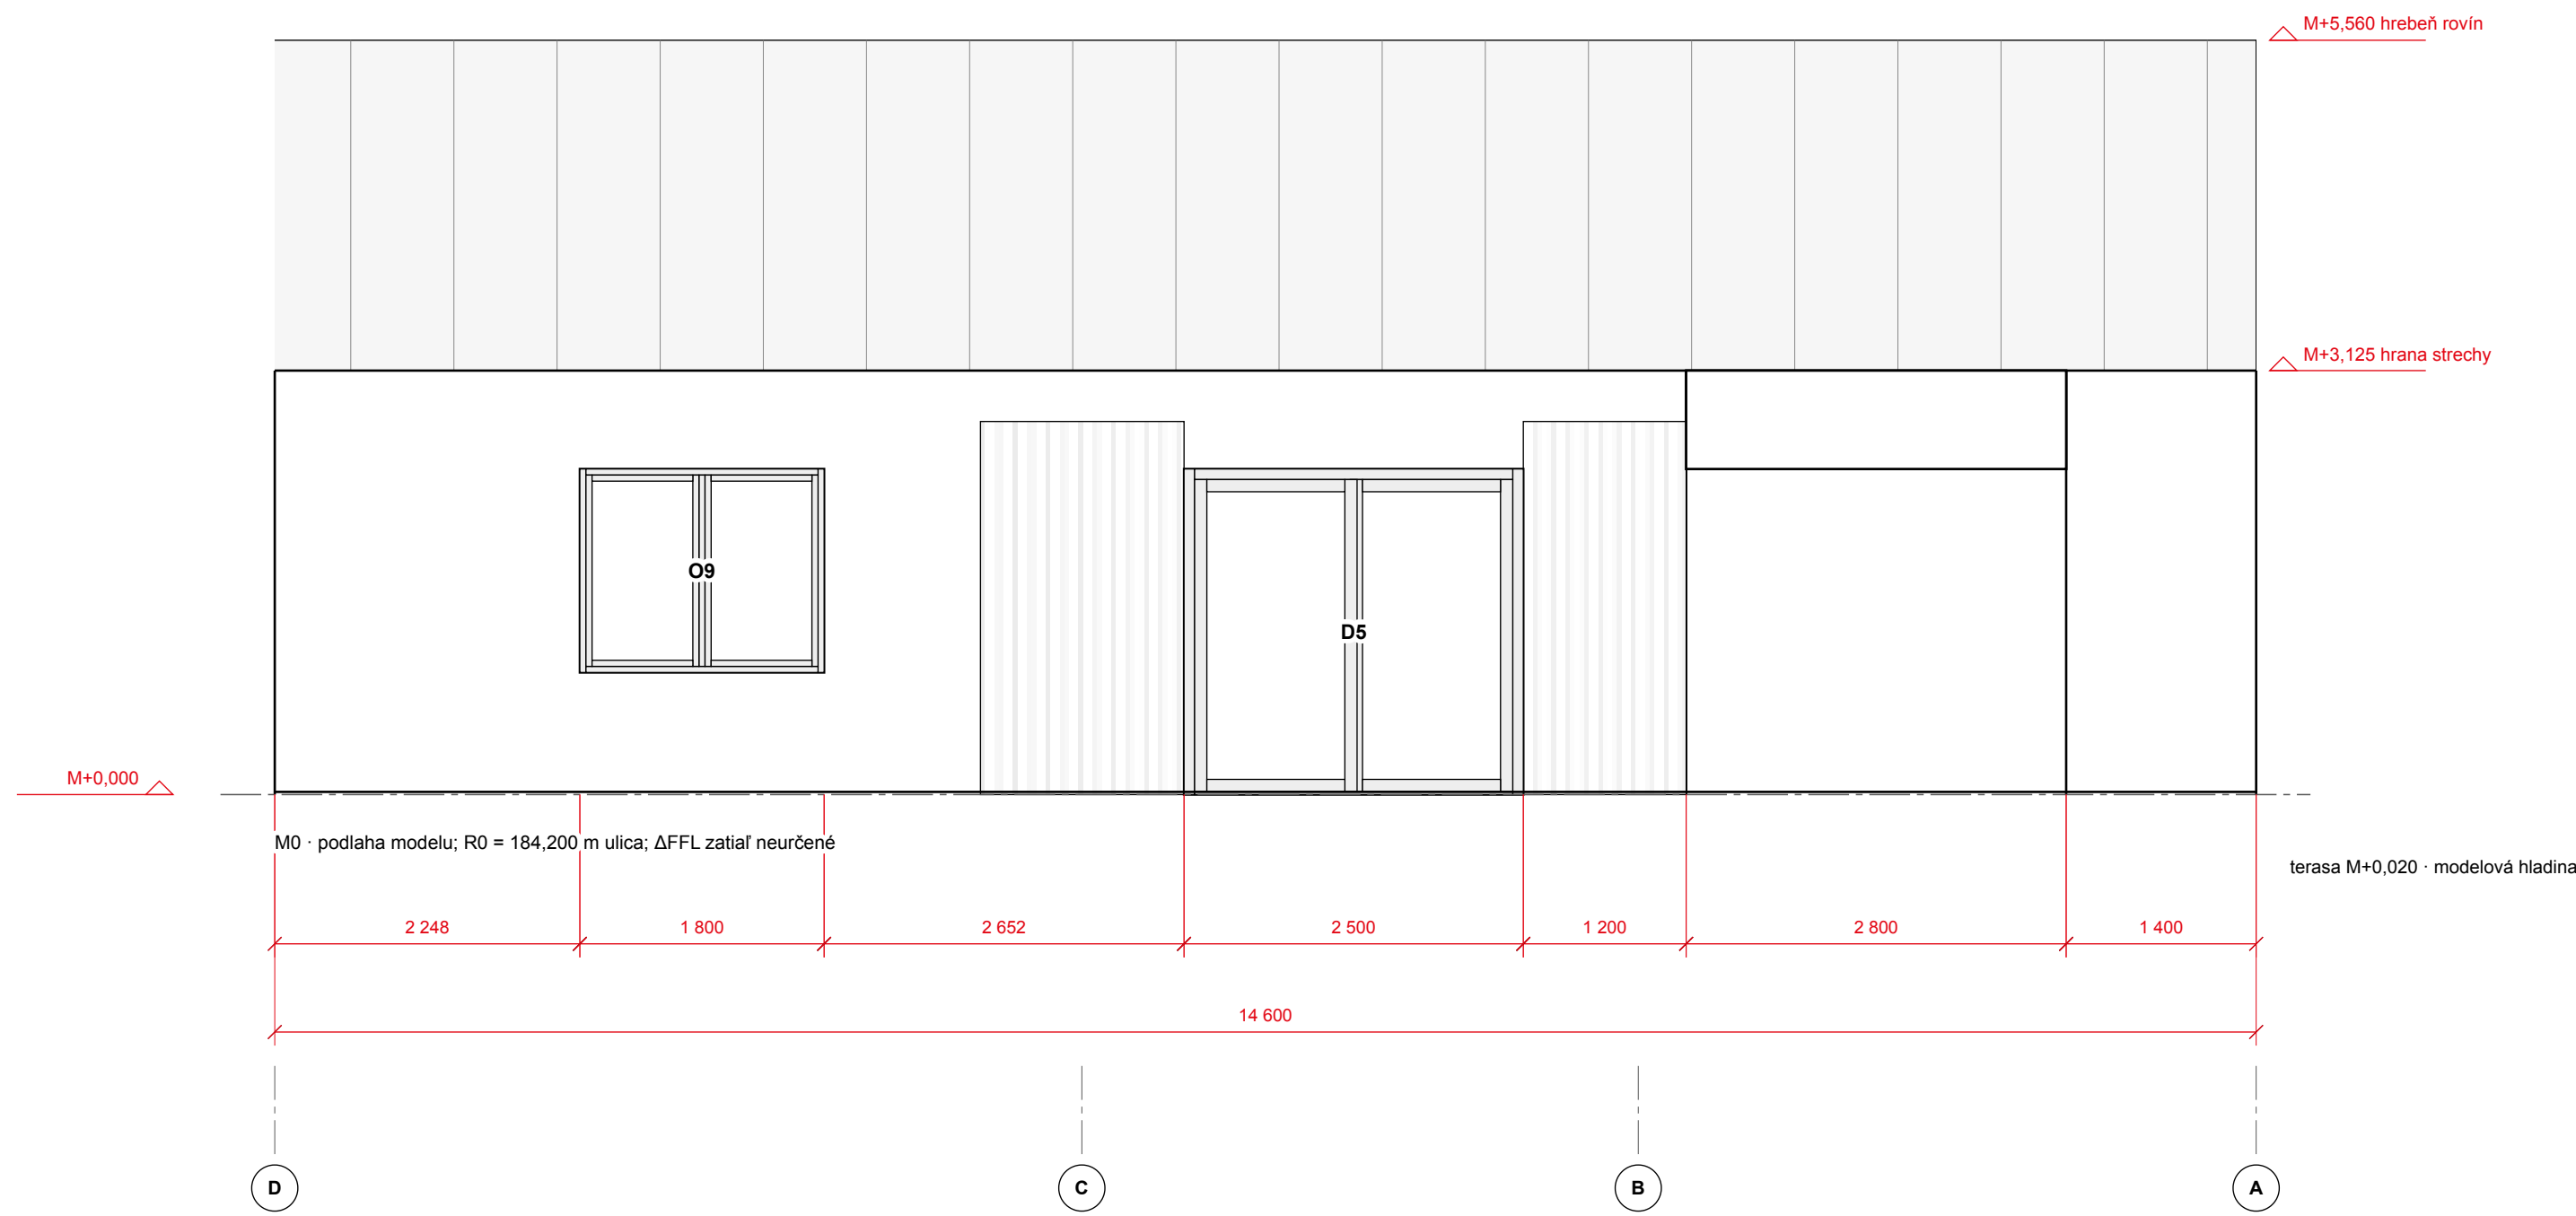

VYTYČOVACIE ÚDAJE OTVOROV TEJTO ROVINY

Kód / identifikátor	Od / do [mm]	Š × V [mm]	Parapet / nadpražie
O9 / Vypĺň otvoru GARDEN-03	X 16 992 / 16 792	1 800 × 1 500	900 / 2 400
D5 / Terasové presklenie 2500	X 11 840 / 14 340	2 500 × 2 400	0 / 2 400

ZNAČKY A MATERIÁLY

- Murivo / keramické prvky
ETICS / minerálna vlna
Betón – len ak je určený návrhom
Drevený obklad

Čiarkovane: prerušené / neurčené konštrukcie.

M = výška k podlahe modelu. Dĺžky v mm.

K ulici RO: z = M + ΔFFL. ΔFFL neurčené.

Obvodový plášť SO30 + TI20: nosné murivo 300 mm a ETICS 200 mm. Voľné piliere SO50: 500 mm plné murivo. Skladby a detaily DT/SK.

KONTROLA TLAČE 100 % - 1 000 mm ≈ 20 mm na papieri

1 : 50 - vypnúť „prispôbiť strane“

NOVOSTAVBA RD BŘEZÍ U MIKULOVA

PARCELA 6012/26 - HLAVNÝ NÁVRH C / B / B

Záhradná (severná) fasáda

R0 = 184,200 m - M0 = PODLAHA MODELU - ΔFFL = M0 - R0 ZATIAĽ NEURČENÉ

Presná modelová projekcia. R05/R06: chýba skutočný terén, sokel, finálne povrchy a realizačné detaily. Rozmery otvorov sú modelové stavebné otvory; výrobný rozmer určí dodávateľ.

STAV

NEVYDANÉ NA REALIZÁCIU

Chýbajúci návrh sa nesmie nahradiť mierkou výkresu.


VYPRACOVAL: digitálne dvojča - bez autorizačnej pečiatky

DÁTUM 2026-09-14 FORMÁT A1 841 × 594 mm MIERKA 1 : 50

ZDROJ 6cd4bc82841b - úplné odtlačky v model-snapshot.json

Západný štít garáže

ROVINA X = 6 440 mm · čítanie klesajúcich súradníc Y

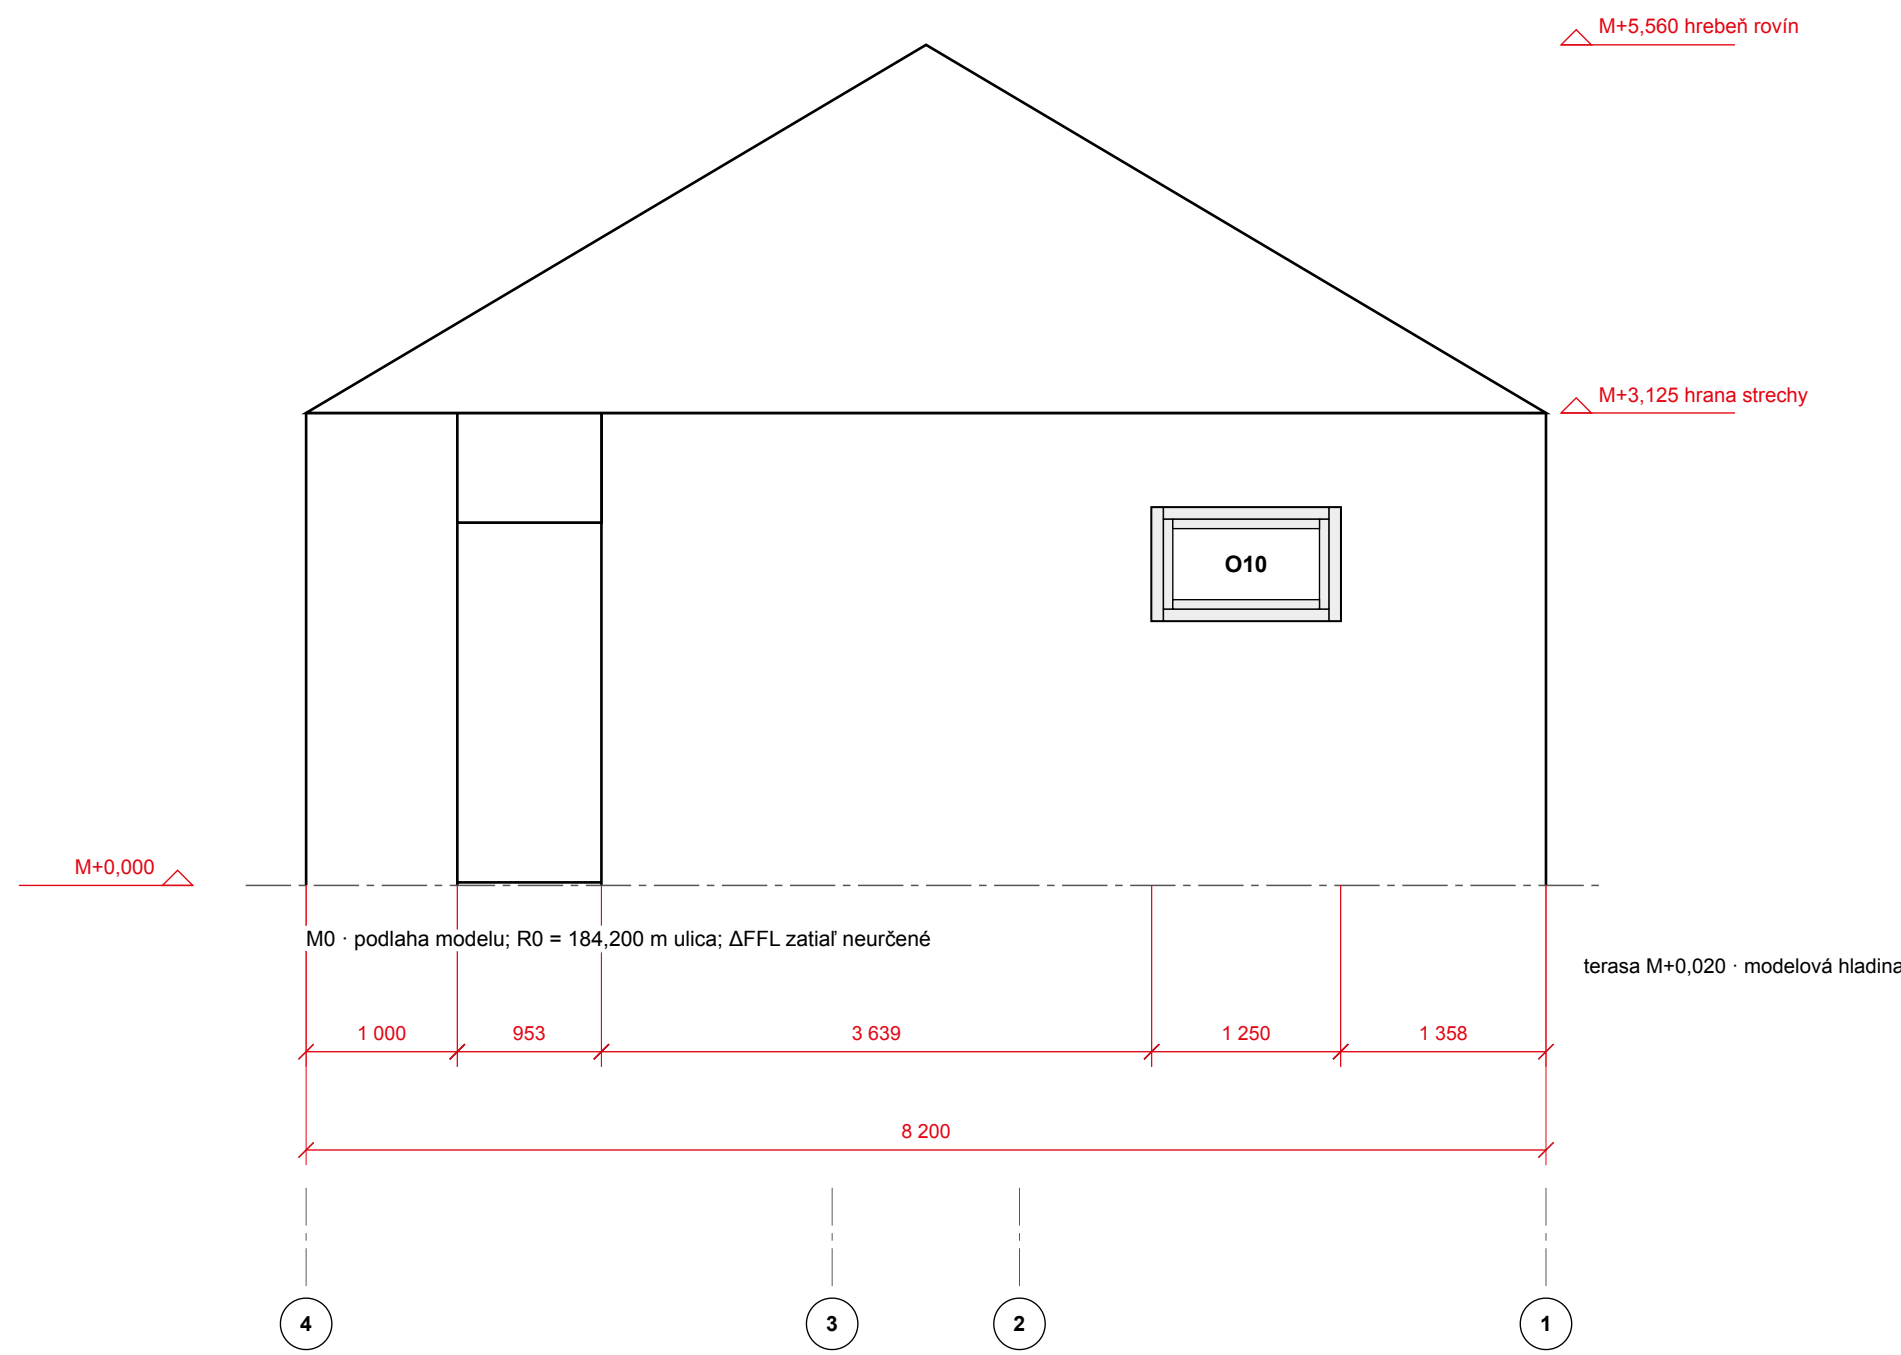

VYTYČOVACIE ÚDAJE OTVOROV TEJTO ROVINY

Kód / identifikátor	Od / do [mm]	Š × V [mm]	Parapet / nadpražie
O10 / Bočné garážové okno WEST-GARAGE-01	Y 4 358 / 5 608	1 250 × 750	1 750 / 2 500

ZNAČKY A MATERIÁLY

- Murivo / keramické prvky
 ETICS / minerálna vlna
 Betón – len ak je určený návrhom
 Drevený obklad

Čiarkovane: prerušené / neurčené konštrukcie.

M = výška k podlahe modelu. Dĺžky v mm.

K ulici R0: z = M + ΔFFL. ΔFFL neurčené.

Obvodový plášť SO30 + TI20: nosné murivo 300 mm a ETICS 200 mm. Vojné piliere SO50: 500 mm plné murivo. Skladby a detaily DT/SK.

KONTROLA TLAČE 100 % - 1 000 mm ≈ 20 mm na papieri

1 : 50 - vypnúť „prispôbiť strane“

NOVOSTAVBA RD BŘEZÍ U MIKULOVA

PARCELA 6012/26 · HLAVNÝ NÁVRH C / B / B

Západný štít garáže

R0 = 184,200 m · M0 = PODLAHA MODELU · ΔFFL = M0 – R0 ZATIAĽ NEURČENÉ

Presná modelová projekcia. R05/R06: chýba skutočný terén, sokel, finálne povrchy a realizačné detaily. Rozmery otvorov sú modelové stavebné otvory; výrobný rozmer určí dodávateľ.

STAV

NEVYDANÉ NA REALIZÁCIU

Chýbajúci návrh sa nesmie nahradiť mierkou výkresu.


VYPRACOVAL: digitálne dvojča · bez autorizačnej pečiatky

DÁTUM 2026-09-14 FORMÁT A1 841 × 594 mm MIERKA 1 : 50

ZDROJ 6cd4bc82841b · úplné odtlačky v model-snapshot.json

Západná stena krídla

ROVINA X = 21 040 mm · čítanie klesajúcich súradníc Y

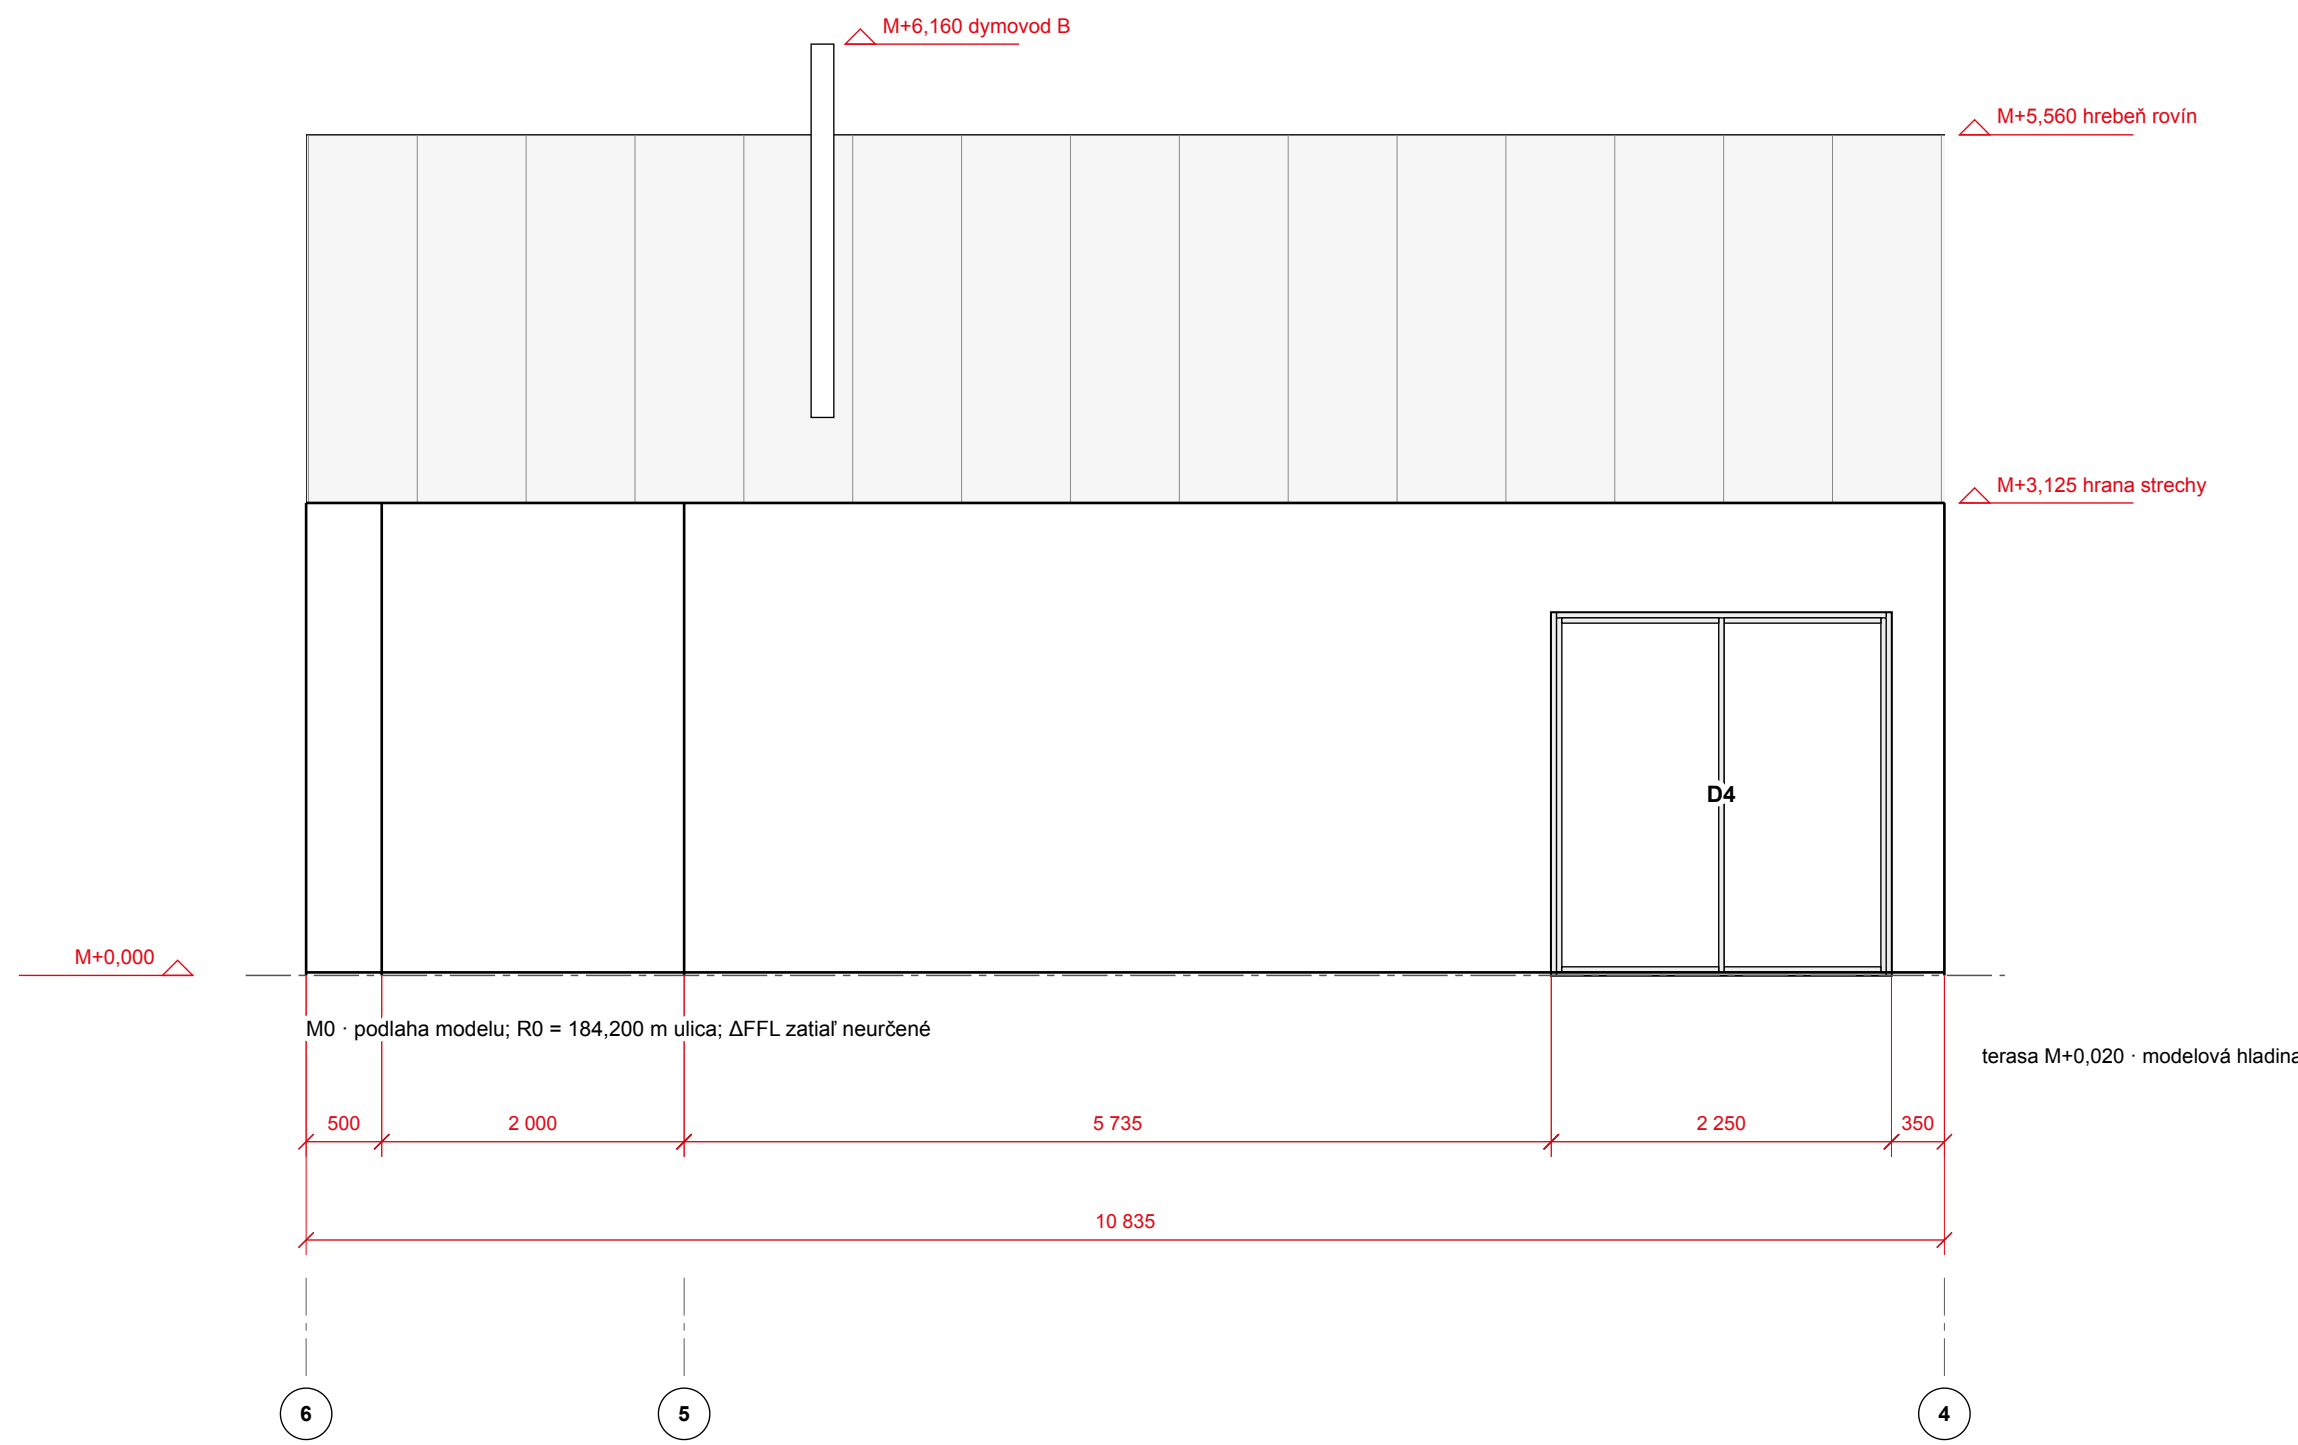

VYTYČOVACIE ÚDAJE OTVOROV TEJTO ROVINY

Kód / identifikátor	Od / do [mm]	Š × V [mm]	Parapet / nadpražie
D4 / Terasové posuvné presklenie 2 250	Y 11 550 / 13 800	2 250 × 2 400	0 / 2 400

ZNAČKY A MATERIÁLY

- Murivo / keramické prvky
- ETICS / minerálna vlna
- Betón – len ak je určený návrhom
- Drevený obklad

Čiarkovane: prerušené / neurčené konštrukcie.

M = výška k podlahe modelu. Dĺžky v mm.

K ulici R0: z = M + ΔFFL. ΔFFL neurčené.

Obvodový plášť SO30 + TI20: nosné murivo 300 mm a ETICS 200 mm. Voľné piliere SO50: 500 mm plné murivo. Skladby a detaily DT/SK.

KONTROLA TLAČE 100 % - 1 000 mm ≈ 20 mm na papieri

1 : 50 - vypnúť „prispôbiť strane“

NOVOSTAVBA RD BŘEZÍ U MIKULOVA

PARCELA 6012/26 · HLAVNÝ NÁVRH C / B / B

Západná stena krídla

R0 = 184,200 m · M0 = PODLAHA MODELU · ΔFFL = M0 – R0 ZATIAĽ NEURČENÉ

Presná modelová projekcia. R05/R06: chýba skutočný terén, sokel, finálne povrchy a realizačné detaily. Rozmery otvorov sú modelové stavebné otvory; výrobný rozmer určí dodávateľ.

STAV

NEVYDANÉ NA REALIZÁCIU

Chýbajúci návrh sa nesmie nahradiť mierkou výkresu.


VYPRACOVAL: digitálne dvojča · bez autorizačnej pečiatky

DÁTUM 2026-09-14 FORMÁT A1 841 × 594 mm MIERKA 1 : 50

ZDRCJ 6cd4bc82841b · úplné odtlačky v model-snapshot.json

Štít krídla · portál krytej terasy


ROVINA Y = 22 035 mm · čítanie klesajúcich súradníc X

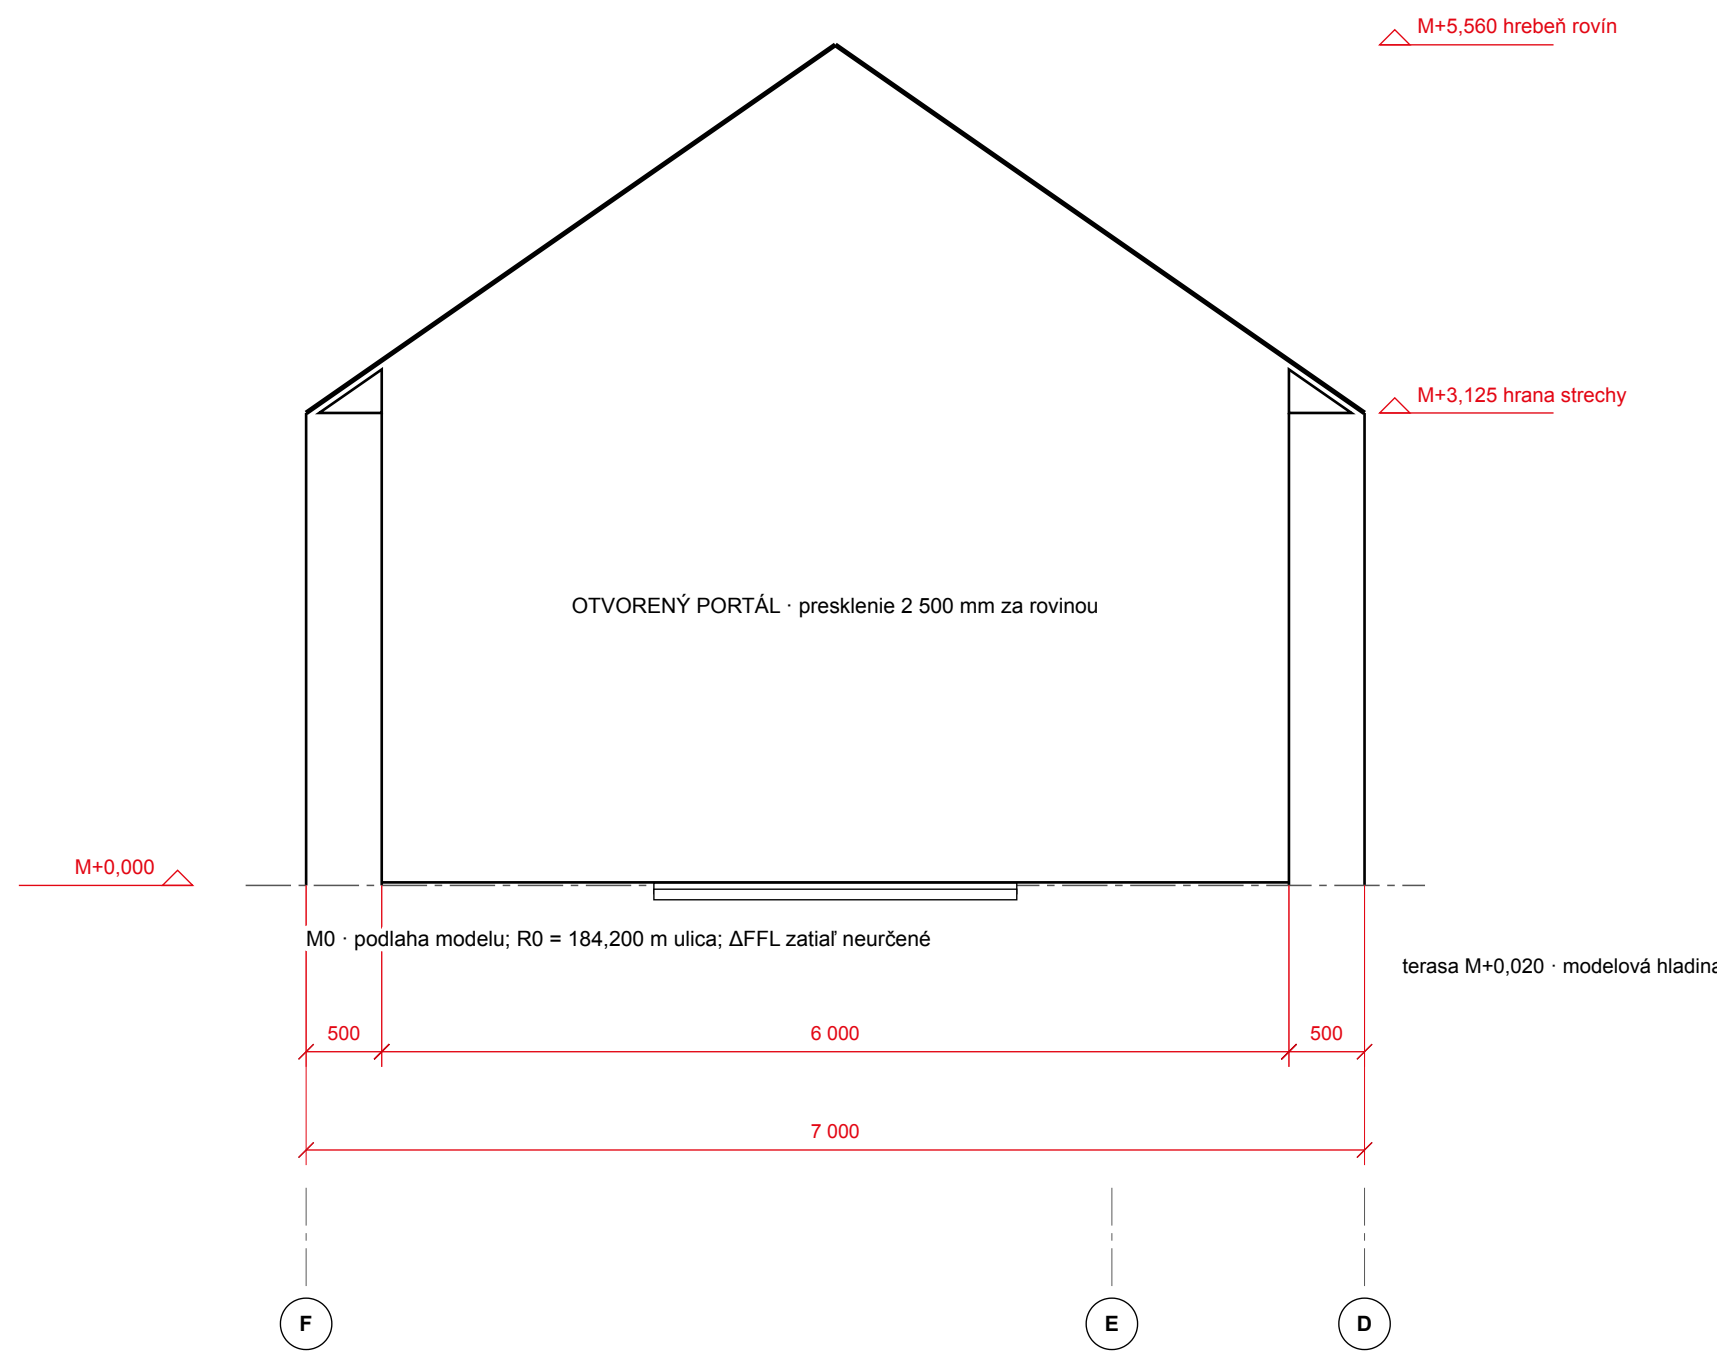

VYTYČOVACIE ÚDAJE OTVOROV TEJTO ROVINY

Kód / identifikátor	Od / do [mm]	Š × V [mm]	Parapet / nadpražie
---------------------	--------------	------------	---------------------

MODELOVÉ STUPNE TERASY · PROFIL 1 : 5

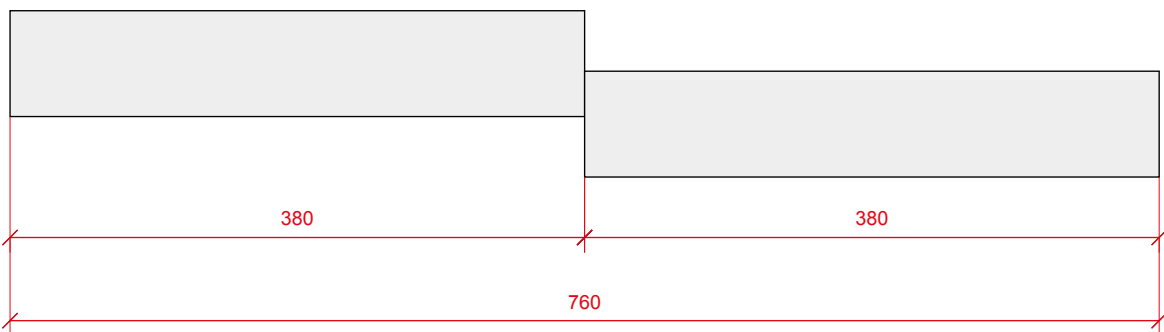

Stupeň	Horné / dolné Z	Hrúbka
1	M+0,015 / M-0,055	70 mm
2	M-0,025 / M-0,095	70 mm

Úrovne modelu; nie hotový návrh schodiska. Terén, založenie a napojenie sú otvorené.

ZNAČKY A MATERIÁLY

- Murivo / keramické prvky
- ETICS / minerálna vlna
- Betón – len ak je určený návrhom
- Drevený obklad

Čiarkovane: prerušené / neurčené konštrukcie.

M = výška k podlahe modelu. Dĺžky v mm.

K ulici R0: z = M + ΔFFL. ΔFFL neurčené.

Obvodový plášť SO30 + TI20: nosné murivo 300 mm a ETICS 200 mm. Voľné piliere SO50: 500 mm plné murivo. Skladby a detaily DT/SK.

KONTROLA TLAČE 100 % - 1 000 mm ≈ 20 mm na papieri

1 : 50 - vypnúť „prispôbiť strane“

NOVOSTAVBA RD BŘEZÍ U MIKULOVA

PARCELA 6012/26 · HLAVNÝ NÁVRH C / B / B

Štít krídla · portál krytej terasy

R0 = 184,200 m · M0 = PODLAHA MODELU · ΔFFL = M0 – R0 ZATIAĽ NEURČENÉ

Presná modelová projekcia. R05/R06: chýba skutočný terén, sokel, finálne povrchy a realizačné detaily. Rozmery otvorov sú modelové stavebné otvory; výrobný rozmer určí dodávateľ.

STAV

NEVYDANÉ NA REALIZÁCIU

Chýbajúci návrh sa nesmie nahradiť mierkou výkresu.


VYPRACOVAL: digitálne dvojča · bez autorizačnej pečiatky

DÁTUM 2026-09-14 FORMÁT A1 841 × 594 mm MIERKA 1 : 50

ZDROJ 6cd4bc82841b · úplné odtlačky v model-snapshot.json

Krytá terasa · zasklená stena

ROVINA Y = 19 535 mm · čítanie klesajúcich súradníc X

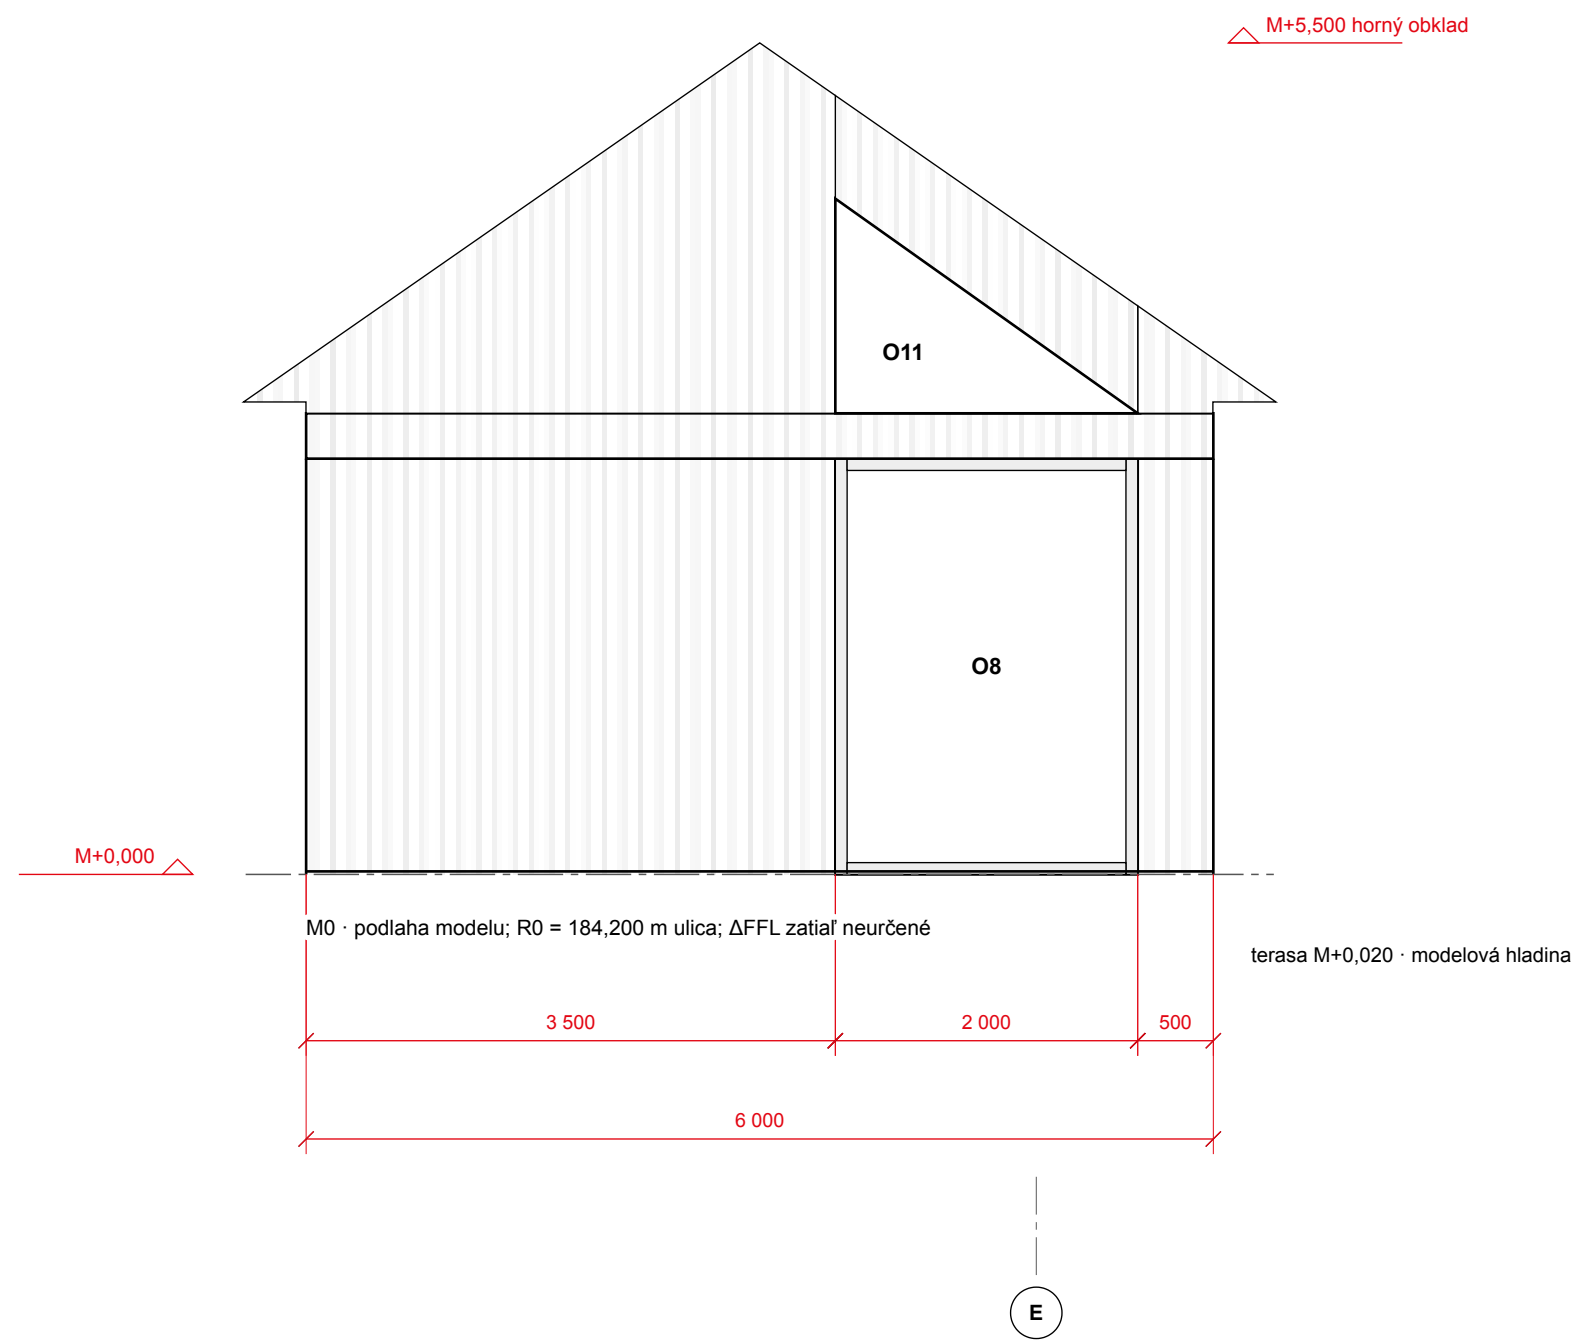


O11 · svetlík nad rovinou pôdorysu

X 22 040–24 040 · spodná hrana M+3,050

vrchol M+4,470 · presný model 4 469,65 mm

VRATNÉ LÍCE KRYTEJ TERASY

X 27 540 · Y 19 535–22 035

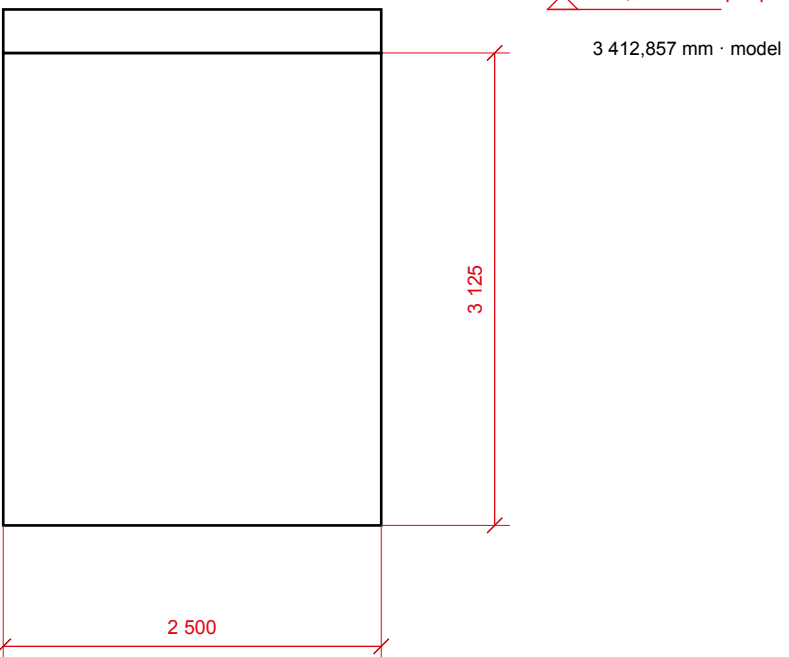

VYTYČOVACIE ÚDAJE OTVOROV TEJTO ROVINY

Kód / identifikátor	Od / do [mm]	Š × V [mm]	Parapet / nadpražie
O8 / Krytá terasa-glazing	X 22 040 / 24 040	2 000 × 2 750	0 / 2 750

ZNAČKY A MATERIÁLY

	Murivo / keramické prvky
	ETICS / minerálna vlna
	Betón – len ak je určený návrhom
	Drevený obklad

Čiarkovane: prerušené / neurčené konštrukcie.

M = výška k podlahe modelu. Dĺžky v mm.

K ulici R0: z = M + ΔFFL. ΔFFL neurčené.

Obvodový plášť SO30 + TI20: nosné murivo 300 mm a ETICS 200 mm. Voľné piliere SO50: 500 mm plné murivo. Skladby a detaily DT/SK.

KONTROLA TLAČE 100 % - 1 000 mm ≈ 20 mm na papieri

1 : 50 - vypnúť „prispôbiť strane“

NOVOSTAVBA RD BŘEZÍ U MIKULOVA

PARCELA 6012/26 · HLAVNÝ NÁVRH C / B / B

Krytá terasa · zasklená stena

R0 = 184,200 m · M0 = PODLAHA MODELU · ΔFFL = M0 – R0 ZATIAĽ NEURČENÉ

Presná modelová projekcia. R05/R06: chýba skutočný terén, sokel, finálne povrchy a realizačné detaily. Rozmery otvorov sú modelové stavebné otvory; výrobný rozmer určí dodávateľ.

STAV

NEVYDANÉ NA REALIZÁCIU

Chýbajúci návrh sa nesmie nahradiť mierkou výkresu.


VYPRACOVAL: digitálne dvojča · bez autorizačnej pečiatky

DÁTUM 2026-09-14 FORMÁT A1 841 × 594 mm MIERKA 1 : 50

ZDROJ 6c44bc82841b · úplné odtlačky v model-snapshot.json


Lodžia · zadná stena garáže

ROVINA Y = 9 247 mm · čítanie klesajúcich súradníc X

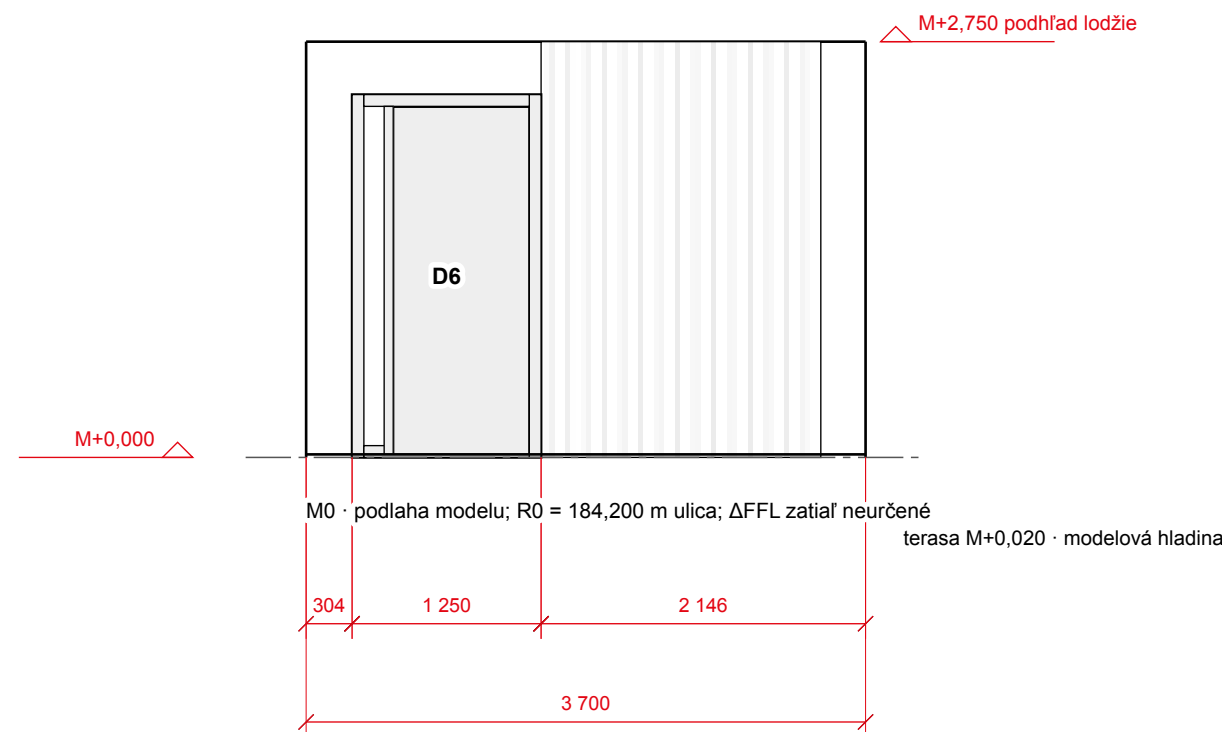

BOČNÉ LÍCE LODŽIE

X 10 640 · Y 9 247–11 200

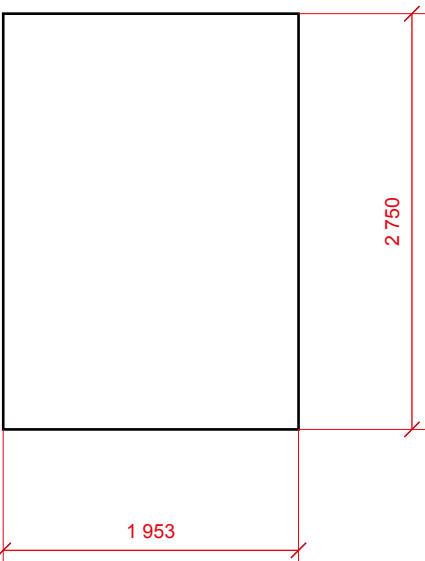

VYTYČOVACIE ÚDAJE OTVOROV TEJTO ROVINY

Kód / identifikátor	Od / do [mm]	Š × V [mm]	Parapet / nadpražie
D6 / LOGGIA-DOOR	X 9 086 / 10 336	1 250 × 2 400	0 / 2 400

ZNAČKY A MATERIÁLY

- Murivo / keramické prvky
- ETICS / minerálna vlna
- Betón – len ak je určený návrhom
- Drevený obklad

Čiarkovane: prerušené / neurčené konštrukcie.

M = výška k podlahe modelu. Dĺžky v mm.

K ulici R0: z = M + ΔFFL. ΔFFL neurčené.

Obvodový plášť SO30 + TI20: nosné murivo 300 mm a ETICS 200 mm. Voľné piliere SO50: 500 mm plné murivo. Skladby a detaily DT/SK.

Bočná stena lodžie: X 10 640, Y 9 247–11 200; bez otvorov.

KONTROLA TLAČE 100 % - 1 000 mm ≈ 20 mm na papieri

1 : 50 - vypnúť „prispôbiť strane“

NOVOSTAVBA RD BŘEZÍ U MIKULOVA

PARCELA 6012/26 · HLAVNÝ NÁVRH C / B / B

Lodžia · zadná stena garáže

R0 = 184,200 m · M0 = PODLAHA MODELU · ΔFFL = M0 – R0 ZATIAĽ NEURČENÉ

Presná modelová projekcia. R05/R06: chýba skutočný terén, sokel, finálne povrchy a realizačné detaily. Rozmery otvorov sú modelové stavebné otvory; výrobný rozmer určí dodávateľ.

STAV

NEVYDANÉ NA REALIZÁCIU

Chýbajúci návrh sa nesmie nahradiť mierkou výkresu.


VYPRACOVAL: digitálne dvojča · bez autorizačnej pečiatky

DÁTUM 2026-09-14 FORMÁT A1 841 × 594 mm MIERKA 1 : 50

ZDROJ 6cd4bc82841b · úplné odtlačky v model-snapshot.json

A-A · Pozdĺžny rez krídlom

X = 24 540 mm : stopa na D1.1.002-C-RE · Pracovňa, H200, kúpeľňa, WC, nosná stena kuchyne, hrebeň obývačky a krytá terasa.

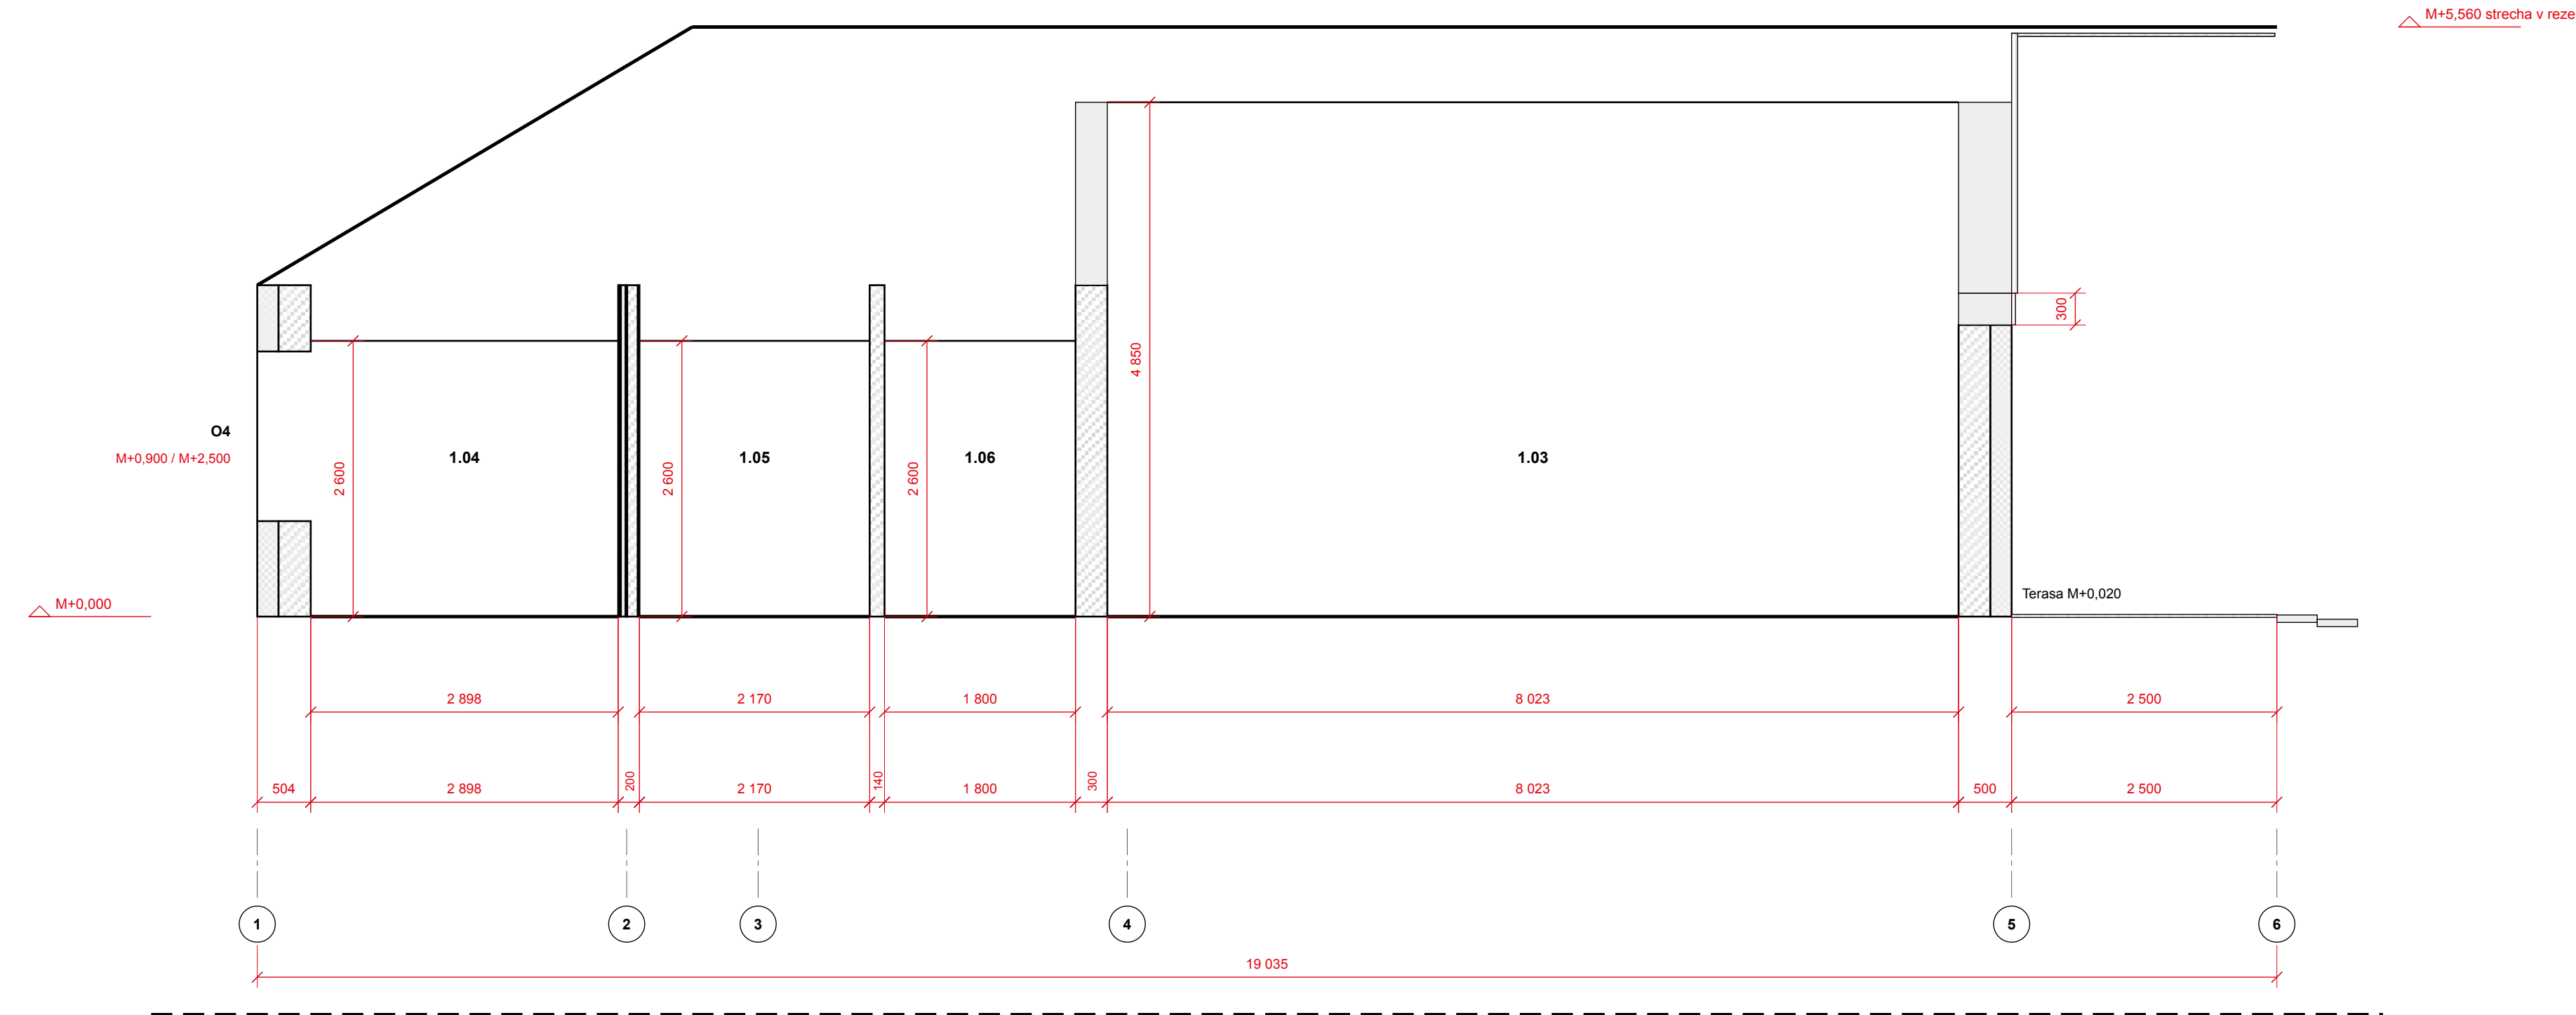

POD NOSNOU DOSKOU SA NIČ NEPREBERÁ Z ARCHÍVNEJ STATIKY.

Nové zadanie: horný monolit 350 × 600 mm, vnútorné rebrá a doska 150–200 mm; detail ZA-02. Nivelačia, výstuž a nosná skladba zatiaľ neurčené. R0 = 184,200 m na ulici; všetky výšky M sú k pôvodnej podlahe modelu.

KOORDINÁCIA NOVÝCH KONŠTRUKCIÍ

Prvok	Záväzný geometrický podklad / chýbajúci návrh
Podlaha M0	Vodovod a kanalizácia nad nosnou doskou. Podlahové vykurovanie mimo garáže, technickej a sprchy; TZ-01. Bez dodatočných vrtov do dosky.
Drevený strop a povala	Povala iba na odkladanie, bez betónovej stropnej dosky/nadbetónávky. Skladovacie a bodové zariadenia musí určiť výpočet. Katedrála 1.03 zostáva otvorená, svetlé výšky 2 750 / 4 850 mm.
Nosné línie a základy	Nový monolitický návrh podľa ZA-02, geotechniky a reakcií nosnej sústavy. Výstuž, rebrá a pracovné škáry sa nepreberajú zo starého projektu.

KONTROLA TLAČE 100 % - 1 000 mm ≈ 20 mm na papieri

1 : 50 - vypnúť „prispôbiť strane“

NOVOSTAVBA RD BŘEZÍ U MIKULOVA

PARCELA 6012/26 · HLAVNÝ NÁVRH C / B / B

A-A · Pozdĺžny rez krídlom

R0 = 184,200 m · M0 = PODLAHA MODELU · ΔFFL = M0 – R0 ZATIAĽ NEURČENÉ


Rozmery nadzemnej architektonickej geometrie z modelu. Základy, nosná skladba podlahy a strechy, vence a krov zostávajú otvorené R01-R04; list nie je realizačný rez.

PÁS NAD PRESKLENÍM · OBAL Z MODELU

Rozmer / úroveň	Hodnota
Dĺžka × hĺbka × výška	6 000 × 500 × 300 mm
Spodok / vrch	M+2,750 / M+3,050
Rozsah v reze	Y 19 035–19 535

R04: nový nosný materiál, výstuž a kotvenie. Vonkajší plášť pásu je drevený obklad; šrafo nepredpisuje betón.

MODELOVÉ STUPNE TERASY · PROFIL 1 : 5

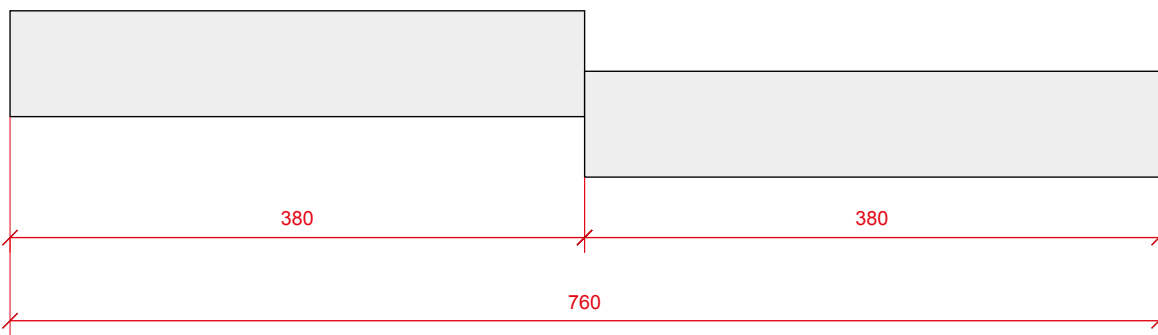

Stupeň	Horné / dolné Z	Hrúbka
1	M+0,015 / M-0,055	70 mm
2	M-0,025 / M-0,095	70 mm

Úrovne modelu; nie hotový návrh schodiska. Terén, založenie a napojenie sú otvorené.

ZNAČKY A MATERIÁLY

- Murivo / keramické prvky
- ETICS / minerálna vlna
- Betón – len ak je určený návrhom
- Drevený obklad

Čiarkovane: prerušené / neurčené konštrukcie.

M = výška k podlahe modelu. Dĺžky v mm.

K ulici R0: z = M + ΔFFL. ΔFFL neurčené.

STAV

NEVYDANÉ NA REALIZÁCIU

Chýbajúci návrh sa nesmie nahradiť mierkou výkresu.


VYPRACOVAL: digitálne dvojča · bez autorizačnej pečiatky

DÁTUM 2026-09-14 FORMÁT A1 841 × 594 mm MIERKA 1 : 50

ZDROJ 6cd4bc82841b · úplné odtlačky v model-snapshot.json

B-B · Pričný rez katedrálovým stropom

Y = 18 620 mm : stopa na D1.1.002-C-RE · Obývačka 1.03, skutočný profil podhľadu, dymovod B a celá západná terasa.

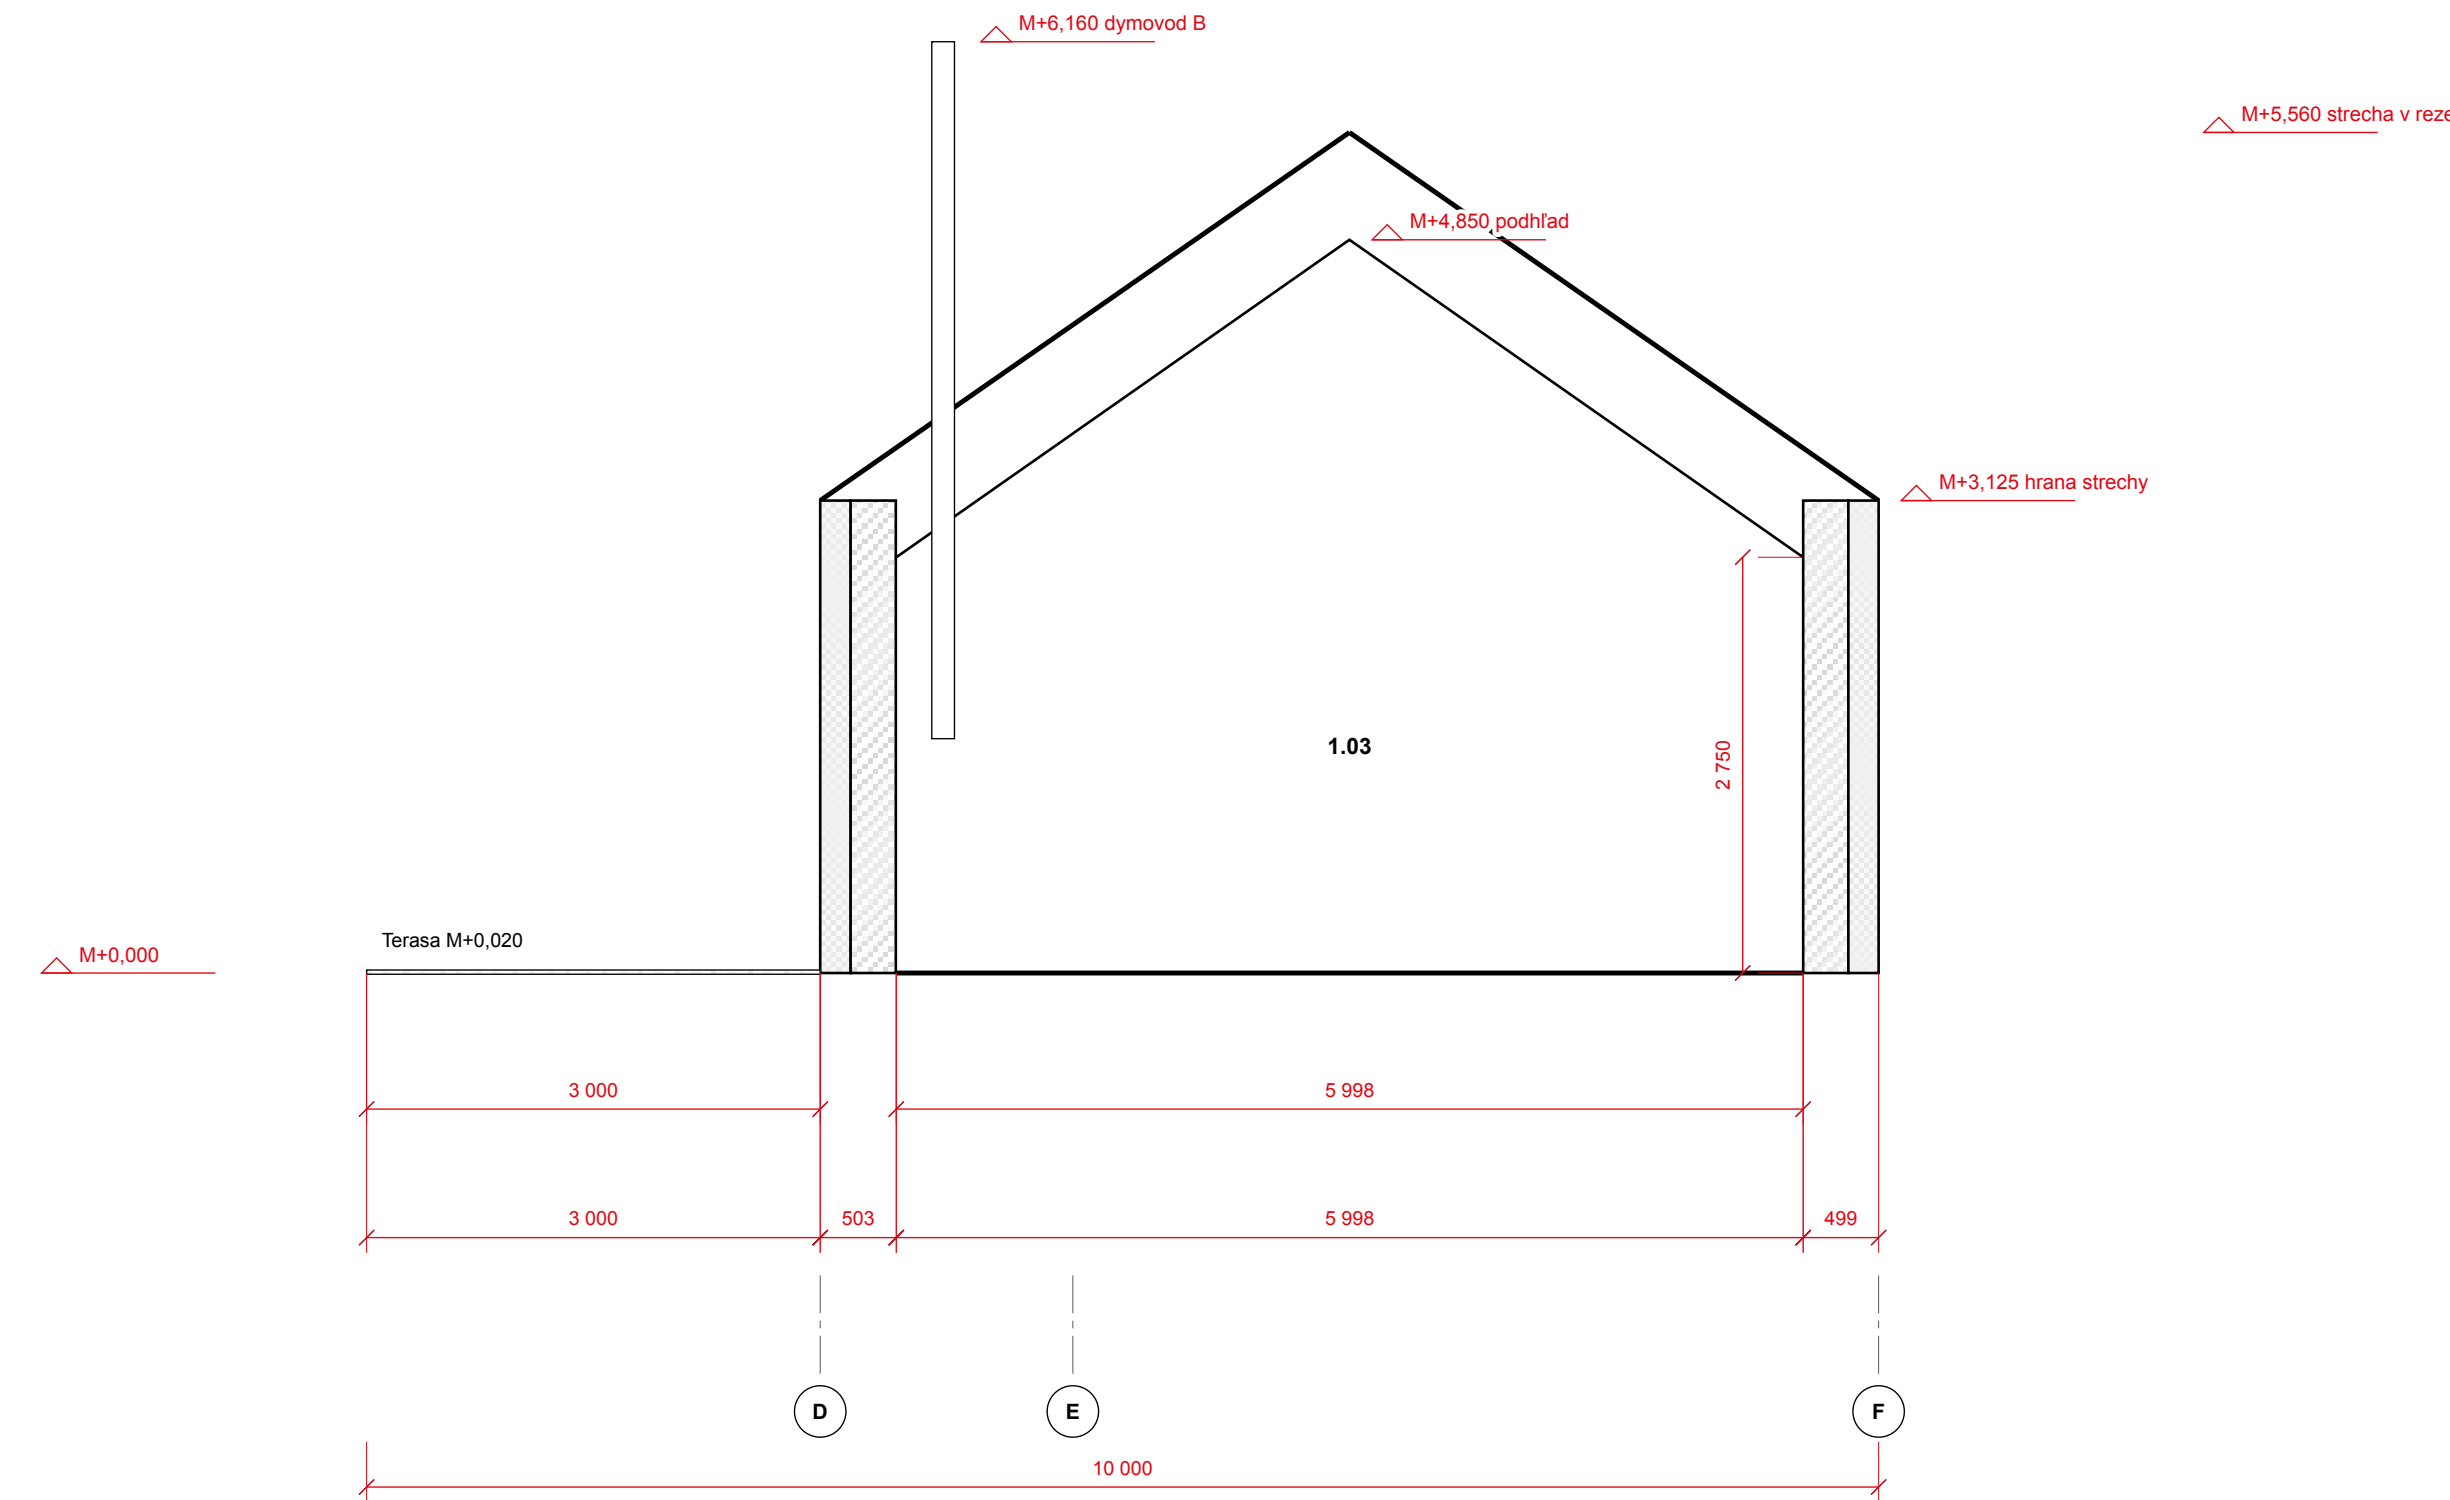

POD NOSNOU DOSKOU SA NIČ NEPREBERÁ Z ARCHÍVNEJ STATIKY.

Nové zadanie: horný monolit 350 × 600 mm, vnútorné rebrá a doska 150–200 mm; detail ZA-02. Nivelačia, výstuž a nosná skladba zatiaľ neurčené. R0 = 184,200 m na ulici; všetky výšky M sú k pôvodnej podlahe modelu.

KOORDINÁCIA NOVÝCH KONŠTRUKCIÍ

Prvok	Záväzný geometrický podklad / chýbajúci návrh
Podlaha M0	Vodovod a kanalizácia nad nosnou doskou. Podlahové vykurovanie mimo garáže, technickej a sprchy; TZ-01. Bez dodatočných vrtov do dosky.
Drevený strop a povala	Povala iba na odkladanie, bez betónovej stropnej dosky/nadbetónávky. Skladovacie a bodové zariadenia musí určiť výpočet. Katedrála 1.03 zostáva otvorená, svetlé výšky 2 750 / 4 850 mm.
Nosné línie a základy	Nový monolitický návrh podľa ZA-02, geotechniky a reakcií nosnej sústavy. Výstuž, rebrá a pracovné škáry sa nepreberajú zo stareho projektu.

ZNAČKY A MATERIÁLY

- Murivo / keramické prvky
- ETICS / minerálna vlna
- Betón – len ak je určený návrhom
- Drevený obklad

Čiarkovane: prerušené / neurčené konštrukcie.
M = výška k podlahe modelu. Dĺžky v mm.
K ulici R0: z = M + ΔFFL. ΔFFL neurčené.

KONTROLA TLAČE 100 % - 1 000 mm ≈ 20 mm na papieri

1 : 50 - vypnúť „prispôbiť strane“

NOVOSTAVBA RD BŘEZÍ U MIKULOVA

PARCELA 6012/26 · HLAVNÝ NÁVRH C / B / B

B-B · Pričný rez katedrálovým stropom

R0 = 184,200 m · M0 = PODLAHA MODELU · ΔFFL = M0 – R0 ZATIAĽ NEURČENÉ

Rozmery nadzemnej architektonickej geometrie z modelu. Základy, nosná skladba podlahy a strechy, vence a krov zostávajú otvorené R01-R04; list nie je realizačný rez.

STAV

NEVYDANÉ NA REALIZÁCIU

Chýbajúci návrh sa nesmie nahradiť mierkou výkresu.


VYPRACOVAL: digitálne dvojča · bez autorizačnej pečiatky

DÁTUM 2026-09-14 FORMÁT A1 841 × 594 mm MIERKA 1 : 50

ZDROJ 6cd4bc82841b · úplné odtlačky v model-snapshot.json

C-C · Pričný rez hlavným traktom

Y = 5 000 mm - stopa na D1.1.002-C-RE - Tretí rez je potrebný pre garáž, nočné krídlo, rozdielne podlahy a nosné línie.

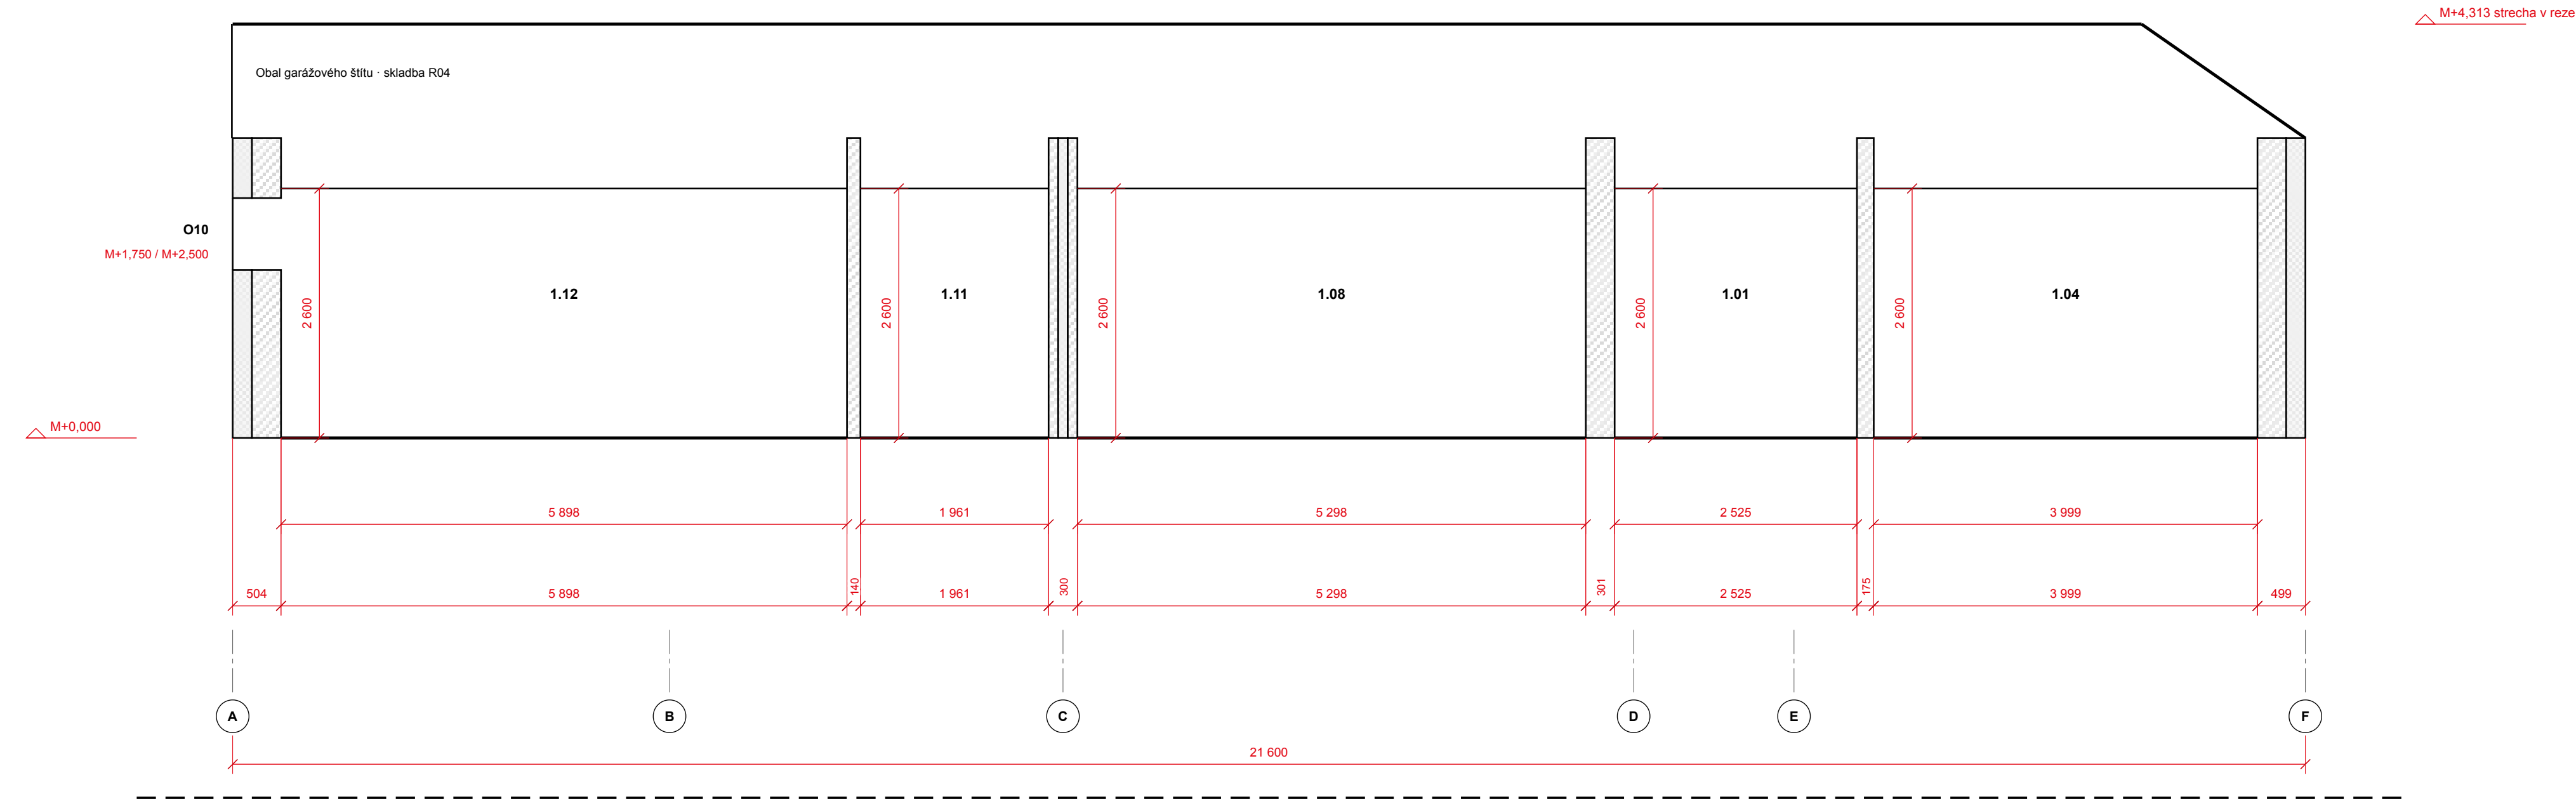

POD NOSNOU DOSKOU SA NIČ NEPREBERÁ Z ARCHÍVNEJ STATIKY.

Nové zadanie: horný monolit 350 × 600 mm, vnútorné rebrá a doska 150–200 mm; detail ZA-02. Nivelačia, výstuž a nosná skladba zatiaľ neurčené. R0 = 184,200 m na ulici; všetky výšky M sú k pôvodnej podlahe modelu.

KOORDINÁCIA NOVÝCH KONŠTRUKCIÍ

Prvok	Záväzný geometrický podklad / chýbajúci návrh
Podlaha M0	Vodovod a kanalizácia nad nosnou doskou. Podlahové vykurovanie mimo garáže, technickej a sprchy; TZ-01. Bez dodatočných vrtov do dosky.
Drevený strop a povala	Povala iba na odkladanie, bez betónovej stropnej dosky/nadbetonávky. Skladovacie a bodové zariadenia musí určiť výpočet. Katedrála 1.03 zostáva otvorená, svetlé výšky 2 750 / 4 850 mm.
Nosné línie a základy	Nový monolitický návrh podľa ZA-02, geotechniky a reakcií nosnej sústavy. Výstuž, rebrá a pracovné škáry sa nepreberajú zo starého projektu.

ZNAČKY A MATERIÁLY

- Murivo / keramické prvky
- ETICS / minerálna vlna
- Betón – len ak je určený návrhom
- Drevený obklad

Čiarkovane: prerušené / neurčené konštrukcie.

M = výška k podlahe modelu. Dĺžky v mm.

K ulici R0: z = M + ΔFFL. ΔFFL neurčené.

KONTROLA TLAČE 100 % - 1 000 mm ≈ 20 mm na papieri

1 : 50 - vypnúť „prispôbiť strane“

NOVOSTAVBA RD BŘEZÍ U MIKULOVA

PARCELA 6012/26 · HLAVNÝ NÁVRH C / B / B

C-C · Pričný rez hlavným traktom

R0 = 184,200 m · M0 = PODLAHA MODELU · ΔFFL = M0 – R0 ZATIAĽ NEURČENÉ

Rozmery nadzemnej architektonickej geometrie z modelu. Základy, nosná skladba podlahy a strechy, vence a krov zostávajú otvorené R01-R04; list nie je realizačný rez.

STAV

NEVYDANÉ NA REALIZÁCIU


Chýbajúci návrh sa nesmie nahradiť mierkou výkresu.

VYPRACOVAL: digitálne dvojča · bez autorizačnej pečiatky

DÁTUM 2026-09-14 FORMÁT A1 841 × 594 mm MIERKA 1 : 50

ZDROJ 6cd4bc82841b · úplné odtlačky v model-snapshot.json

Základy · nosné línie a ťažké priečky

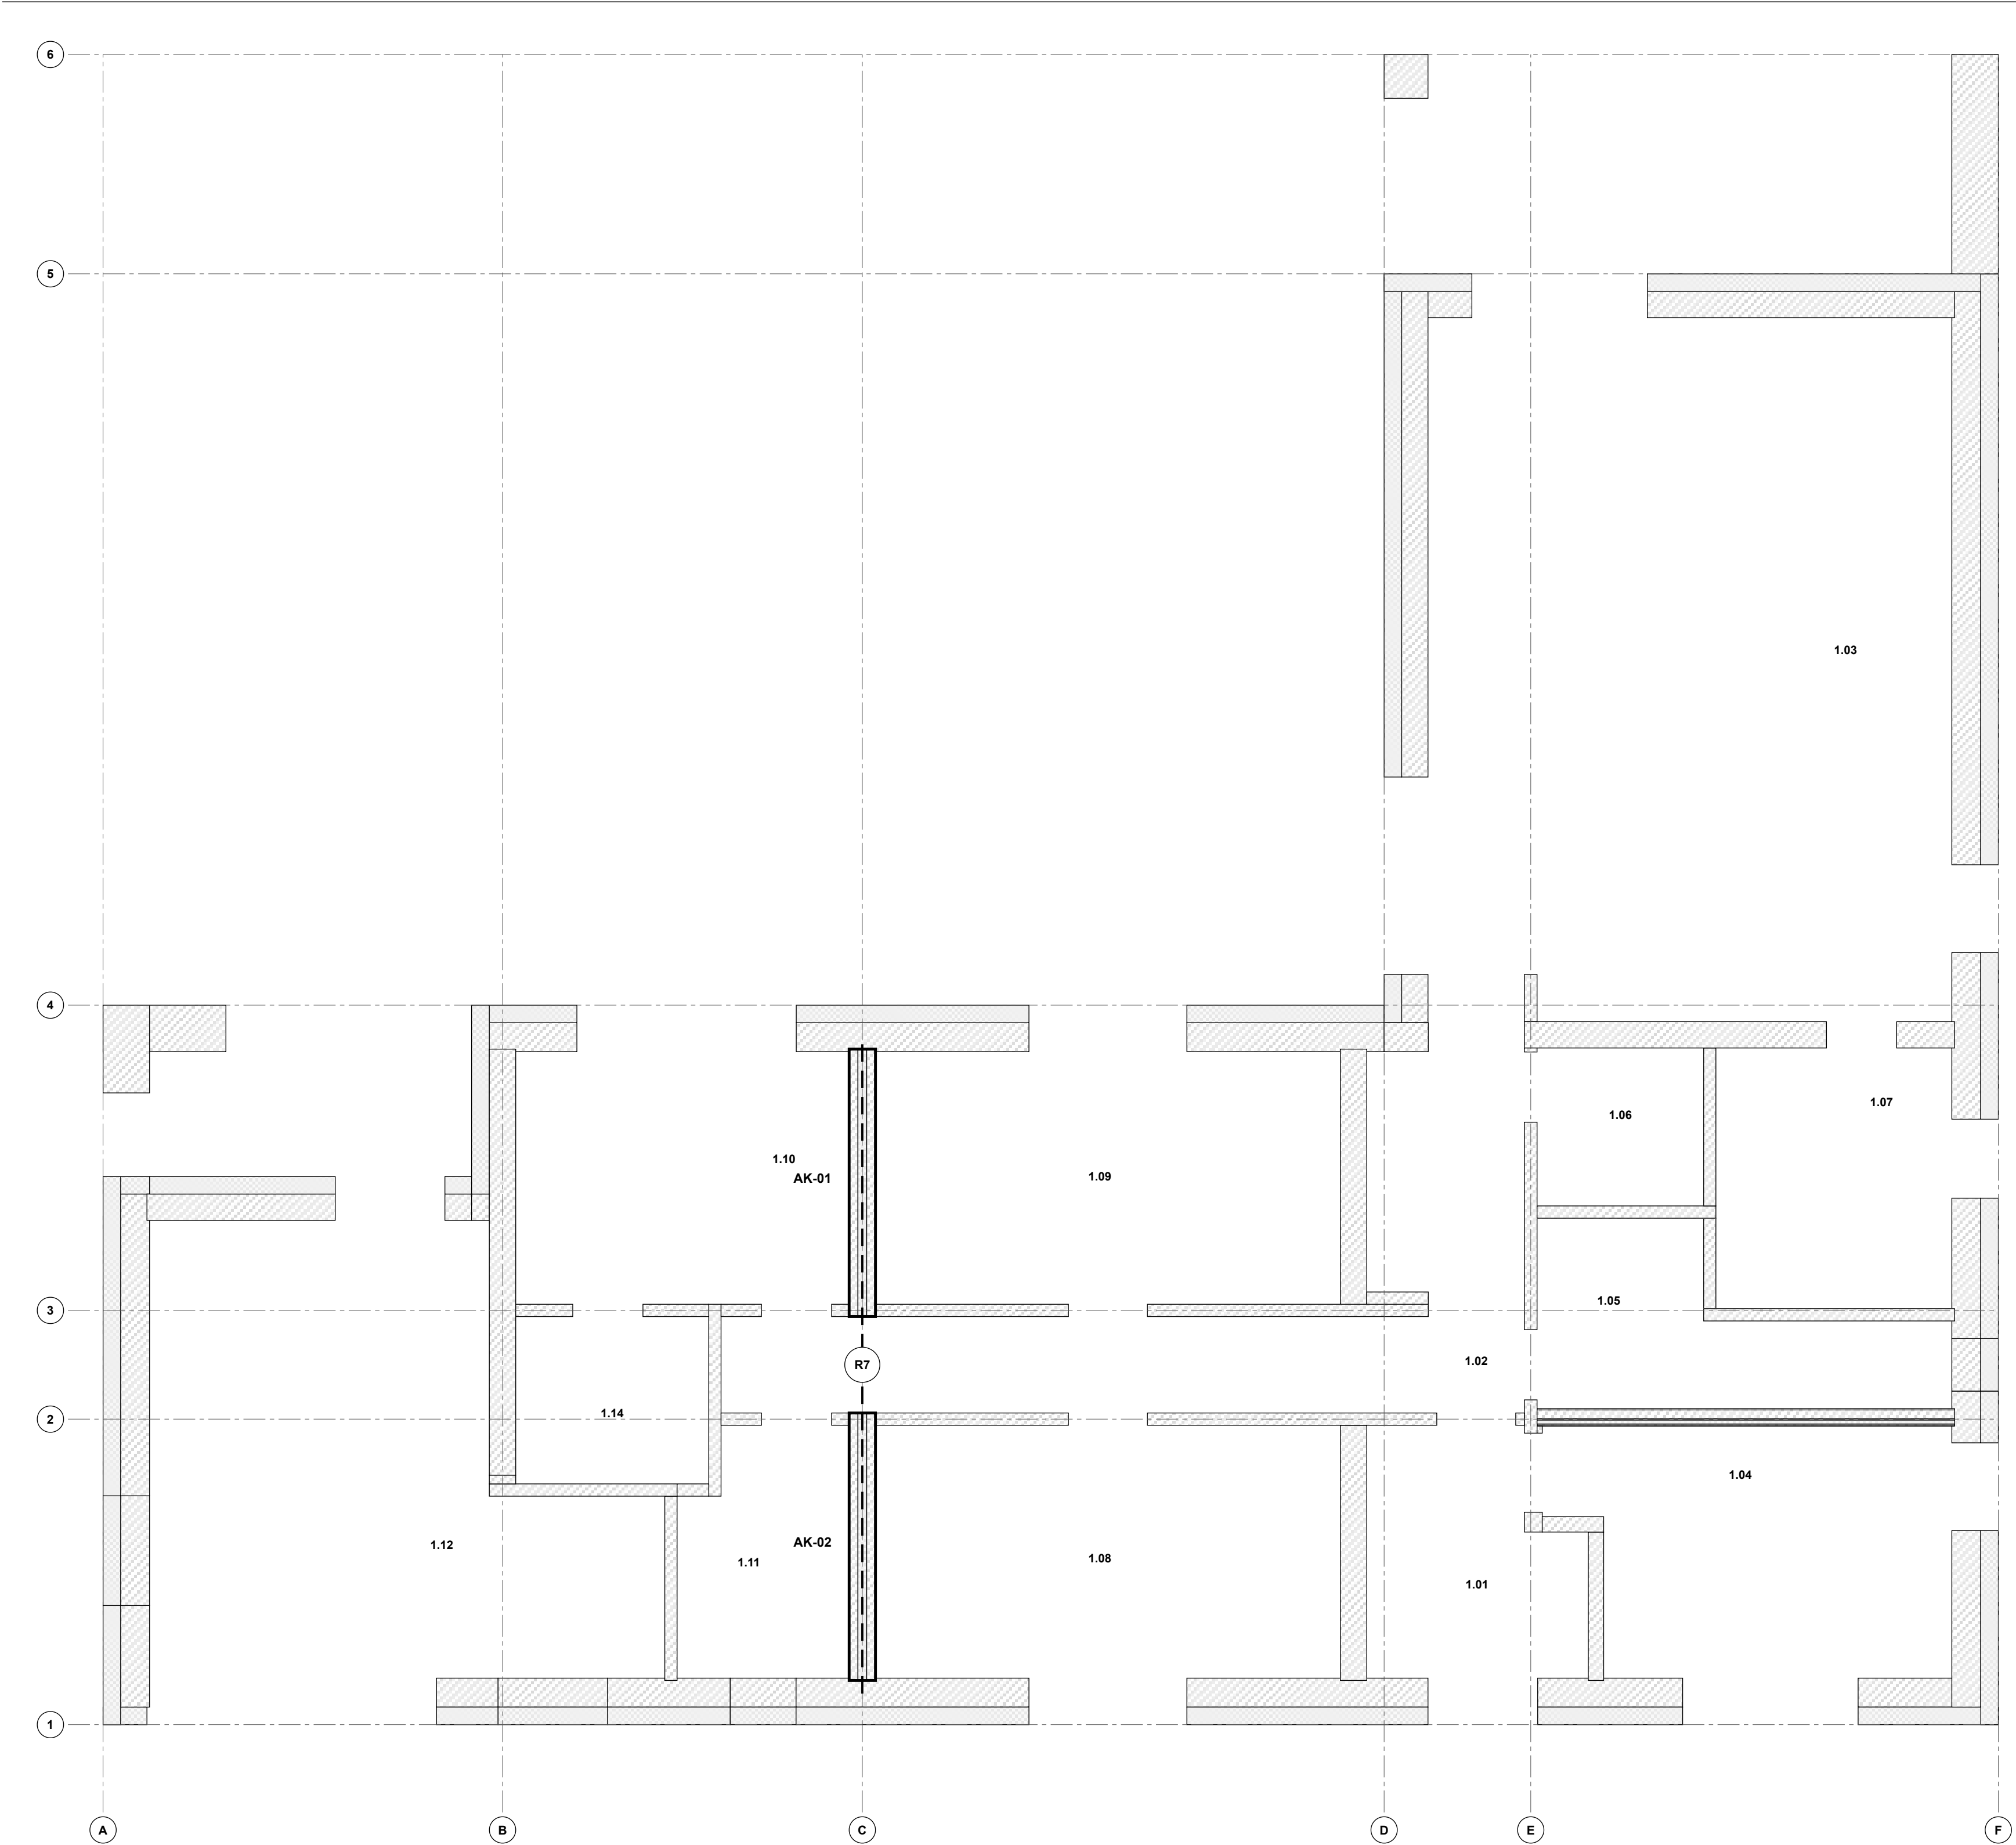

KONTROLA TLAČE 100 % - 1 000 mm = 20 mm na papieri
1 : 50 - vypnúť „prispôbiť strane“

NOVOSTAVBA RD BŘEZÍ U MIKULOVA

PARCELA 6012/26 · HLAVNÝ NÁVRH C / B / B

Základy · nosné línie a ťažké priečky

R0 = 184,200 m · M0 = PODLAHA MODELU · ΔFFL = M0 – R0 ZATIAĽ NEURČENÉ

NEHOTOVÝ LIST. Výpočet hmotností SA30 z deklarovaných údajov a geometrie nie je posúdením únosností. Základy, existujúca doska, podlažie a konečné zariadenia vyžadujú nový statický návrh.

STAV

NEVYDANÉ NA REALIZÁCIU

Chýbajúci návrh sa nesmie nahradiť mierkou výkresu.

VYPRACOVAL: digitálne dvojča · bez autorizačnej pečiatky

DÁTUM 2026-09-14 FORMÁT A1 841 × 594 mm MIERKA 1 : 50

ZDROJ 6cd4bc82841b · úplné odtlačky v model-snapshot.json

Línia	Súradnica [mm]	Význam
A	6 440	X / pôvodná os
B	10 993	X / pôvodná os
C	15 093	X / pôvodná os
D	21 040	X / pôvodná os
E	22 711	X / pôvodná os
F	28 040	X / pôvodná os
1	3 000	Y / pôvodná os
2	6 482	Y / pôvodná os
3	7 721	Y / pôvodná os
4	11 200	Y / pôvodná os
5	19 535	Y / pôvodná os
6	22 035	Y / pôvodná os

SA30 · VLASTNÁ HMOTNOSŤ ZAŤAŽUJÚCA DOSKU

Stena	L [mm]	H [mm]	kg/m	kg spolu
AK-01	3 048	3 125	456,25	1 390,65
AK-02	3 048	3 125	456,25	1 390,65

Oba plášte: 2 × 73 kg/m² muriva bez omlietky. Spolu 2 781,3 kg. Vata, povrchy, obklady, základacia vrstva a vybavenie navyše; úplné návrhové zaťaženie neurčené.

Zdroj: LeierPLAN 10 N+F, Devecser · technický list Leier 07/2025

R7: kandidátna os X 15 093; Y 3 354–10 849. Dva zaťažené úseky po 3 048 mm, voľná chodba 1 099 mm. Osi tehlových plášťov sú ±100 mm od R7. Pripadný spojitý pás prechádza iba pod podlahou.

SA30 ostáva nenosná pre strechu a strop. Návrh musí overiť prenos jej hmotnosti cez existujúcu dosku, uloženie pásu a podlažie. R7 nemá určený prierez ani výstuž a nie je pokynom na zásah do vyliatej dosky.


Horný monolit 350 × 600 mm a doska 150–200 mm sú požiadavky stavebníka, nie výsledok výpočtu. Rozmery a väzby: ZA-02; priestorový pohľad: ZA-03.

Monolitické založenie · rozmery a väzby

MONOLIT DO ODNÍMATEĽNÉHO DEBNENIA · ZADANIE STAVEBNÍKA


Horný pás 350 × 600 mm je daný rozmer. Podľa doplnenia stavebníka je doska vylíata aj s lodžiou a krytou terasou. Lica, výšky a výstuž treba zamerať; nepoužíva sa stratené debnenie.

Z1 · HORNÝ OBVODOVÝ MONOLIT · 1 : 10

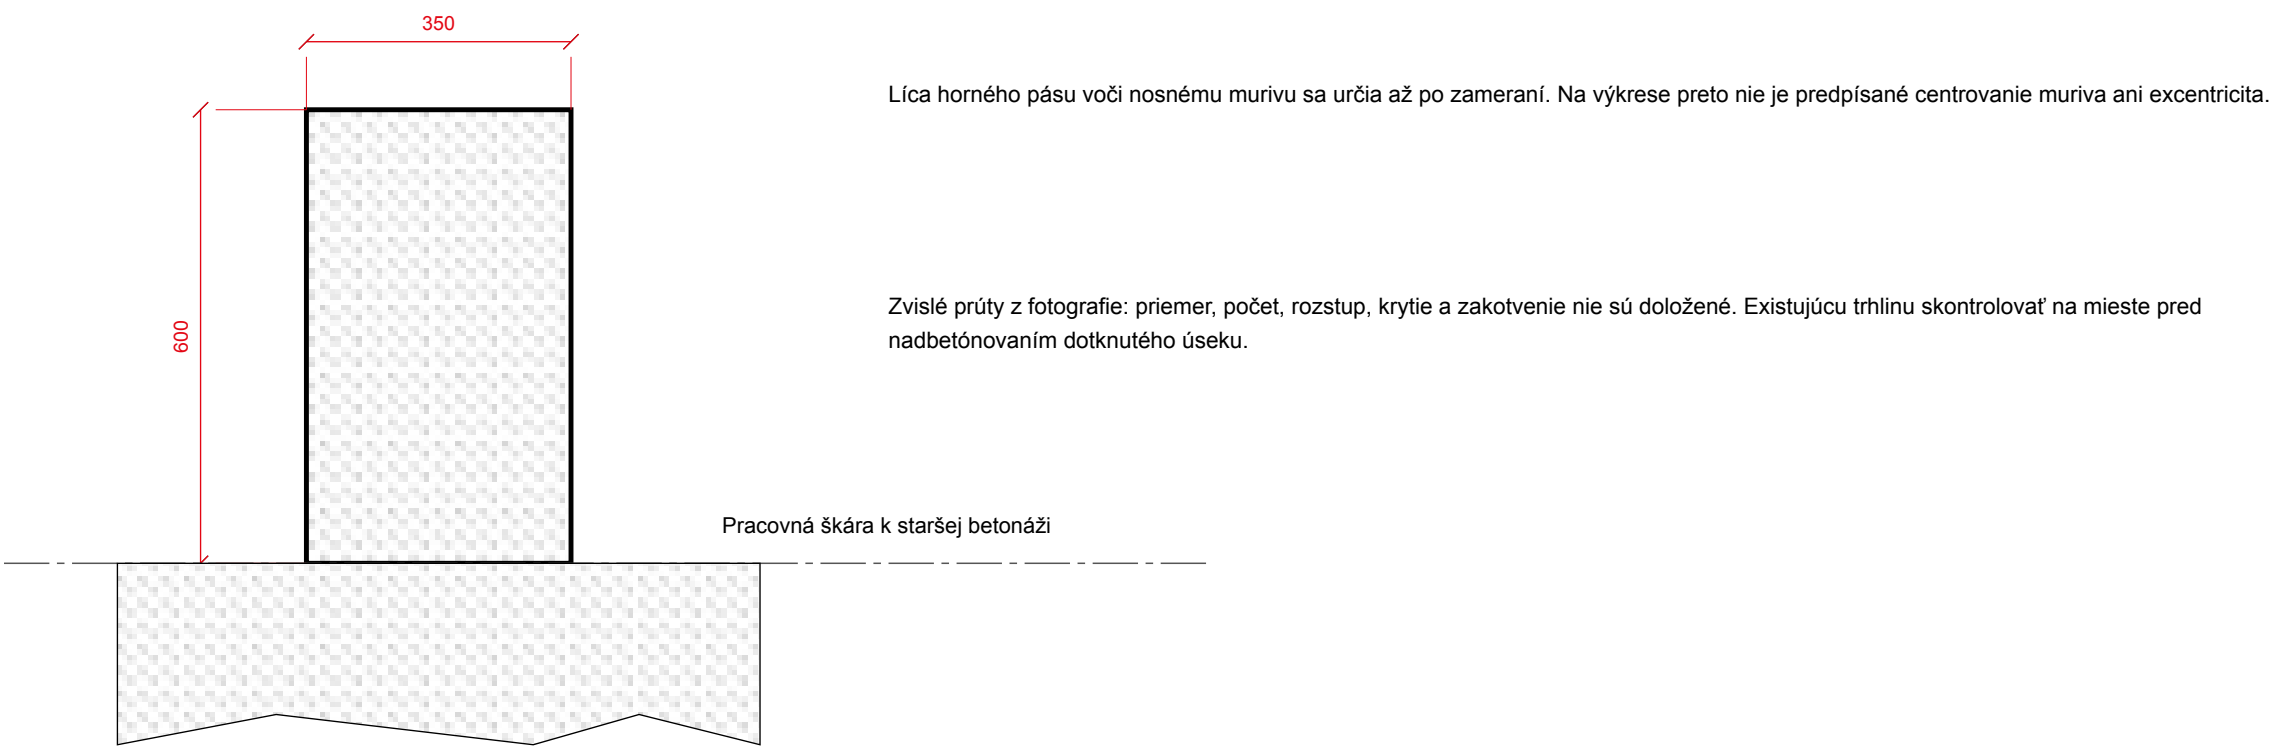

Spodný pás: 600 mm v zemi podľa stavebníka.
Šírka, spodok a horné líce voči R0 zatiaľ nezamerané.
Prerušený obrys spodného pásu neurčuje jeho šírku ani výšku.

D1 · NOSNÁ DOSKA A INŠTALÁCIE · 1 : 10

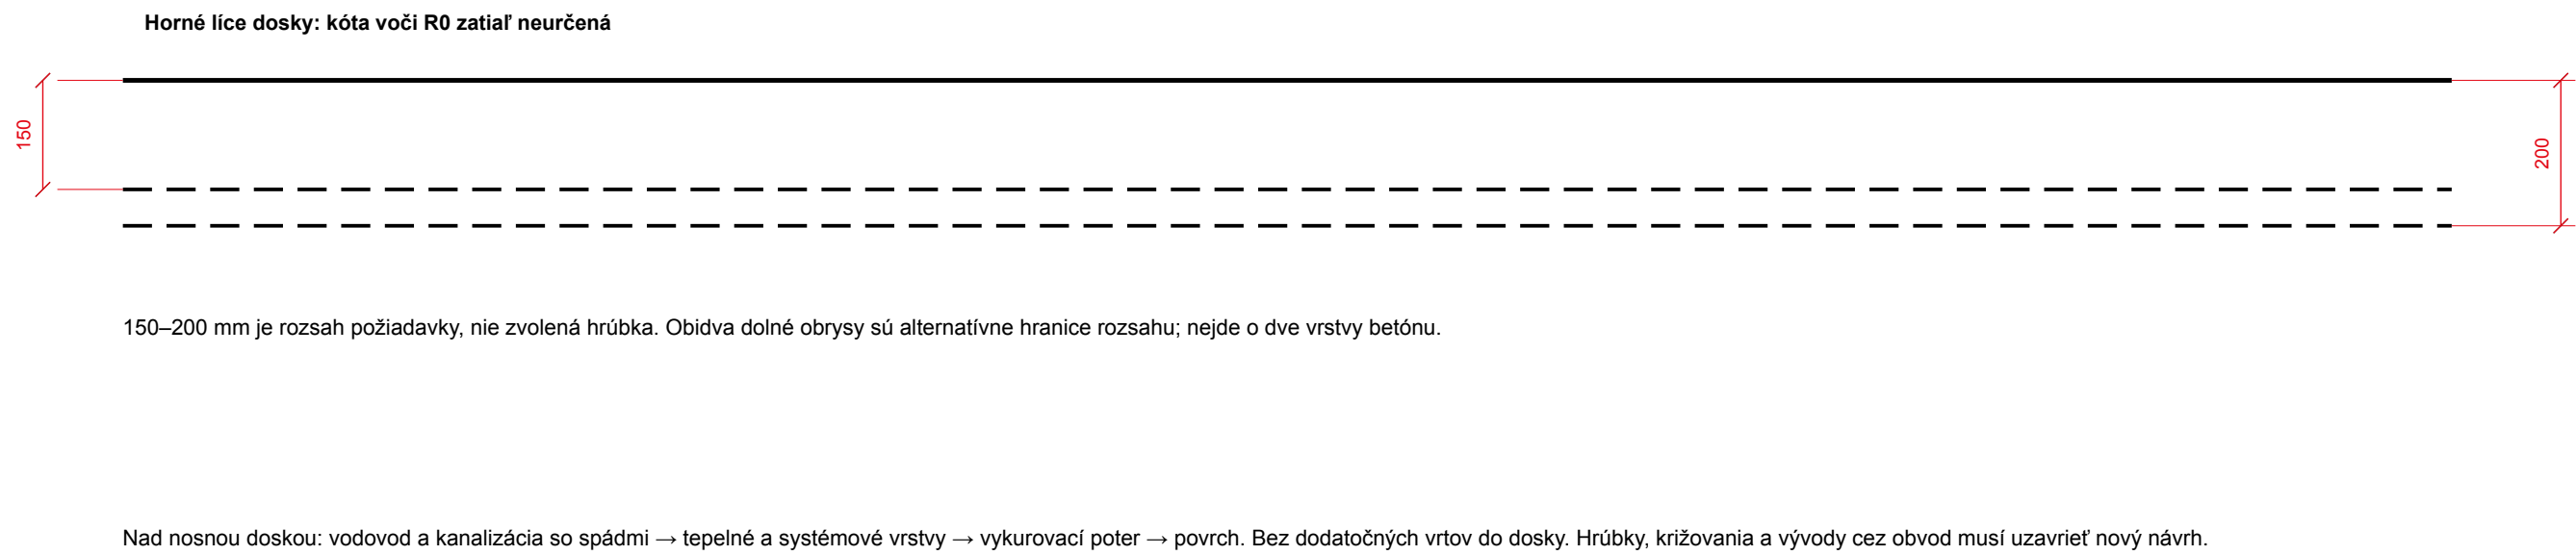

VNÚTORNÉ REBRÁ A ZÁKLADOVÁ PÔDA

Prvok / rozhodnutie	Záväzné zadanie / nadväznosť	Čo ešte určuje návrh
R1–R7 · vnútorné trasy	Monolitické, v horných 600 mm podľa stavebníka. Musia mať konkrétnu cestu prenosu zaťaženia do únosného podkladu alebo podpor.	Polohy, šírk, uloženie, výstuž a spoje podľa reakcií stien, stropu a krovu.
Zásyp pod doskou	Stavebník požaduje zhrnutú zeminu. Vhodnosť existujúcej zeminy, vlhkosť, hutnenie po vrstvách a výsledná únosnosť nie sú overené.	Geotechnické posúdenie a merateľné podmienky prevzatia podkladu.
Betón C16/20	Požadovaný pre pokračovanie; fotografie ani názov triedy nepotvrdzujú dodanú zmes alebo vhodnosť pre všetky prvky.	Doklad o dodávke, expozičné triedy, krytie a statická únosnosť. Sokel posúdiť samostatne.
Škály a monolit	Spodný pás už bol betonovaný. Nová horná časť bude mať pracovnú škálu; monolitický systém neznamená betónáž bez škály.	Priprava a posúdenie styku, prenos šmyku, zakotvenie a postup betónáže.
Ťažké priečky SA30	AK-01/02 zaťažujú dosku aj ako nenosné priečky. Ich vlastná hmotnosť je vyčíslená na ZA-01; kandidátka trasa R7 na ZA-03.	Posúdiť existujúcu dosku a podopretie oboch plášťov. SA30 ani H200 neslúžia ako potvrdené podpory strechy alebo stropu.

VÝŠKA PODLAHY SA NAVRHNE Z NADVÄZUJÚCICH ÚROVNÍ

Všetko v mm: ΔFFL = zE + 600 + j + p

zE = zameraný vrch existujúceho spodného pásu nad R0; j = vrch dosky mínus vrch nového pásu; p = úplná podlahová skladba nad doskou.

Možný styk dosky s pásom	Výšková väzba; styk a únosnosť musí určiť návrh
Horné líca dosky a nového pásu zarovnané	j = 0; hrúbka dosky sa k vrchu pásu znova nepripočíta.
Celá doska uložená nad novým pásom	j = hrúbka dosky; 150–200 mm je zatiaľ len požadovaný rozsah.

KONTROLA TLAČE 100 % - 200 mm = 20 mm na papieri

1 : 10 - vypnúť „prispôbiť strane“

NOVOSTAVBA RD BŘEZÍ U MIKULOVA

PARCELA 6012/26 · HLAVNÝ NÁVRH C / B / B

Monolitické založenie · rozmery a väzby

R0 = 184,200 m · M0 = PODLAHA MODELU · ΔFFL = M0 – R0 ZATIAĽ NEURČENÉ

Rozmery 350/600/150–200 mm pochádzajú zo zadania stavebníka. Zameranie a statické overenie chýbajú. Nejde o výkres výstuže ani pokyn na pokračovanie betónáže.

STAV

NEVYDANÉ NA REALIZÁCIU

Chýbajúci návrh sa nesmie nahradiť mierkou výkresu.


VYPRACOVAL: digitálne dvojča · bez autorizačnej pečiatky

DÁTUM 2026-09-14 FORMÁT A1 841 × 594 mm MIERKA 1 : 10

ZDROJ 6cd4bc82841b · úplné odtlačky v model-snapshot.json

Základy domu v priestore

Celý obrys vrátane lodžie a krytej terasy · ulica dole, garáž vľavo

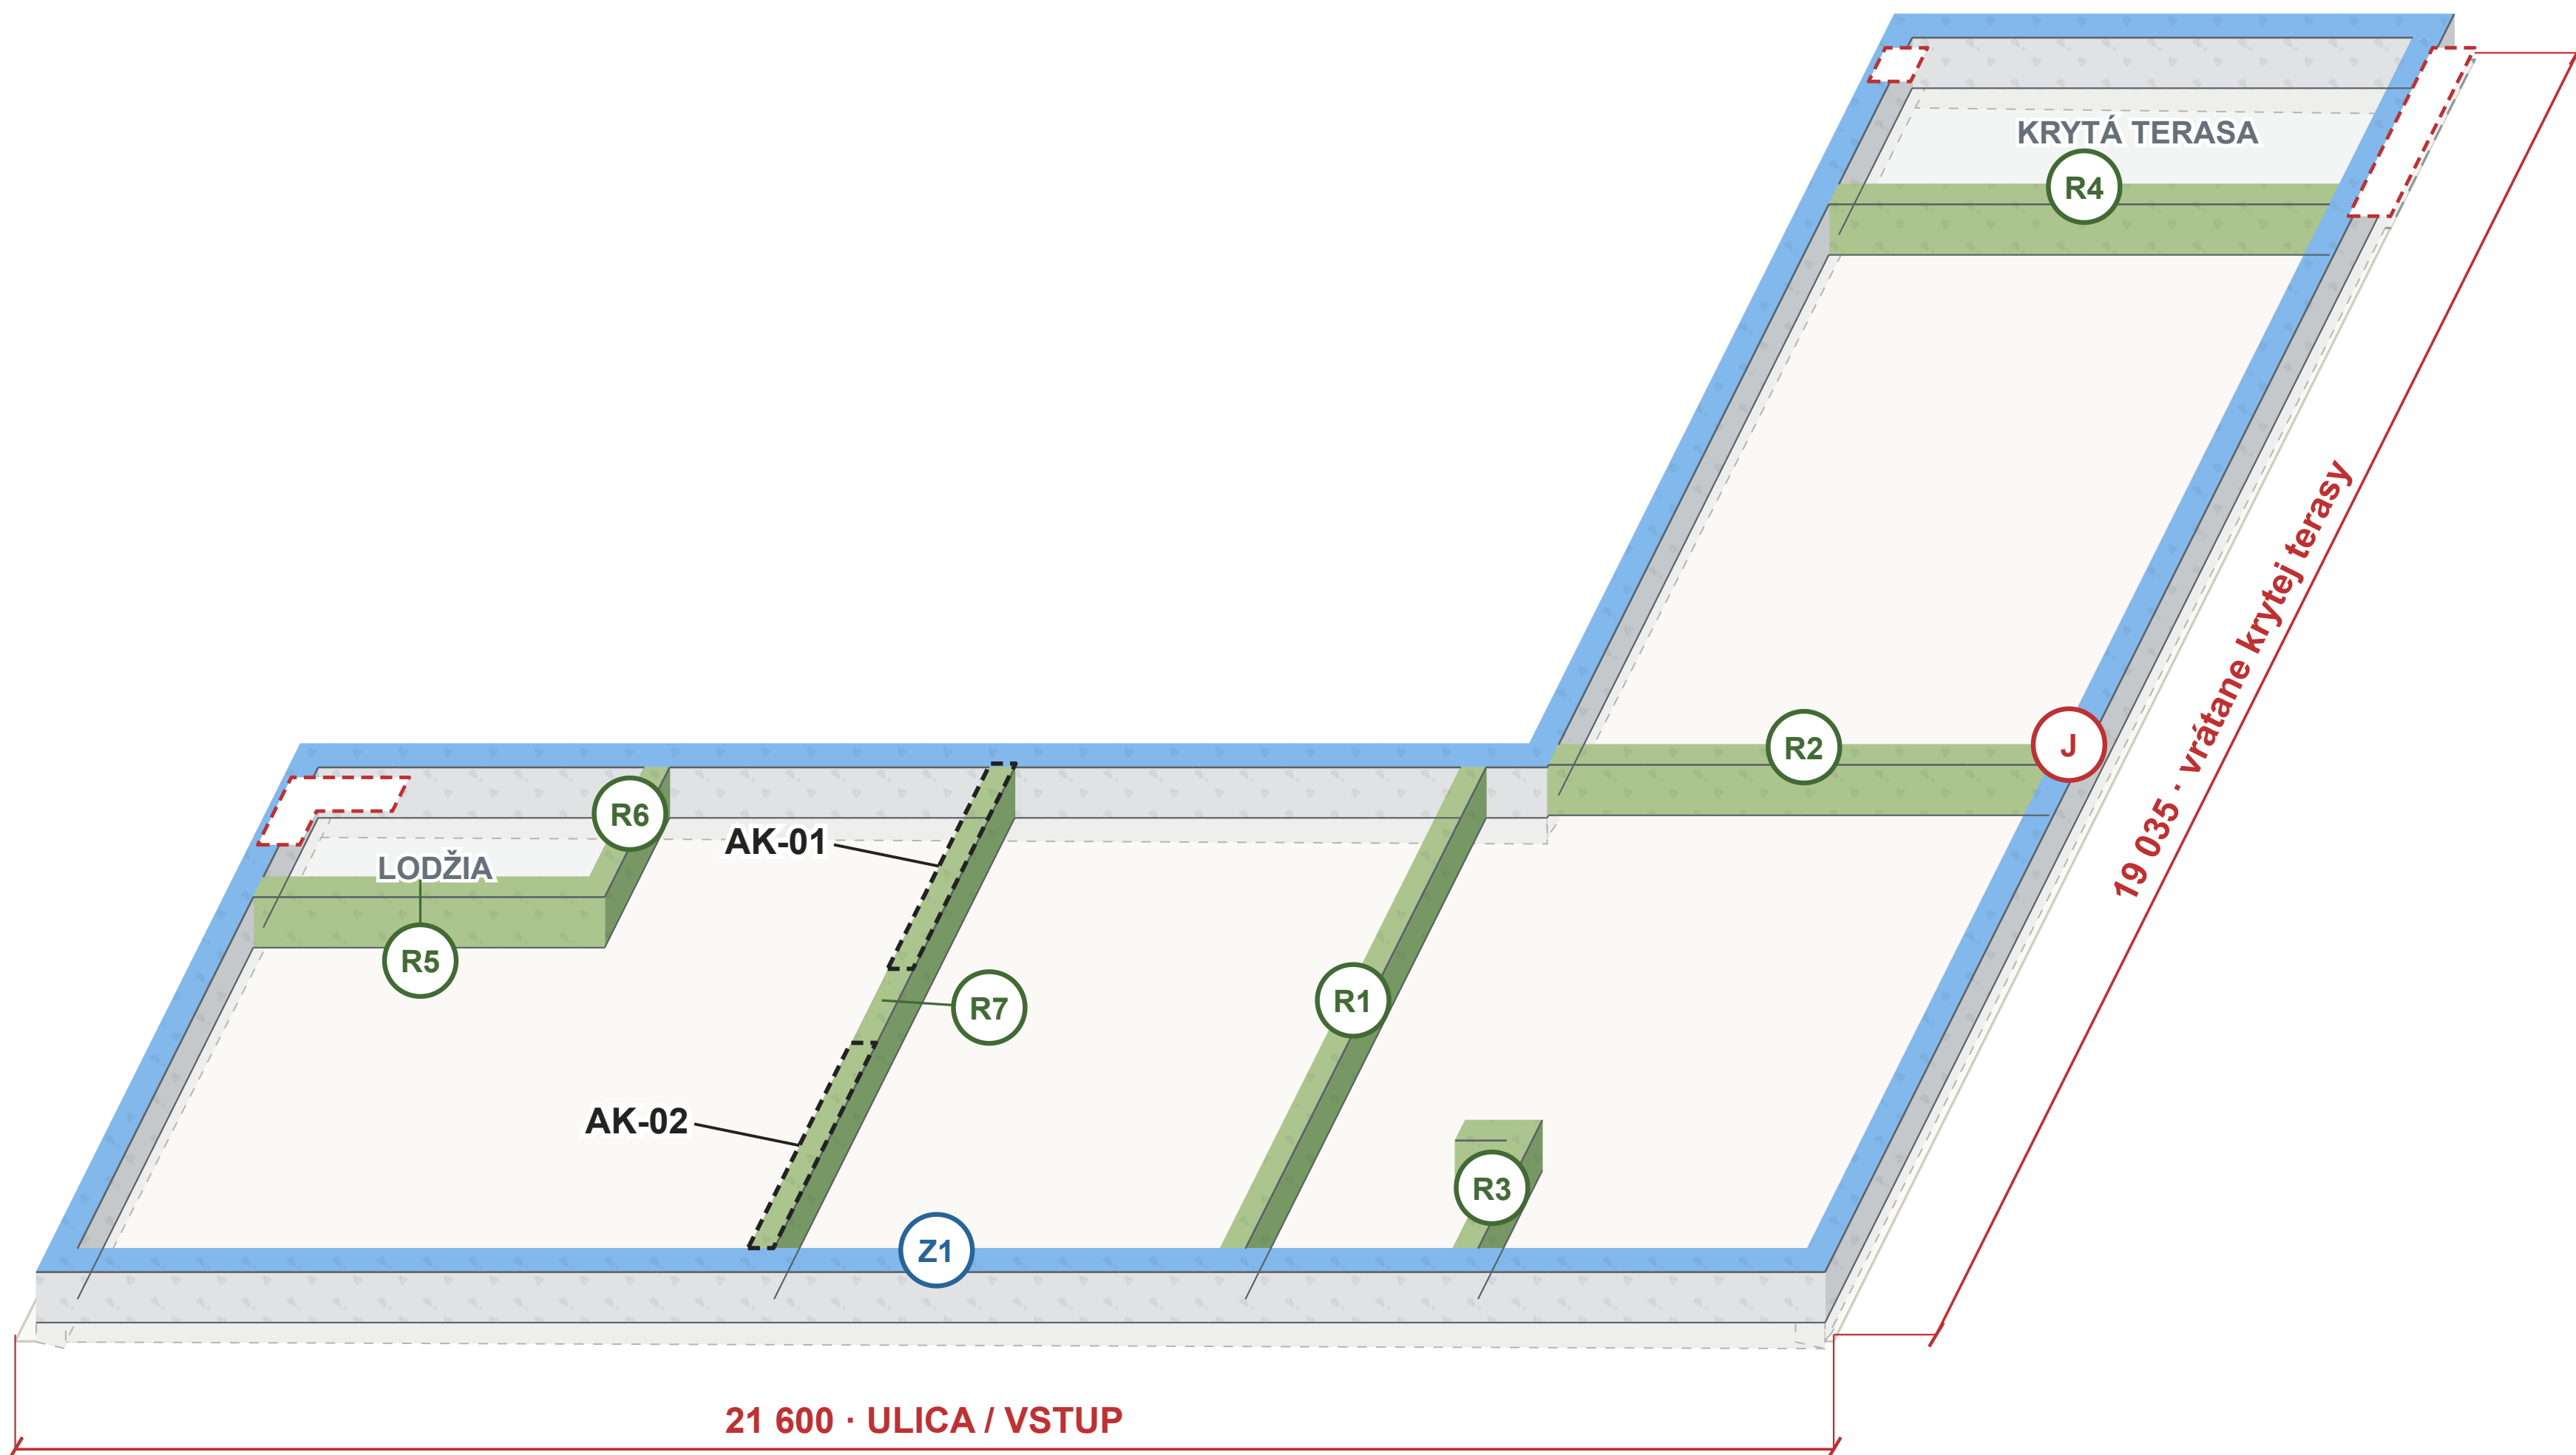

R7 · PODOPRETIE VLASTNEJ HMOTNOSTI SA30 NA VÝPOČET

AK-01 + AK-02: 456,25 kg/m muriva bez omietky, spolu 2 781,3 kg. Povrchy a ďalšie vrstvy navyše. Čiarkovane sú označené iba zaťažené úseky; chodba ostáva voľná.


Doska vrátane terás je podľa stavebníka vyliata; tu je odkrytá. R7 je návrh na posúdenie existujúcej dosky, nie pokyn na jej rezanie alebo betónáž.

NÁVRH NA KOORDINÁCIU · NEVYDANÉ NA REALIZÁCIU

ČO V OBRÁZKU VIDIŠ

- Z1** **Obvod vrátane oboch terás**
350 × 600 mm podľa zadania. Líca a skutočné rozmery treba zamerať.
- R** **R1 až R7 · návrhové trasy**
R1–R6 podľa stien a terás. R7 pod vlastnou hmotnosťou SA30. Výška 600 mm; šírka, uloženie a výstuž na výpočet.
- J** **Napojenie rebra na obvod**
Označené miesto na návrh spojenia. Obrázok nepredpisuje priemery, počty ani kotvenie prútov.

J · PRINCÍP NAPOJENIA

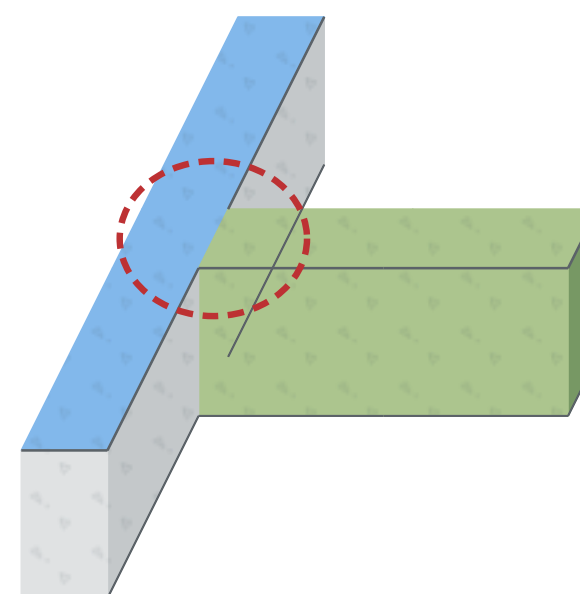

Zväčšený princíp bez mierky. Šírka rebra je grafická. Čiarkované obrysy na terasách označujú nadzemné podpery.

Spodný pás: podľa stavebníka 600 mm v zemi. Jeho náznak je prerušovaný; šírka a kóty výkopu zostávajú neurčené.

Axonometria bez odmeriavania · súradnice z modelu C/B/B

KONTROLA TLAČE 100 % · úsečka 20 mm na papieri

Axonometria bez mierky; z obrázka neodmeriavať rozmery.

NOVOSTAVBA RD BŘEZÍ U MIKULOVA

PARCELA 6012/26 · HLAVNÝ NÁVRH C / B / B

Základy · priestorový pohľad na pásy a rebrá

R0 = 184,200 m · M0 = PODLAHA MODELU · ΔFFL = M0 – R0 ZATIAĽ NEURČENÉ

Celý L-obrys vrátane lodžie a krytej terasy. R7 dopĺňa kandidátny pás pod vlastnou hmotnosťou SA30; priečky zostávajú nenosné pre strechu a strop. R1–R7 nemajú potvrdené prierezy, uloženie ani výstuž. Podklad a zdroj hmotnosti: ZA-01.

STAV

NEVYDANÉ NA REALIZÁCIU


Chýbajúci návrh sa nesmie nahradiť mierkou výkresu.

VYPRACOVAL: digitálne dvojča · bez autorizačnej pečiatky

DÁTUM 2026-09-14 FORMÁT A1 841 × 594 mm MIERKA axonometria

ZDROJ 6cd4bc82841b · úplné odlišky v model-snapshot.json

Pôdorys strechy

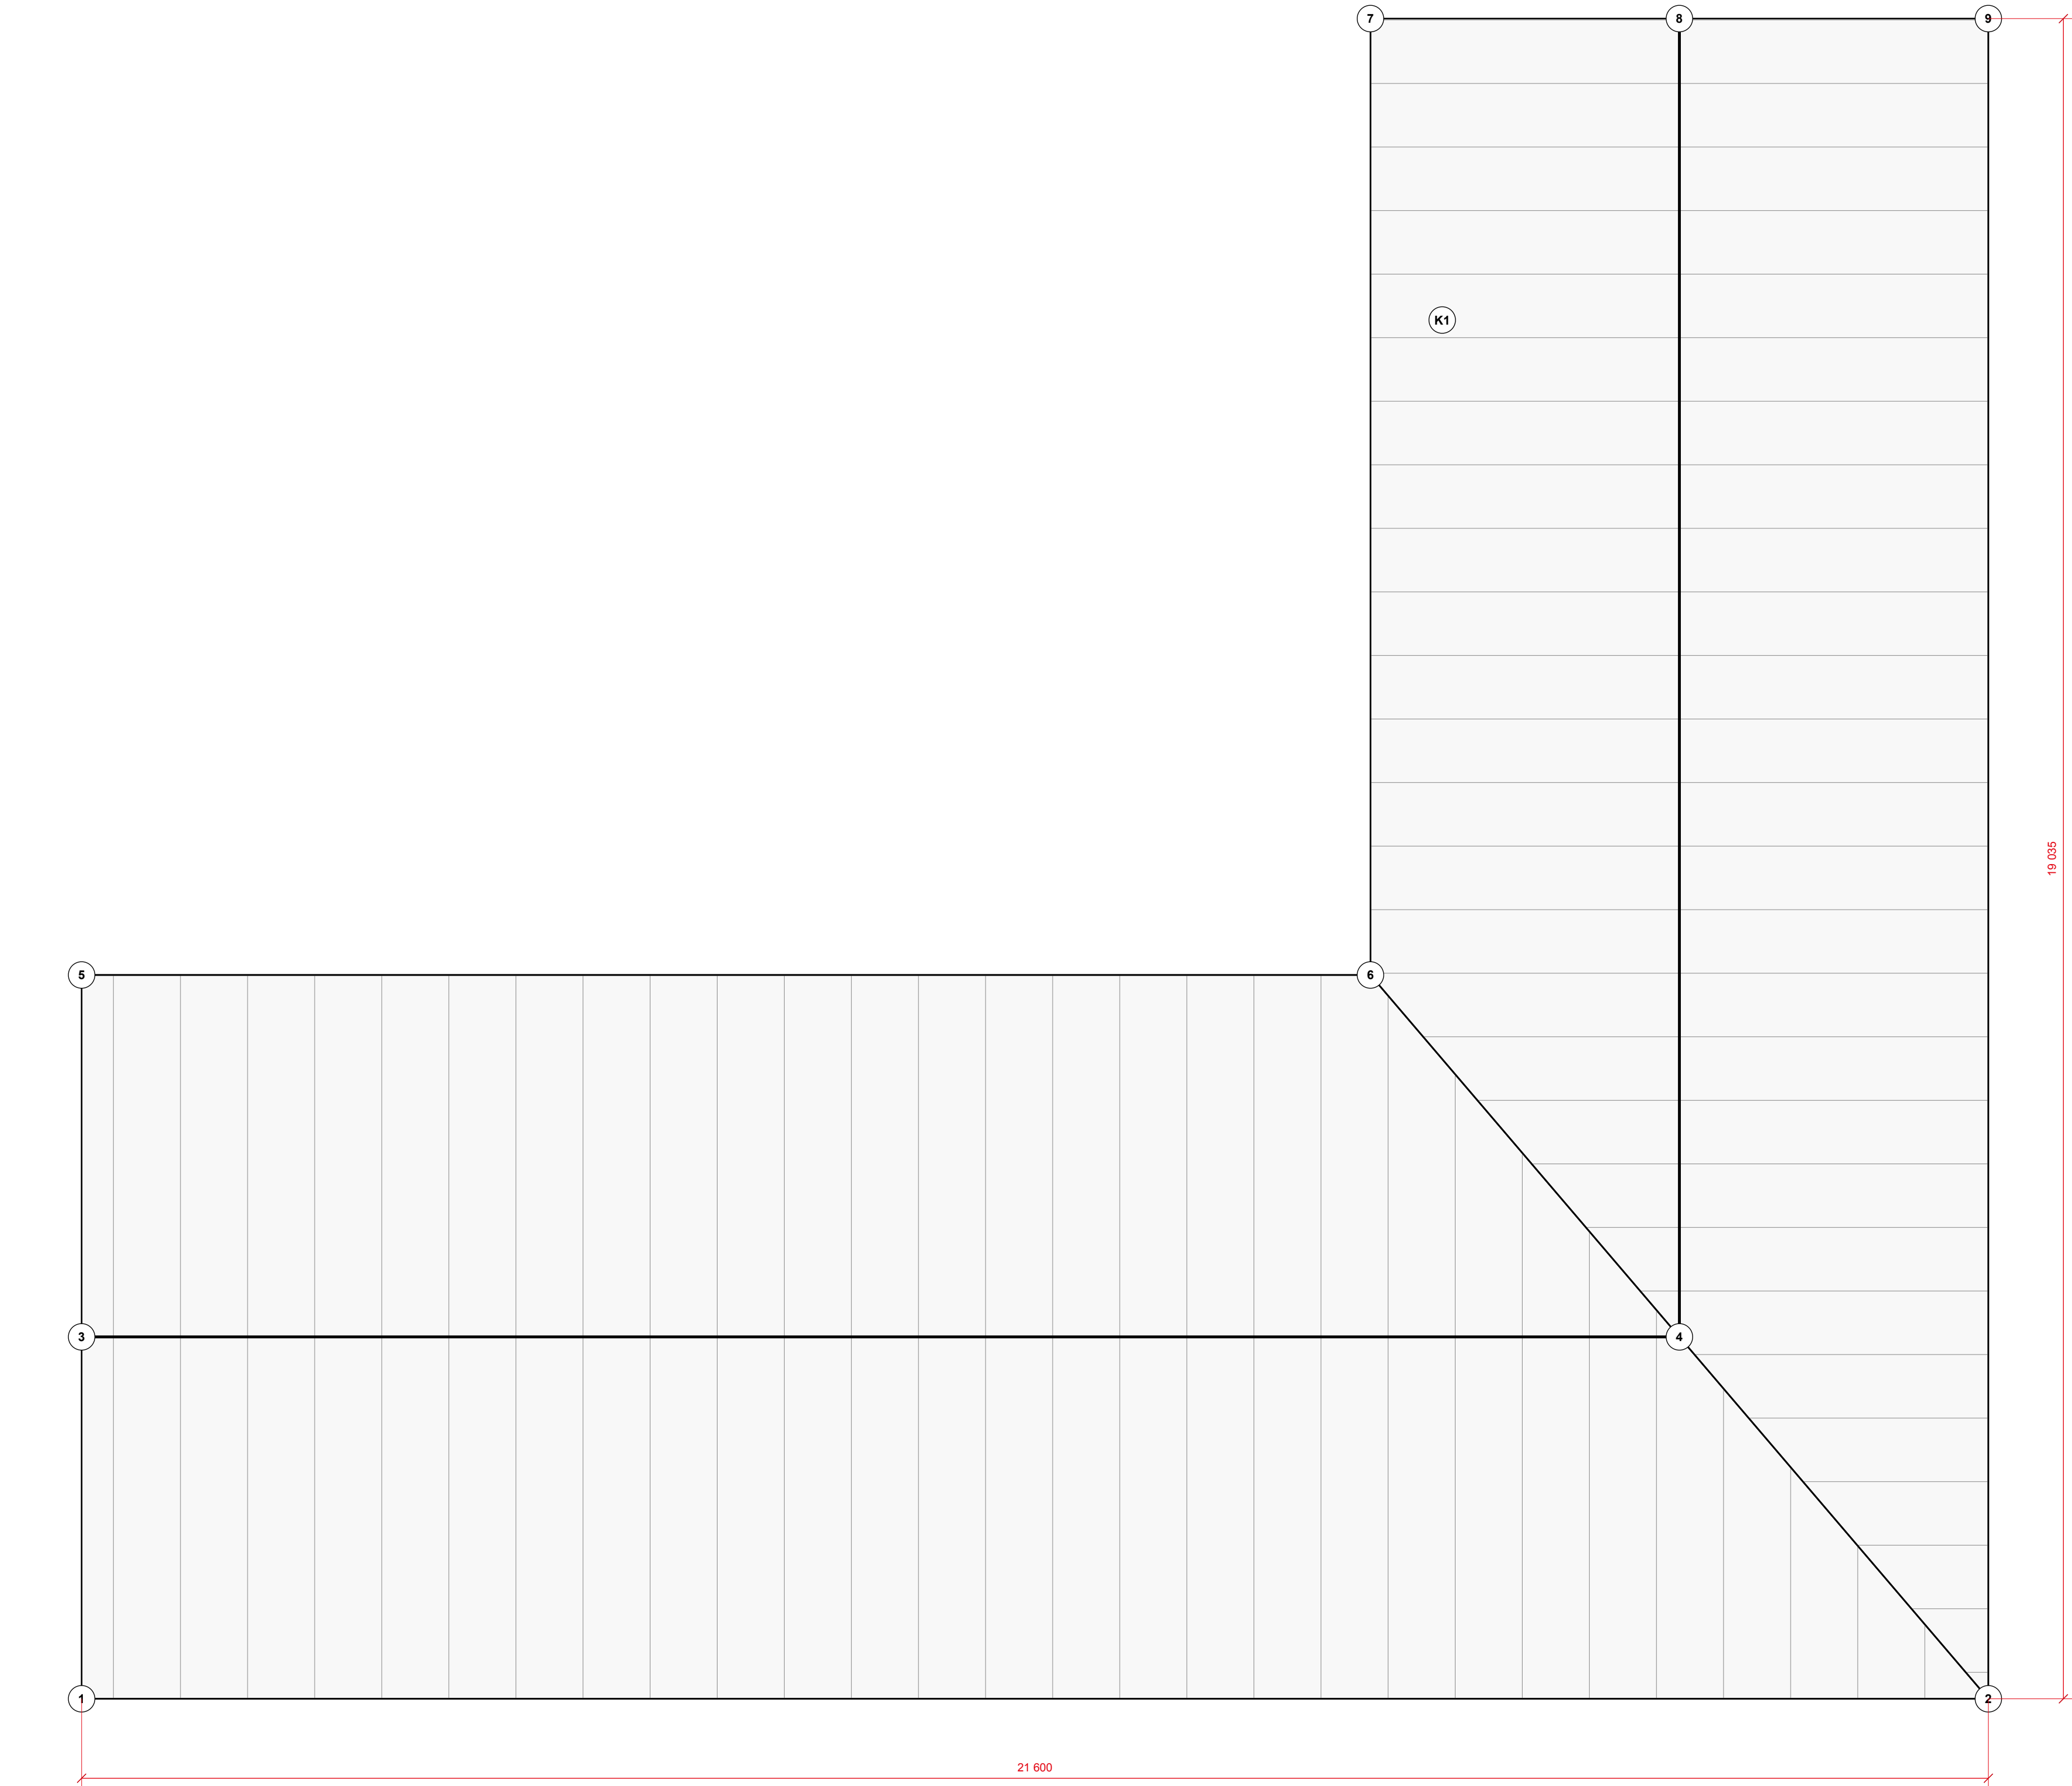

Bod	X [mm]	Y [mm]	Z [mm]	Ref.
1	6 440	3 000	3 125	ST
2	28 040	3 000	3 125	ST
3	6 440	7 100	5 560	ST
4	24 540	7 100	5 560	ST
5	6 440	11 200	3 125	ST
6	21 040	11 200	3 125	ST
7	21 040	22 035	3 125	ST
8	24 540	22 035	5 560	ST
9	28 040	22 035	3 125	ST

GEOMETRIA STRECHY Z MODELOVÝCH VRCHOLOV

Hlavný trakt: atan((5560 - 3125) / 4100) = 30.706180°. Kridlo: 34.826887°. Pôvodné štítky 30°/34° nie sú presným sklonom tejto geometrie. Obal sa nemení.

K1: FLUE-LIVING-103-B; X 21 853, Y 18 620, Ø 150 mm, ukončenie M+6,160. Kotoľňa B zatiaľ nemá modelovanú vonkajšiu trasu dymovodu.

Falcové línie zobrazujú existujúci modelový raster krytiny. Nie sú rozmiestnením krokiev. Úžľabie, nárožie, hrebeň a odkvapné hrany sú z tej istej geometrie ako 3D.

Nové zadanie: falcovaný plech, nulový architektonický presah. Krytá terasa je zapustená hmota, nie presah. Koncová rovina strechy sa viaže na lice čela terasy; lemovanie a žľab potrebujú finálny detail.

Poväť iba na odkladanie vecí. Drevené pôdne väzníky v pravidelnom trakte, samostatné drevené polia pri uzle L a osobitná katedrála. Bez betónového stropu a nadbetonávky. Prierezy, skladovacie zaťaženie, spoje a kotvenie vyžadujú výpočet.

KONTROLA TLAČE 100 % - 1 000 mm ≈ 20 mm na papieri

1 : 50 - vypnúť „prispôbiť strane“

NOVOSTAVBA RD BŘEZÍ U MIKULOVA

PARCELA 6012/26 · HLAVNÝ NÁVRH C / B / B

Pôdorys strechy

R0 = 184,200 m · M0 = PODLAHA MODELU · ΔFFL = M0 – R0 ZATIAĽ NEURČENÉ

Geometrické vrcholy, hrany a presahy z lib/twin-roof.ts. Návrh krovu a strešného plášťa je samostatná otvorená časť R04. Čísla bodov sú doplnkové, existujúce osi zostávajú.

STAV

NEVYDANÉ NA REALIZÁCIU

Chýbajúci návrh sa nesmie nahradiť mierkou výkresu.


VYPRACOVAL: digitálne dvojča · bez autorizačnej pečiatky

DÁTUM 2026-09-14 FORMÁT A1 841 × 594 mm MIERKA 1 : 50

ZDROJ 6cd4bc82841b · úplné odtlačky v model-snapshot.json

Situácia osadenia · ulica

ULIČNÁ ČASŤ · nadväzuje SI-02 · prekrytie Y 17 500–21 000 mm

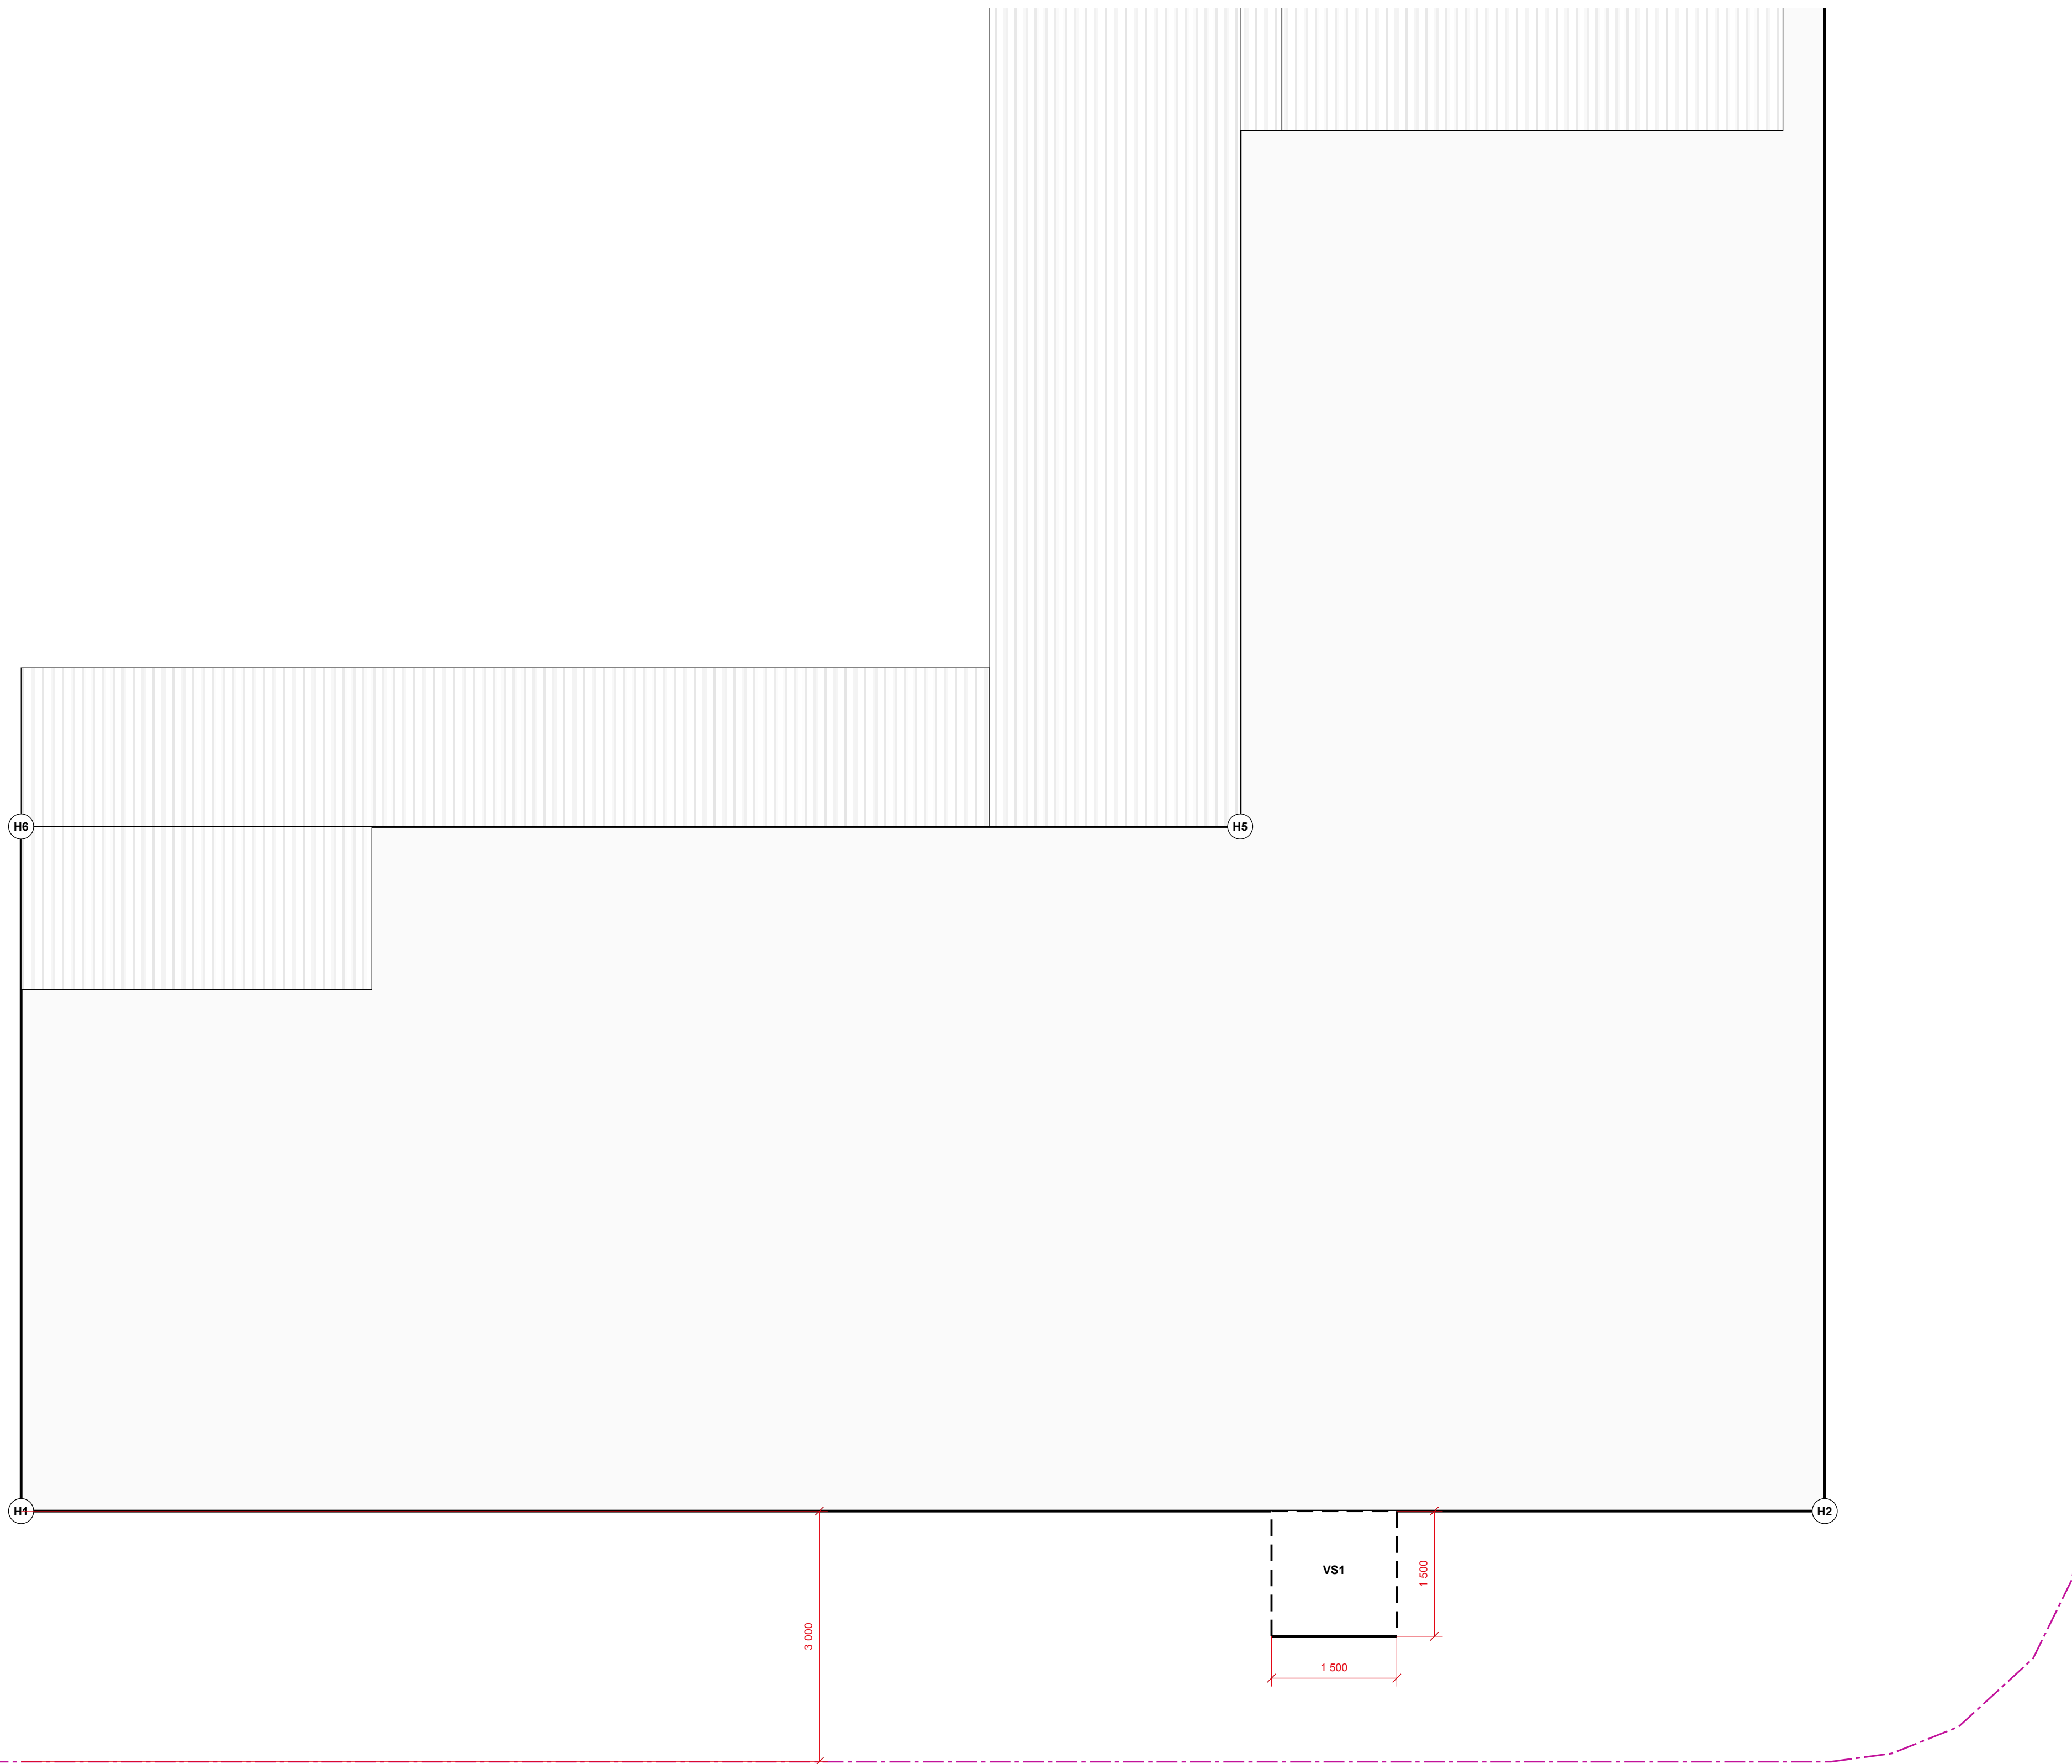

PARCELA 6012/26. Uličný aj pravý KOLMÝ odstup 3 000 mm. Jediný súradnicový rámec C/B/B.

Katastrálna hranica a požadované osadenie nie sú geodetické vytyčenie. Pred stavbou overiť hranice a výškopis.

VS1 · NÁVRH VSTUPU

Pri D2: podesta 1 500 × 1 500 mm v existujúcom prístupe. Čelo Y 1 500; dvere sa otvárajú dovnútra.

Jeden stupeň h = 150 mm je návrhový cieľ. Výšky podesty a prístupu, spád a prah sú otvorené; výšková väzba ZA-02. Nejde o zameraný ani realizačný stav.

Schod je pred podestou. Jeho výška sa meria od miestneho prístupu; neznamená podlahu 150 mm nad ulicou R0.

KONTROLA TLAČE 100 % - 1 000 mm ≈ 20 mm na papieri

1 : 50 - vypnúť „prispôbiť strane“

NOVOSTAVBA RD BŘEZÍ U MIKULOVA

PARCELA 6012/26 · HLAVNÝ NÁVRH C / B / B

Situácia osadenia · ulica

R0 = 184,200 m · M0 = PODLAHA MODELU · ΔFFL = M0 – R0 ZATIAĽ NEURČENÉ

Rozdelenie na dva nadväzujúce listy zachováva 1:50. Hranice a výškové osadenie treba geodeticky overiť. R05 zostáva otvorený.

STAV

NEVYDANÉ NA REALIZÁCIU


Chýbajúci návrh sa nesmie nahradiť mierkou výkresu.

VYPRACOVAL: digitálne dvojča · bez autorizačnej pečiatky

DÁTUM 2026-09-14 FORMÁT A1 841 × 594 mm MIERKA 1 : 50

ZDROJ 6cd4bc82841b · úplné odtlačky v model-snapshot.json

ZÁHRADNÁ ČASŤ · nadväzuje SI-01 · prekrytie Y 17 500–21 000 mm

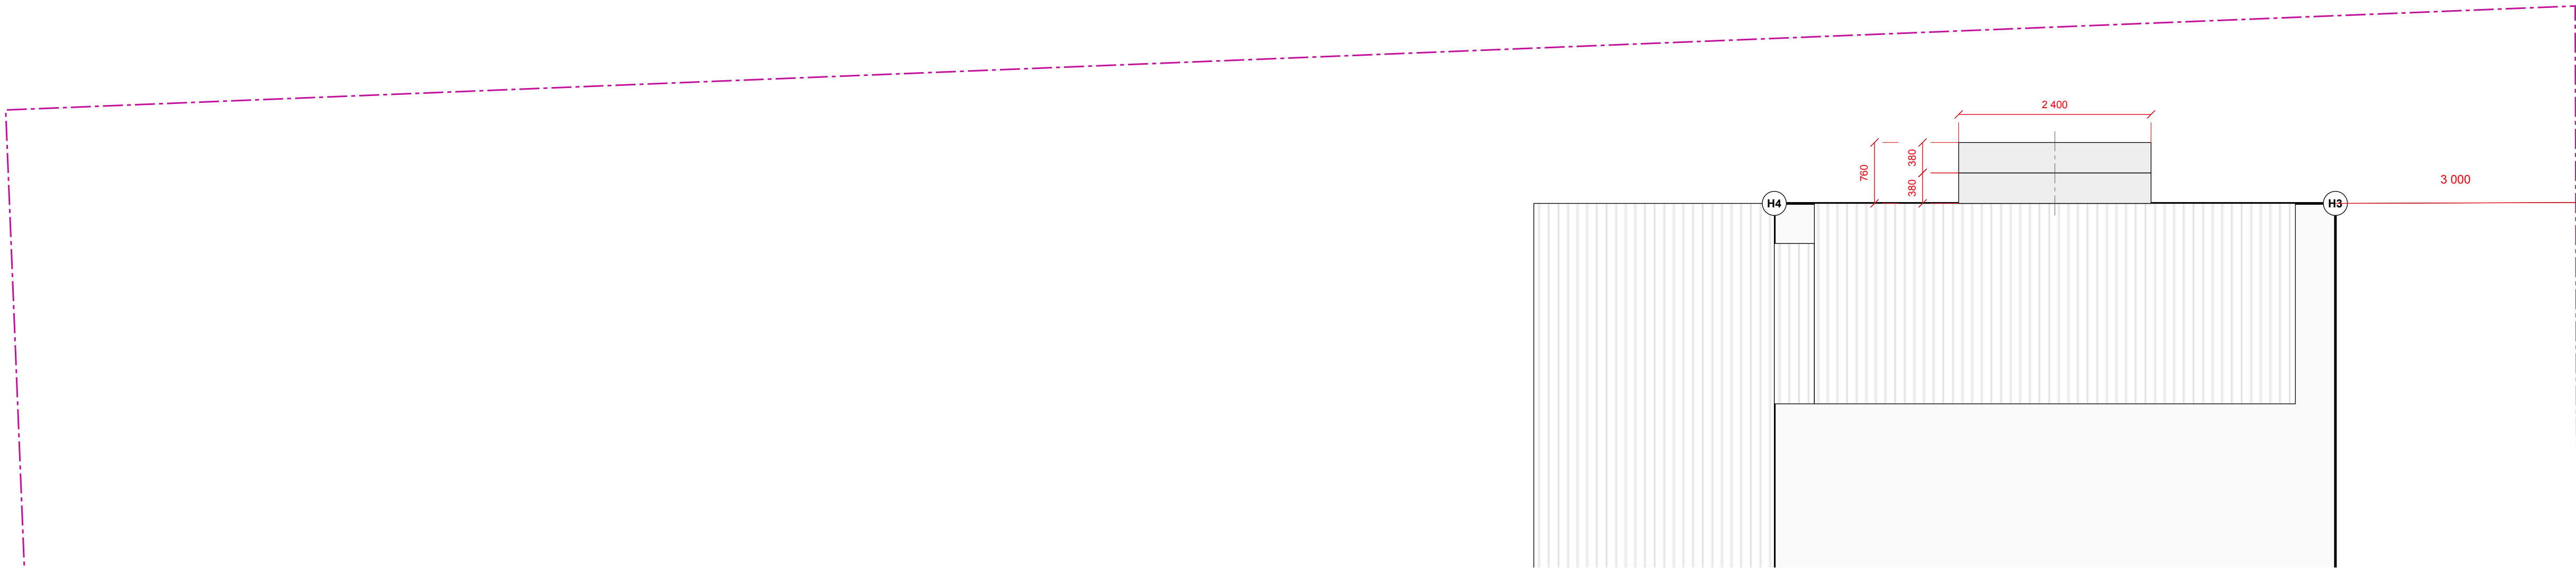

Katastrálna hranica a požadované osadenie nie sú geodetické vytýčenie.
Pred stavbou overiť hranice a výškopis.

Bod	X [mm]	Y [mm]	Prvok
H1	6 440	3 000	vonkajšnje lice
H2	28 040	3 000	vonkajšnje lice
H3	28 040	22 035	vonkajšnje lice
H4	21 040	22 035	vonkajšnje lice
H5	21 040	11 200	vonkajšnje lice
H6	6 440	11 200	vonkajšnje lice


R0 = 184,200 m: najvyšší bod ulice pri pracovni podľa stavebníka. Spodná uličná rímsa má podmienený limit 188,700 m. Presné XY bodu, Bp v a rozdiel ΔFFL podlahy k R0 treba potvrdiť; bod sa preto neumiestňuje odhadom.

Štúdia Z7/Z22: pre samostatný dom uličná čiara 3 m. Overiť 7 m medzi obytnými domami, plochy zelene, spevnenie a dve parkovacie miesta. Podrobné zdroje a otvorené kontroly: UP-01

Voda a odpad sa vedú nad nosnou doskou. Vývody a ich úrovne cez obvodovú konštrukciu musia byť určené v novom návrhu; žiadne dodatočné vŕtanie dosky

Vytyčenie stupňov: spoločná os X 24 540 mm; prvé čelo Y 22 035 mm = os 6. Krajné lica X 23 340 / 25 740 mm. Odstupy od vonkajších líc krídla: 2 300 mm / 2 300 mm.

KONTROLA TLAČE 100 % · 1 000 mm = 20 mm na papier

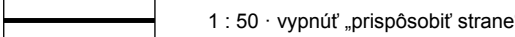**PARCELA 6012/26 · HLAVNÝ NÁVRH C / B / B**
$$R0 = 184,200 \text{ m} \cdot M0 = \text{PODLAHA MODELU} \cdot \Delta FFL = M0 - R0 \text{ ZATIAĽ NEURČENÉ}$$

Rozdelenie na dva nadväzujúce listy zachováva 1:50. Hranice a výškové osadenie treba geodeticky overiť. R05 zostáva otvorený

STAV

Chýbajúci návrh sa nesmie nahradiť mierkou výkresu.

VYPRACOVAL: digitálne dvojča · bez autorizačnej pečiatky

DÁTUM 2026-09-14 FORMÁT A1 841 × 594 mm MIERKA 1 : 50

DÁTUM 2026-09-14 FORMÁT A1 841 × 594 mm MIERKA 1 : 50

ZDROJ 6cd4bc82841b - úplné odťahy v model-snapshot.json

Kontrola územného plánu

PARCELA 6012/26 · PRIRADENIE DO Z.7 / SV / ZÓNA C

Priradenie je interpretácia oficiálnej mapy podľa zhodného katastrálneho obrysu. ÚP po zmene č. 3 je účinný od 22.05.2026. Výšková kontrola používa aktuálne pravidlá, nie staré projektové kóty.

Požiadavka	Údaj / zdroj	Stav C/B/B
Rimsa najviac 4,5 m	ÚP I.F.3, tlačená str.34: od najvyššej vozovky po spodnú uličnú rímsu. Pri oznámenom R0 = 184,200 m vychádza limit 188,700 m.	M+3,125 je hrana strešnej roviny, nie overený spodok rímasy. ΔFFL a finálny detail chýbajú.
Sedlová strecha 25–40°	ÚP I.F.3, str.35, zóna C: Modelový obal je záväzný; sklon sa počíta z vrcholov.	30,706180° / 34,826887°: v rozsahu.
Uličná šíra 3 m	Štúdia Z7/Z22, PDF str.2, samostatné domy. Doplnok 2026 o 5 m sa týka radových domov.	Uličný odstup 3 000 mm; hlavný trakt a hrebeň rovnobežne s ulicou.
Odstupy	Štúdia Z7/Z22: k hranici min.2 m, pri obytných miestnostiach medzi domami min.7 m.	Pravá hranica 3 000 mm: Skutočný odstup susedného domu treba overiť.
Podlaha, terén a vstup	Štúdia: podlaha max.0,5 m nad upraveným terénom s väzbou na obrubník; pred domom max.3 stupne. Rimsa max.4,5 m nad podlahou.	Stavebník chce aspoň jeden stupeň; návrhový cieľ 1 × 150 mm pred podestou. Nivelácia pásu, terénu a prahový detail chýbajú.
Zastavanosť, zeleň, parkovanie	ÚP KZP0,7 vrátane spevnených plôch. Štúdia: budovy max.50 %, zeleň min.30 %, dve parkovacie miesta.	Vyžaduje výkaz zjednotených plôch a overenie státi podľa konečnej situácie.

OFICIÁLNE PODKLADY · OVERENÉ 14.09.2026

ÚP po zmene č.3 · I.F.3 str.34–35
https://www.mikulov.cz/data/content_files/831/brez-i-up-oop-uz.pdf

Hlavný výkres I.b
https://www.mikulov.cz/data/content_files/832/1b-hlv-1.pdf

Urbanistická kompozícia I.f · výška4,5m
https://www.mikulov.cz/data/content_files/832/1f-urbanisticka-kompozice.pdf

Štúdia Z7/Z22 + doplnok2026 · PDF2–4
https://www.mikulov.cz/data/content_files/731/textova-cast-souhlas-obce-stavebni-cara-5m.pdf

Vzťah k R0 = 184,200 m	Výška [m]
Hotová podlaha M0	184,200 + ΔFFL
Hrana strešnýchrovín	187,325 + ΔFFL
Hrebeň strešnýchrovín	189,760 + ΔFFL
Limit spodnej uličnej rímasy	188,700 (podmienené R0)

ΔFFL = rozdiel podlahy k ulici v metroch, zatiaľ neurčený. Bp v XY bodu treba potvrdiť. Vizualizačný biely portál siaha nad strešnú rovinu; finálny obal a spodok rímasy určí detail.

KONTROLA TLAČE 100 % - 1 000 mm ≈ 20 mm na papieri
1 : 50 - vypnúť „prispôbiť strane“

NOVOSTAVBA RD BŘEZÍ U MIKULOVA

PARCELA 6012/26 · HLAVNÝ NÁVRH C / B / B

Kontrola územného plánu

R0 = 184,200 m · M0 = PODLAHA MODELU · ΔFFL = M0 – R0 ZATIAĽ NEURČENÉ

Nejde o potvrdenie stavebného úradu. Všetky nesplnené alebo neoverené položky zostávajú otvorené do získania konkrétnych podkladov.

STAV

NEVYDANÉ NA REALIZÁCIU

Chýbajúci návrh sa nesmie nahradiť mierkou výkresu.

VYPRACOVAL: digitálne dvojča · bez autorizačnej pečiatky

DÁTUM 2026-09-14 FORMÁT A1 841 × 594 mm MIERKA tabuľka

ZDROJ 6cd4bc82841b · úplné odtlačky v model-snapshot.json

Výpis okien a vonkajších dverí

O1-O10 / D1-D16 PREVZATÉ BEZ PREČÍSLOVANIA · ROZMERY V MM · 1 KS KAŽDÉHO KÓDU

Kód / zdrojové ID	Rovina / súradnica	Od → do	Š × V / parapet	Krídlo / priechod	Druh / miestnosť
D1 / GARAGE-DOOR	S · Y 3 000	X 6 940 → 10 240	3 300 × 2 400 / 0	neurčené / neurčené	sekčná brána / 1.12
O1 / Výplň otvoru FRONT-02	S · Y 3 000	X 10 942 → 12 192	1 250 × 750 / 1 750	neurčené / neurčené	okno / 1.12
O2 / Výplň otvoru FRONT-03	S · Y 3 000	X 13 588 → 14 338	750 × 750 / 1 750	neurčené / neurčené	okno / 1.11
O3 / Výplň otvoru FRONT-05	S · Y 3 000	X 16 992 → 18 792	1 800 × 1 500 / 900	neurčené / neurčené	okno / 1.08
D2 / Výplň otvoru FRONT-ENTRY	S · Y 3 000	X 21 540 → 22 790	1 250 × 2 250 / 0	neurčené / neurčené	dvere / 1.01
O4 / Výplň otvoru FRONT-07	S · Y 3 000	X 24 442 → 26 442	2 000 × 1 600 / 900	neurčené / neurčené	pevné zasklenie / 1.04
O5 / Bočná výplň otvoru EAST-01	E · X 28 040	Y 5 212 → 6 212	1 000 × 1 600 / 900	neurčené / neurčené	okno / 1.04
O6 / Bočná výplň otvoru EAST-02	E · X 28 040	Y 6 801,5 → 7 401,5	600 × 750 / 1 750	neurčené / neurčené	okno / 1.05
D3 / Bočná výplň otvoru EAST-03	E · X 28 040	Y 9 000 → 9 900	900 × 2 250 / 0	neurčené / 648	dvere / 1.07
O7 / Bočná výplň otvoru EAST-04	E · X 28 040	Y 11 800 → 12 800	1 000 × 1 600 / 900	neurčené / neurčené	okno / 1.03
O8 / Krytá terasa-glazing	NN2 · Y 19 535	X 22 040 → 24 040	2 000 × 2 750 / 0	neurčené / neurčené	pevné zasklenie / 1.03
D4 / Terasové posuvné presklenie 2 250	WW · X 21 040	Y 11 550 → 13 800	2 250 × 2 400 / 0	neurčené / neurčené	posuvné / 1.03
O9 / Výplň otvoru GARDEN-03	N · Y 11 200	X 16 992 → 18 792	1 800 × 1 500 / 900	neurčené / neurčené	okno / 1.09
D5 / Terasové presklenie 2500	N · Y 11 200	X 11 840 → 14 340	2 500 × 2 400 / 0	neurčené / neurčené	posuvné / 1.10
O10 / Bočné garážové okno WEST-GARAGE-01	W · X 6 440	Y 4 358 → 5 608	1 250 × 750 / 1 750	neurčené / neurčené	okno / 1.12
D6 / LOGGIA-DOOR	L · Y 9 247	X 9 086 → 10 336	1 250 × 2 400 / 0	neurčené / neurčené	dvere / 1.12
O11 / svetlík nad O8	NN2 · Y 19 535	X 22 040 → 24 040	2 000 × 1 419,65 / 3 050	pevné / neprechodné	trojuholník / 1.03

Uvedené rozmery patria otvorom v modeli. Výrobný rozmer rámu, montážna škára, profily, prah, zasklenie, kovanie a požadované vlastnosti zatiaľ nie sú špecifikované. Údaje označené „neurčené“ nemožno odvodiť od oka.

O11 je doplnený kód svetlíka nad rovinou pôdorysného rezu. Trojuholník nie je obdĺžnik: vrcholy X|Z [mm] (22040;3050), (24040;3050), (24040;4469,649650). Rozmer z geometrie rendereru; výrobná šablóna a osadenie sa musia dopracovať.

KONTROLA TLAČE 100 % - 1 000 mm = 20 mm na papieri

1 : 50 - vypnúť „prispôbiť strane“

NOVOSTAVBA RD BŘEZÍ U MIKULOVA

PARCELA 6012/26 · HLAVNÝ NÁVRH C / B / B

Výpis okien a vonkajších dverí

R0 = 184,200 m · M0 = PODLAHA MODELU · ΔFFL = M0 – R0 ZATIAĽ NEURČENÉ

R09: modelový výpis je koordinovaný s pôdorysom, výrobná špecifikácia nie je uzavretá. O11 pridáva chýbajúci horný svetlík.

STAV

NEVYDANÉ NA REALIZÁCIU

Chýbajúci návrh sa nesmie nahradiť mierkou výkresu.

VYPRACOVAL: digitálne dvojča · bez autorizačnej pečiatky

DÁTUM 2026-09-14 FORMÁT A1 841 × 594 mm MIERKA tabuľka

ZDROJ 6cd4bc82841b · úplné odtlačky v model-snapshot.json

Výpis vnútorných dverí

O1-O10 / D1-D16 PREVZATÉ BEZ PREČÍSLOVANIA · ROZMERY V MM · 1 KS KAŽDÉHO KÓDU

Kód / zdrojové ID	Rovina / súradnica	Od → do	Š × V / parapet	Krídlo / priechod	Druh / miestnosť
D7 / DOOR-101-102	interiér - Y 6 482	X 21 640 → 22 540	900 × 2 100 / 0	900 / neurčené	do puzdra / 1.02; posun -X 950 mm
D8 / DOOR-102-104	interiér - X 22 740,5	Y 5 421 → 6 322	901 × 2 100 / 0	800 / neurčené	otočné / 1.04; pánt nižšia súradnica; smer +X
D9 / DOOR-102-105	interiér - X 22 711	Y 6 701,5 → 7 501,5	800 × 2 100 / 0	700 / neurčené	otočné / 1.05; pánt nižšia súradnica; smer +X
D10 / DOOR-102-106	interiér - X 22 711	Y 9 866 → 10 666	800 × 2 100 / 0	700 / neurčené	otočné / 1.06; pánt vyššia súradnica; smer +X
D11 / DOOR-103-107	interiér - Y 10 862	X 26 081 → 26 881	800 × 2 100 / 0	700 / neurčené	otočné / 1.07; pánt vyššia súradnica; smer +Y
D12 / DOOR-102-108	interiér - Y 6 482	X 17 442 → 18 342	900 × 2 100 / 0	800 / neurčené	otočné / 1.08; pánt vyššia súradnica; smer -Y
D13 / DOOR-102-109	interiér - Y 7 721	X 17 442 → 18 342	900 × 2 100 / 0	800 / neurčené	otočné / 1.09; pánt vyššia súradnica; smer +Y
D14 / C-PRIVATE-BED	interiér - Y 7 721	X 13 943 → 14 743	800 × 2 100 / 0	800 / neurčené	otočné / 1.10; pánt vyššia súradnica; smer +Y
D15 / C-HALL-BATH	interiér - Y 6 482	X 13 943 → 14 743	800 × 2 100 / 0	800 / neurčené	otočné / 1.11; pánt vyššia súradnica; smer -Y
D16 / C-BED-CLOSET	interiér - Y 7 721	X 11 793 → 12 593	800 × 2 100 / 0	800 / neurčené	do puzdra / 1.14; posun +X 850 mm

Uvedené rozmery patria otvorom v modeli. Výrobný rozmer rámu, montážna škára, profily, prah, zasklenie, kovanie a požadované vlastnosti zatiaľ nie sú špecifikované. Údaje označené „neurčené“ nemožno odvodiť od oka.

Orientácia krídel sa preberá z existujúceho pôdorysu; osi, otvory aj kódy sú zachované. Dodávateľ má potvrdiť zárubne, svetlú priechodnosť, výšku prahu a montážne tolerancie, najmä pri H200 a akustických priečkach.

KONTROLA TLAČE 100 % - 1 000 mm ≈ 20 mm na papieri

1 : 50 - vypnúť „prispôbiť strane“

NOVOSTAVBA RD BŘEZÍ U MIKULOVA

PARCELA 6012/26 · HLAVNÝ NÁVRH C / B / B

Výpis vnútorných dverí

R0 = 184,200 m · M0 = PODLAHA MODELU · ΔFFL = M0 – R0 ZATIAĽ NEURČENÉ

R09: modelový výpis je koordinovaný s pôdorysom, výrobná špecifikácia nie je uzavretá. O11 pridáva chýbajúci horný svetlík.

STAV

NEVYDANÉ NA REALIZÁCIU

Chýbajúci návrh sa nesmie nahradiť mierkou výkresu.

VYPRACOVAL: digitálne dvojča · bez autorizačnej pečiatky

DÁTUM 2026-09-14 FORMÁT A1 841 × 594 mm MIERKA tabuľka

ZDROJ 6cd4bc82841b · úplné odtlačky v model-snapshot.json

Skladby konštrukcií · register

AKTÍVNE SKLADBY STIEN · STARÉ PODLAHY A STRECHA SA NEPREBERAJÚ

Kód	Aktuálna geometria / skladba	Stav pre realizáciu
SO30 + TI20	Nosné murivo 300 + vonkajšie kontaktné zateplenie 200 = 500 mm nominálne. Pôdorysné líca miestností zostávajú; lokálne odstupy líc modelu 499–504 mm sa neprepisujú.	Určiť výrobok, omietky a finálne líca, statiku a systémové napojenia.
SO50	Voľné piliere / steny krytých terás: plné murivo 500 mm bez ETICS.	Overiť únosnosť, stabilitu, založenie, povrchy.
SN30, SN20	Nosné vnútorné murivo z keramikých tvaroviek hr. 300 / 200 mm, na systémovú murovaciu maltu	Kódy a nominálne hrúbky z hotového pôdorysu. Nový výrobok, úplné vrstvy, kotvenie a nosnú funkciu uzavrieť v R01/R04/R07.
SP30, SP20, SP14	Nenosné priečkové murivo z keramikých tvaroviek hr. 300 / 200 / 140 mm, na systémovú murovaciu maltu (vrátane puzdra posuvných dverí)	Kódy a nominálne hrúbky z hotového pôdorysu. Nový výrobok, úplné vrstvy, kotvenie a nosnú funkciu uzavrieť v R01/R04/R07.
SP10, SP6	Sadrokartónové systémové priečky a predsteny hr. 100 / 60 mm, s výpňou z minerálnej vlny	Kódy a nominálne hrúbky z hotového pôdorysu. Nový výrobok, úplné vrstvy, kotvenie a nosnú funkciu uzavrieť v R01/R04/R07.
SA30	Leier LeierPLAN 10 P10 100 mm + Minerálna vata 100 mm + Leier LeierPLAN 10 P10 100 mm = 300 mm. 300 mm = 100 + 100 + 100 mm bez omietok a obkladov. Líca v pôdoryse zostávajú zachované; povrchové úpravy sa určia samostatne.	Návrh nenosnej priečky: Pôvodné označenie týchto úsekov bolo nosné; zmenu nosného systému a podopretie nadväzujúcich konštrukcií musí overiť statik.
H200	Knauf Silentboard · vonkajšia doska pracovne 12,5 mm + Knauf Silentboard · vnútorná doska 12,5 mm + Dutina W623 · pružné závesy, CD 60/27 a vata 40 mm 45 mm + Súvislá vápenno-cementová omietka · dutina 15 mm + LeierPLAN 10 N+F · murivo 100 mm + Vápenno-cementová omietka · kúpeľňa 15 mm = 200 mm. 200 mm = 15 + 100 + 15 + 45 + 25 mm od sprchy, vrátane oboch omietok a dosiek. Vata 40 mm aj rošt sú v 45 mm dutine. Hydroizolácia, lepidlo, obklad a prípadná celoplošná stierka sú navyše.	Nenosná priečka H200. Statik overí stabilitu LeierPLAN 10 pri výške 3 125 mm, založenie, napojenie a náhradu pôvodnej nosnej funkcie. Kotvy a rozstup pružných závesov zvoliť pre konkrétne dutinové murivo a hmotnosť opláštenia.
PODLAHY	M0 = pôvodná podlaha, ΔFFL k ulici R0 neznáme. Voda a odpad nad doskou; kúrenie mimo garáže, technickej a sprchy; TZ-01.	Určiť hrúbky, spády, izolácie, vykurovací poter a povrchy. Bez vrtov do dosky.
STRECHA / POVALA	Falcovaný plech, bez architektonických presahov. Roviny M+3,125 / M+5,560; povala iba na odkladanie mimo katedrály 1.03.	Drevený nosný strop a záklop; bez betónovej stropnej dosky/nadbetonávky. Určiť skladovacie a bodové zariadenia, prierezy, spoje, vrstvy a parotesnosť.
ZÁKLADY / DOSKA	Monolitický horný pás 350 × 600 mm; vnútorné rebrá; požadovaná doska 150–200 mm. Podľa zadania, nie zamerania. ZA-02.	Overiť zemínu, už realizovaný pás, C16/20 a jeho expozíciu; navrhnuť rozmery, výstuž a škáry.

H200: požiadavka $R_w \geq 51$ dB. Predbežný výpočet z podkladov nie je meranie ani potvrdenie konkrétnej realizácie. SA30: R_w celej zostavy nedoložené. Akustika aj kotvenie sa musia posúdiť pre nové nosné riešenie.

KONTROLA TLAČE 100 % - 1 000 mm = 20 mm na papieri

1 : 50 - vypnúť „prispôbiť strane“

NOVOSTAVBA RD BŘEZÍ U MIKULOVA

PARCELA 6012/26 · HLAVNÝ NÁVRH C / B / B

Skladby konštrukcií · register

R0 = 184,200 m · M0 = PODLAHA MODELU · ΔFFL = M0 – R0 ZATIAĽ NEURČENÉ

Zachované sú rozhodnuté materiály a líca. Chýbajúce nové konštrukcie sú explicitne otvorené; staré rozporné skladby a statika sa nepoužívajú.

STAV

NEVYDANÉ NA REALIZÁCIU

Chýbajúci návrh sa nesmie nahradiť mierkou výkresu.

VYPRACOVAL: digitálne dvojča · bez autorizačnej pečiatky


DÁTUM 2026-09-14 FORMÁT A1 841 × 594 mm MIERKA tabuľka

ZDROJ 6cd4bc82841b · úplné odtlačky v model-snapshot.json

Akustické steny H200 / SA30


AK-01 / AK-02 / AK-03 - GEOMETRIA VRSTIEV A NAPOJENÍ

SA30 - Dvojlášt'ová akustická priečka

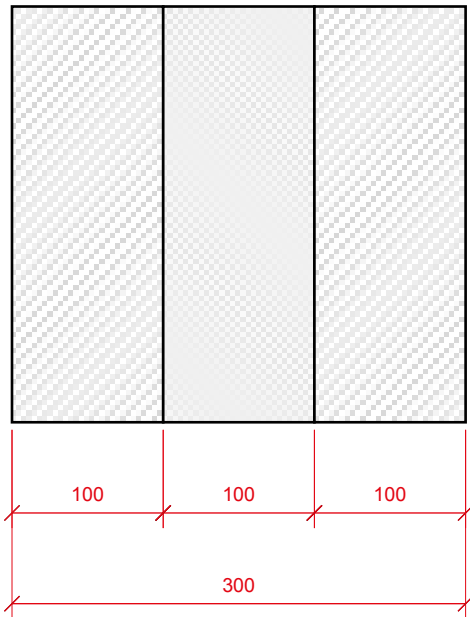


Vrstva	Hrúbka [mm]
Leier LeierPLAN 10 P10	100
Minerálna vata	100
Leier LeierPLAN 10 P10	100

H200 - LeierPLAN 10 + akustická predstena Silentboard

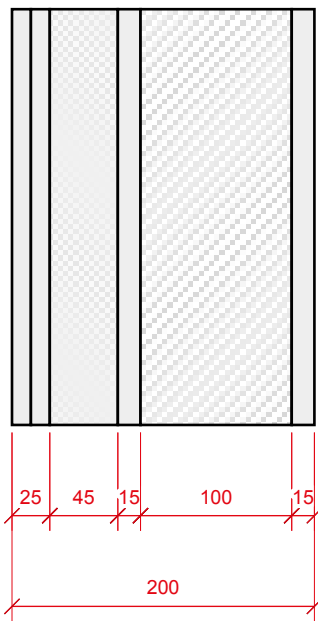

Vrstva	Hrúbka [mm]
Knauf Silentboard - vonkajšia doska pracovne	12,5
Knauf Silentboard - vnútorná doska	12,5
Dutina W623 - pružné závesy, CD 60/27 a vata 40 mm	45
Súvislá vápenno-cementová omietka - dutina	15
LeierPLAN 10 N+F - murivo	100
Vápenno-cementová omietka - kúpeľňa	15

D1 - D-AK03-01 / R1 - PRI ZÁRUBNIACH - 1 : 5

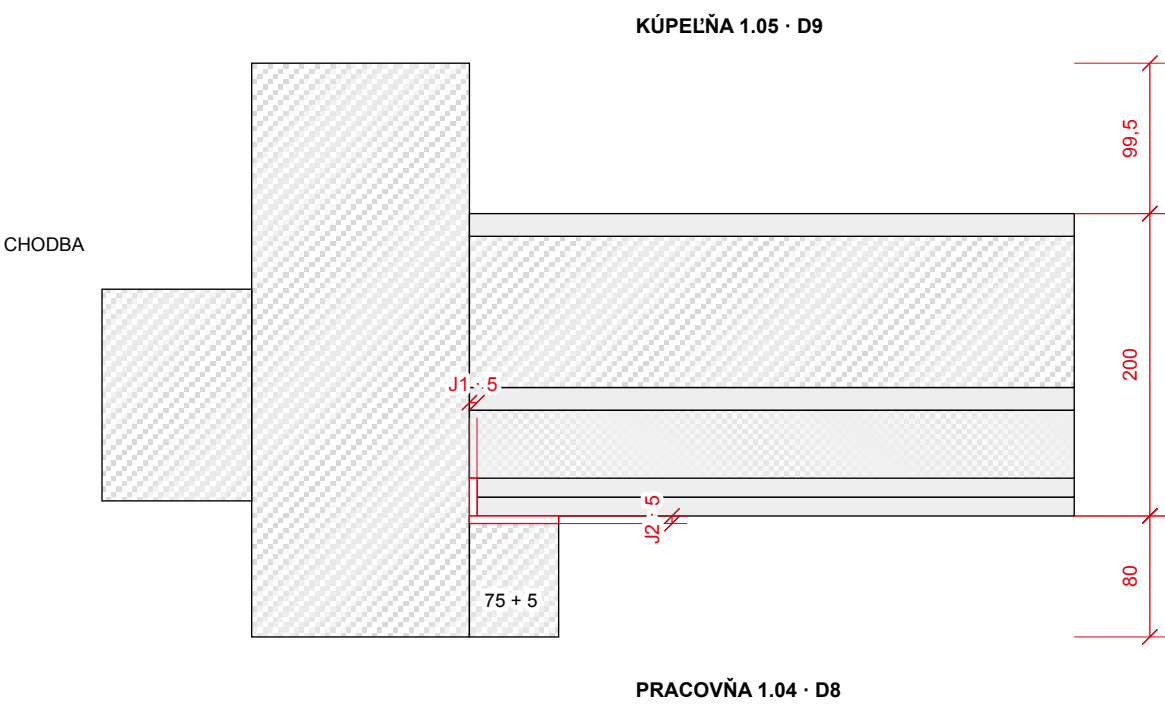

Spoj / súradnice [mm]	Predpis existujúceho detailu
J1 - X 22 783-22 788 / Y 6 402-6 427	Čelá oboch dosiek: 5 mm, Trenn-Fix + Uniflott podľa princípu W623-B2.
J2 - X 22 783-22 842 / Y 6 397-6 402	5 mm mäkké oddelenie pri lici vonkajšej dosky. Pružný akustický tmel na vhodnej podkladovej vrstve; bez sadry alebo malty.

Súradnice predstavujú návrhovú rezervu v nominálnom pôdoryse; realizačná škára sa meria od hotového kontaktného povrchu. Veľký pôdorys a 3D zachovávajú obálku konštrukcie. Ich plná výplň v mierke domu nepredpisuje zaliatie škár J1/J2. Záväzný princíp ich vyhotovenia je v tomto zväčšenom detaile.

Obvodový UD, podtesnenie a mechanické kotvy nie sú v tejto schéme určené. R07: dopracovať kotvy, závesy, stabilitu muríva, spoje pri podlahe a stropce a hydroizoláciu sprchy. J2 je projektový detail, nie skúšaný katalógový spoj.

KONTROLA TLAČE 100 % - 100 mm = 20 mm na papieri
1 : 5 - vypňoť „prispôbiť strane“

NOVOSTAVBA RD BŘEZÍ U MIKULOVA

PARCELA 6012/26 - HLAVNÝ NÁVRH C / B / B

Akustické steny H200 / SA30

R0 = 184,200 m - M0 = PODLAHA MODELU - ΔFFL = M0 - R0 ZATIAĽ NEURČENÉ

Vrstvy z lib/acoustic-walls.ts. J1/J2 z lib/h200-junction.json. Detail vrstiev 1:5; realizačné kotvenie a nosné napojenia vyžadujú nový návrh.

STAV

NEVYDANÉ NA REALIZÁCIU


Chýbajúci návrh sa nesmie nahradiť mierkou výkresu.

VYPRACOVAL: digitálne dvojča - bez autorizačnej pečiatky

DÁTUM 2026-09-14 FORMÁT A1 841 × 594 mm MIERKA 1 : 5

ZDROJ 6cd4bc82841b - úplné odlišky v model-snapshot.json

Podlahové vykurovanie a rozsah povaly

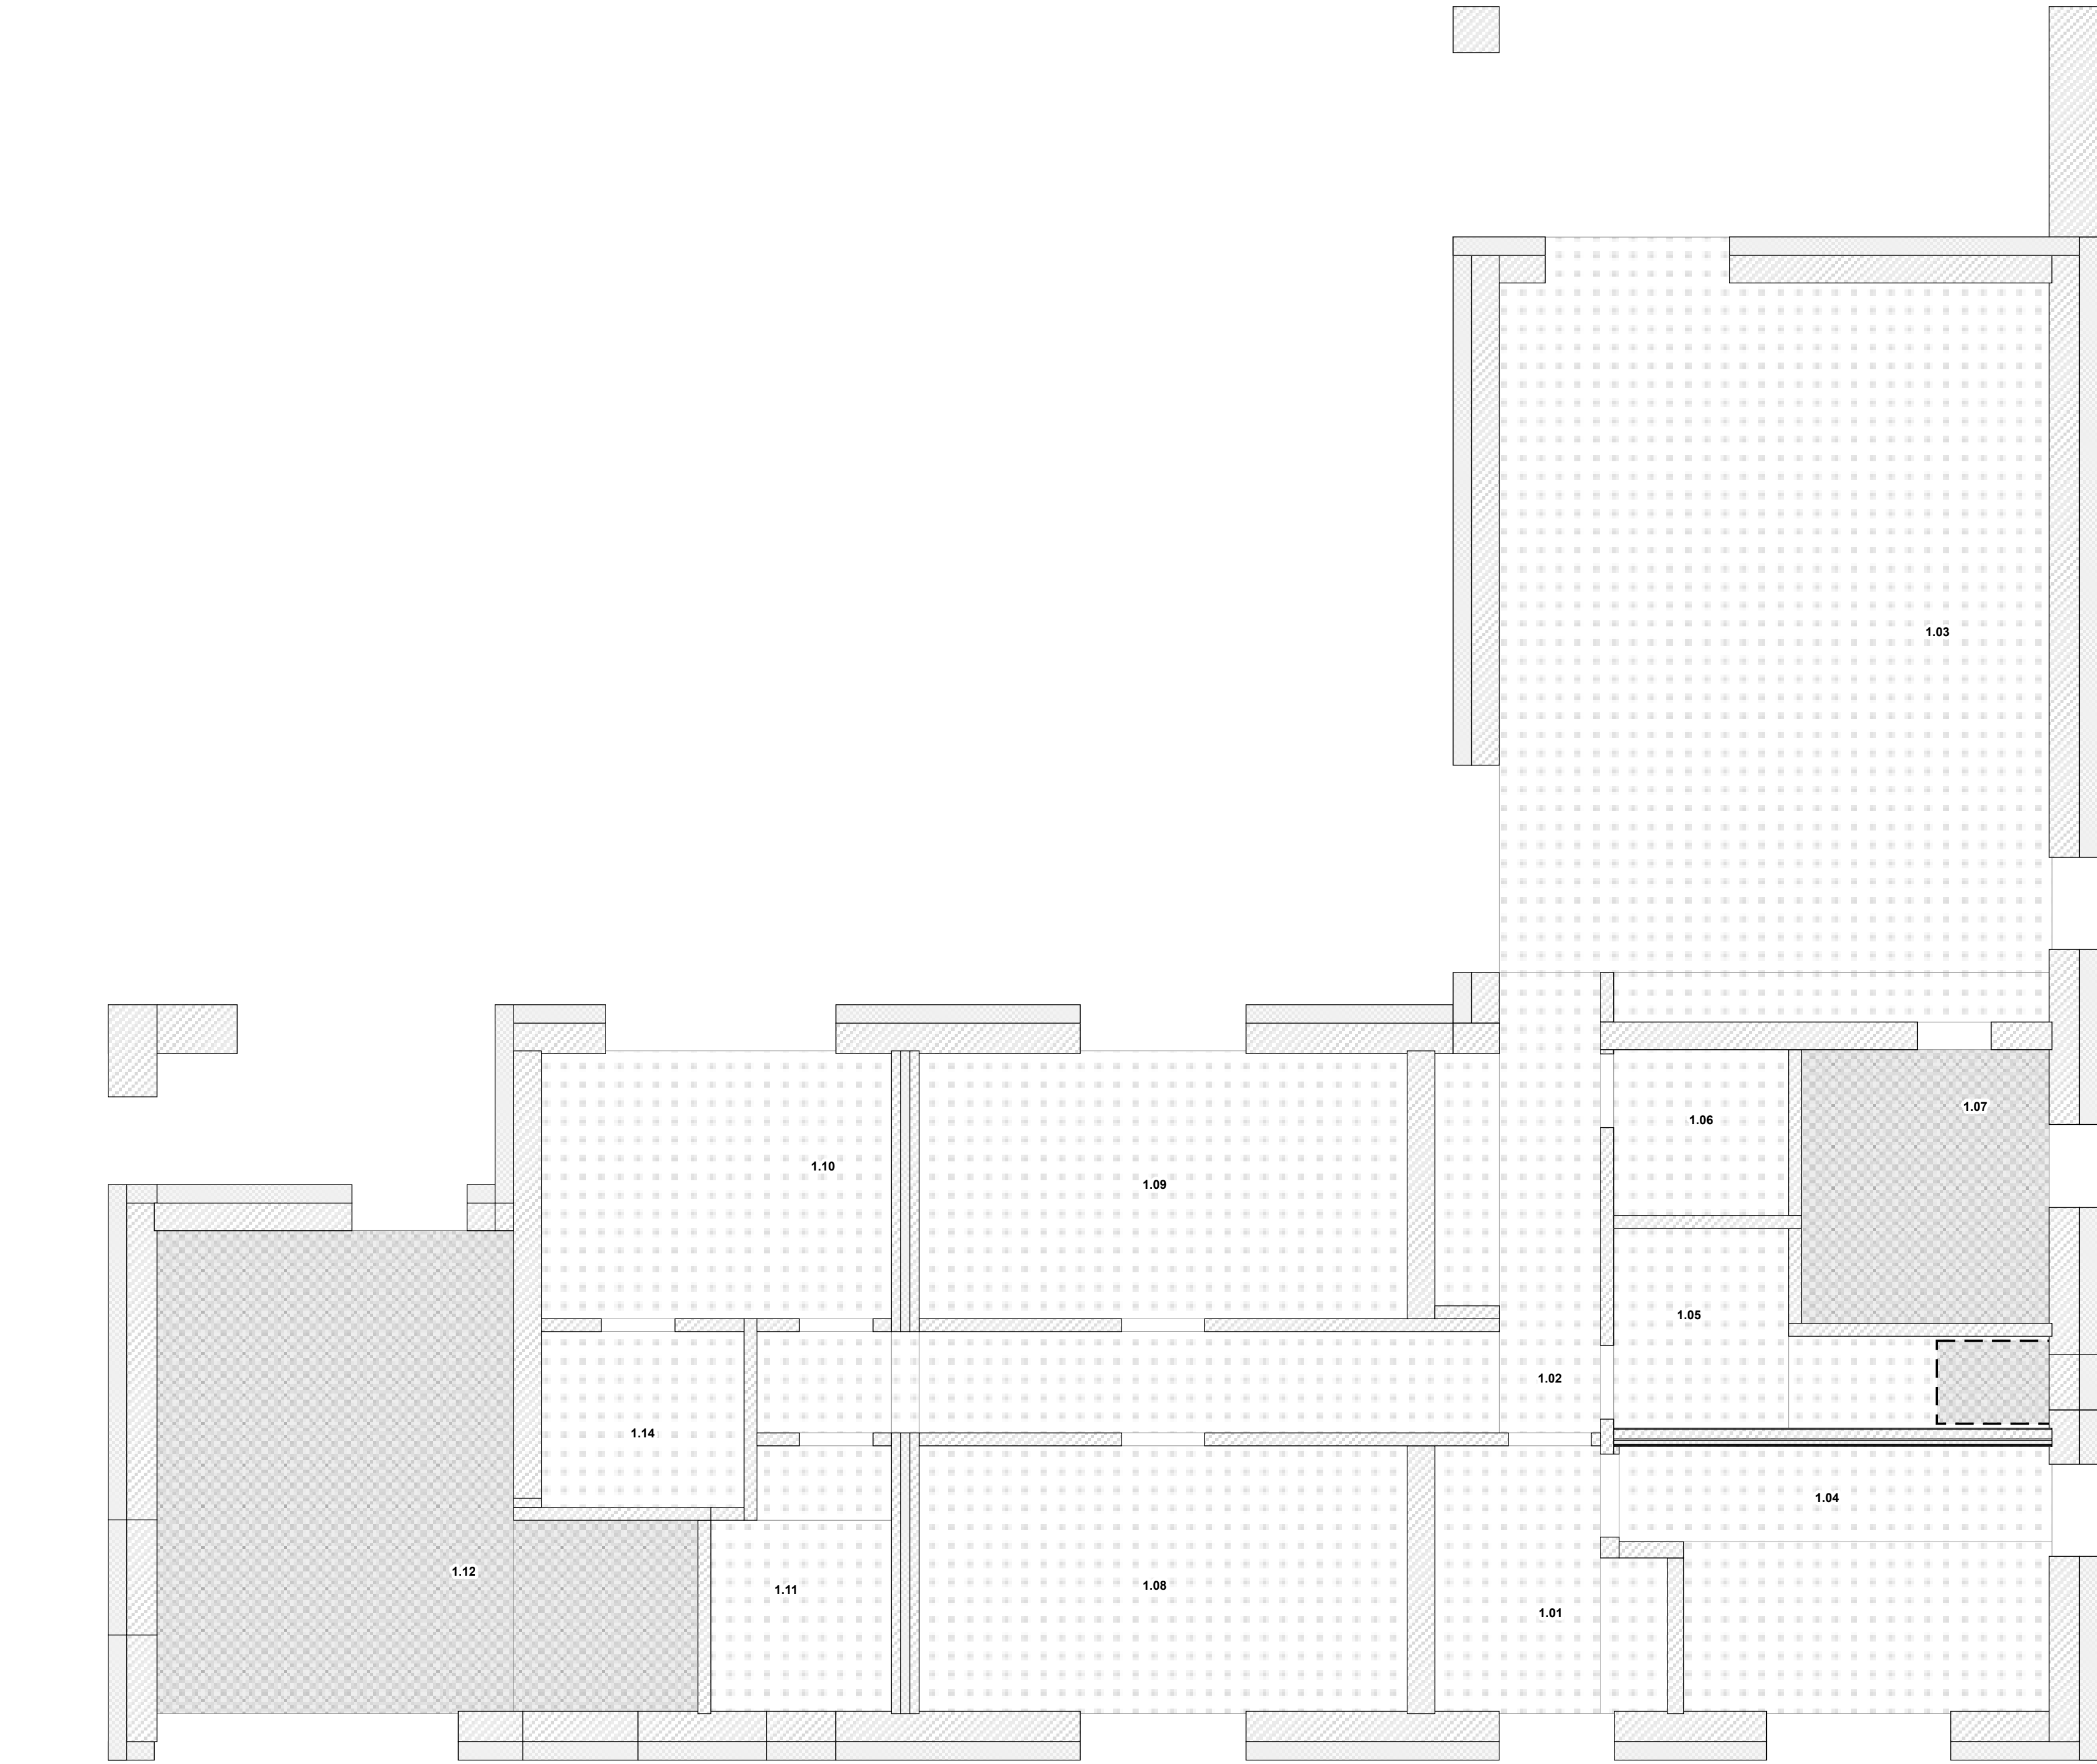

VODA A ODPAD NAD NOSNOU DOSKOU - ŽIADNE DODATOČNÉ VRTY DO DOSKY

Výšky trasovania, priemery, spády, izolačné hrúbky, vývody cez obvod a skladby vykurovaných aj nevykurovaných podláh zostávajú súčasťou nového profesijného návrhu.

KONTROLA TLAČE 100 % - 1 000 mm ≈ 20 mm na papieri

1 : 50 - vypnúť „prispôbiť strane“

NOVOSTAVBA RD BŘEZÍ U MIKULOVA

PARCELA 6012/26 - HLAVNÝ NÁVRH C / B / B

Podlahové vykurovanie a rozsah povaly

R0 = 184,200 m · M0 = PODLAHA MODELU · ΔFFL = M0 - R0 ZATIAĽ NEURČENÉ

Pôdorysná geometria bez zmeny. Nové požiadavky stavebníka sú zakreslené k miestnostiam; list nie je výpočtom kúrenia ani statickým návrhom pochôdzného stropu.

ROZSAH PODLAHOVÉHO VYKUROVANIA

Miestnosť	Rozsah zadania
1.01	Podlahové vykurovanie
1.02	Podlahové vykurovanie
1.03	Podlahové vykurovanie
1.04	Podlahové vykurovanie
1.05	Áno; okrem sprchovej plochy
1.06	Podlahové vykurovanie
1.07	Bez podlahového vykurovania
1.08	Podlahové vykurovanie
1.09	Podlahové vykurovanie
1.10	Podlahové vykurovanie
1.11	Podlahové vykurovanie
1.12	Bez podlahového vykurovania
1.14	Podlahové vykurovanie

Priestor s požadovaným vykurovaním

Vylúčený priestor / sprcha

Sprcha z modelu: X 26 291–27 541; Y 6 652–7 552 mm. Slovo „sprcha“ je vyložené ako sprchová plocha; vylúčenie celej kúpeľne 1.05 nebolo zadané.

Bodkovaná plocha znamená požadovaný rozsah vykurovania, nie kľadačský plán rúrok. Nábytok, steny a zariadenia, tepelné straty, okruhy, rozstupy a regulácia musia vstúpiť do samostatného výpočtu.

POVALA: potvrdená iba na odkladanie vecí. Drevené stropy a záklop, bez betónovej stropnej dosky a nadbetónávky. Rozsah zahŕňa garáž aj technickú; nad 1.03 zostáva otvorená katedrála. Skladovacie a bodové zataženia ešte treba navrhnuť.

STAV

NEVYDANÉ NA REALIZÁCIU

Chýbajúci návrh sa nesmie nahradiť mierkou výkresu.

VYPRACOVAL: digitálne dvojča - bez autorizačnej pečiatky

DÁTUM 2026-09-14 FORMÁT A1 841 × 594 mm MIERKA 1 : 50

ZDROJ 6cd4bc82841b - úplné odtlačky v model-snapshot.json