


Situácia osadenia · ulica

ULIČNÁ ČASŤ · nadväzuje SI-02 · prekrytie Y 17 500–21 000 mm

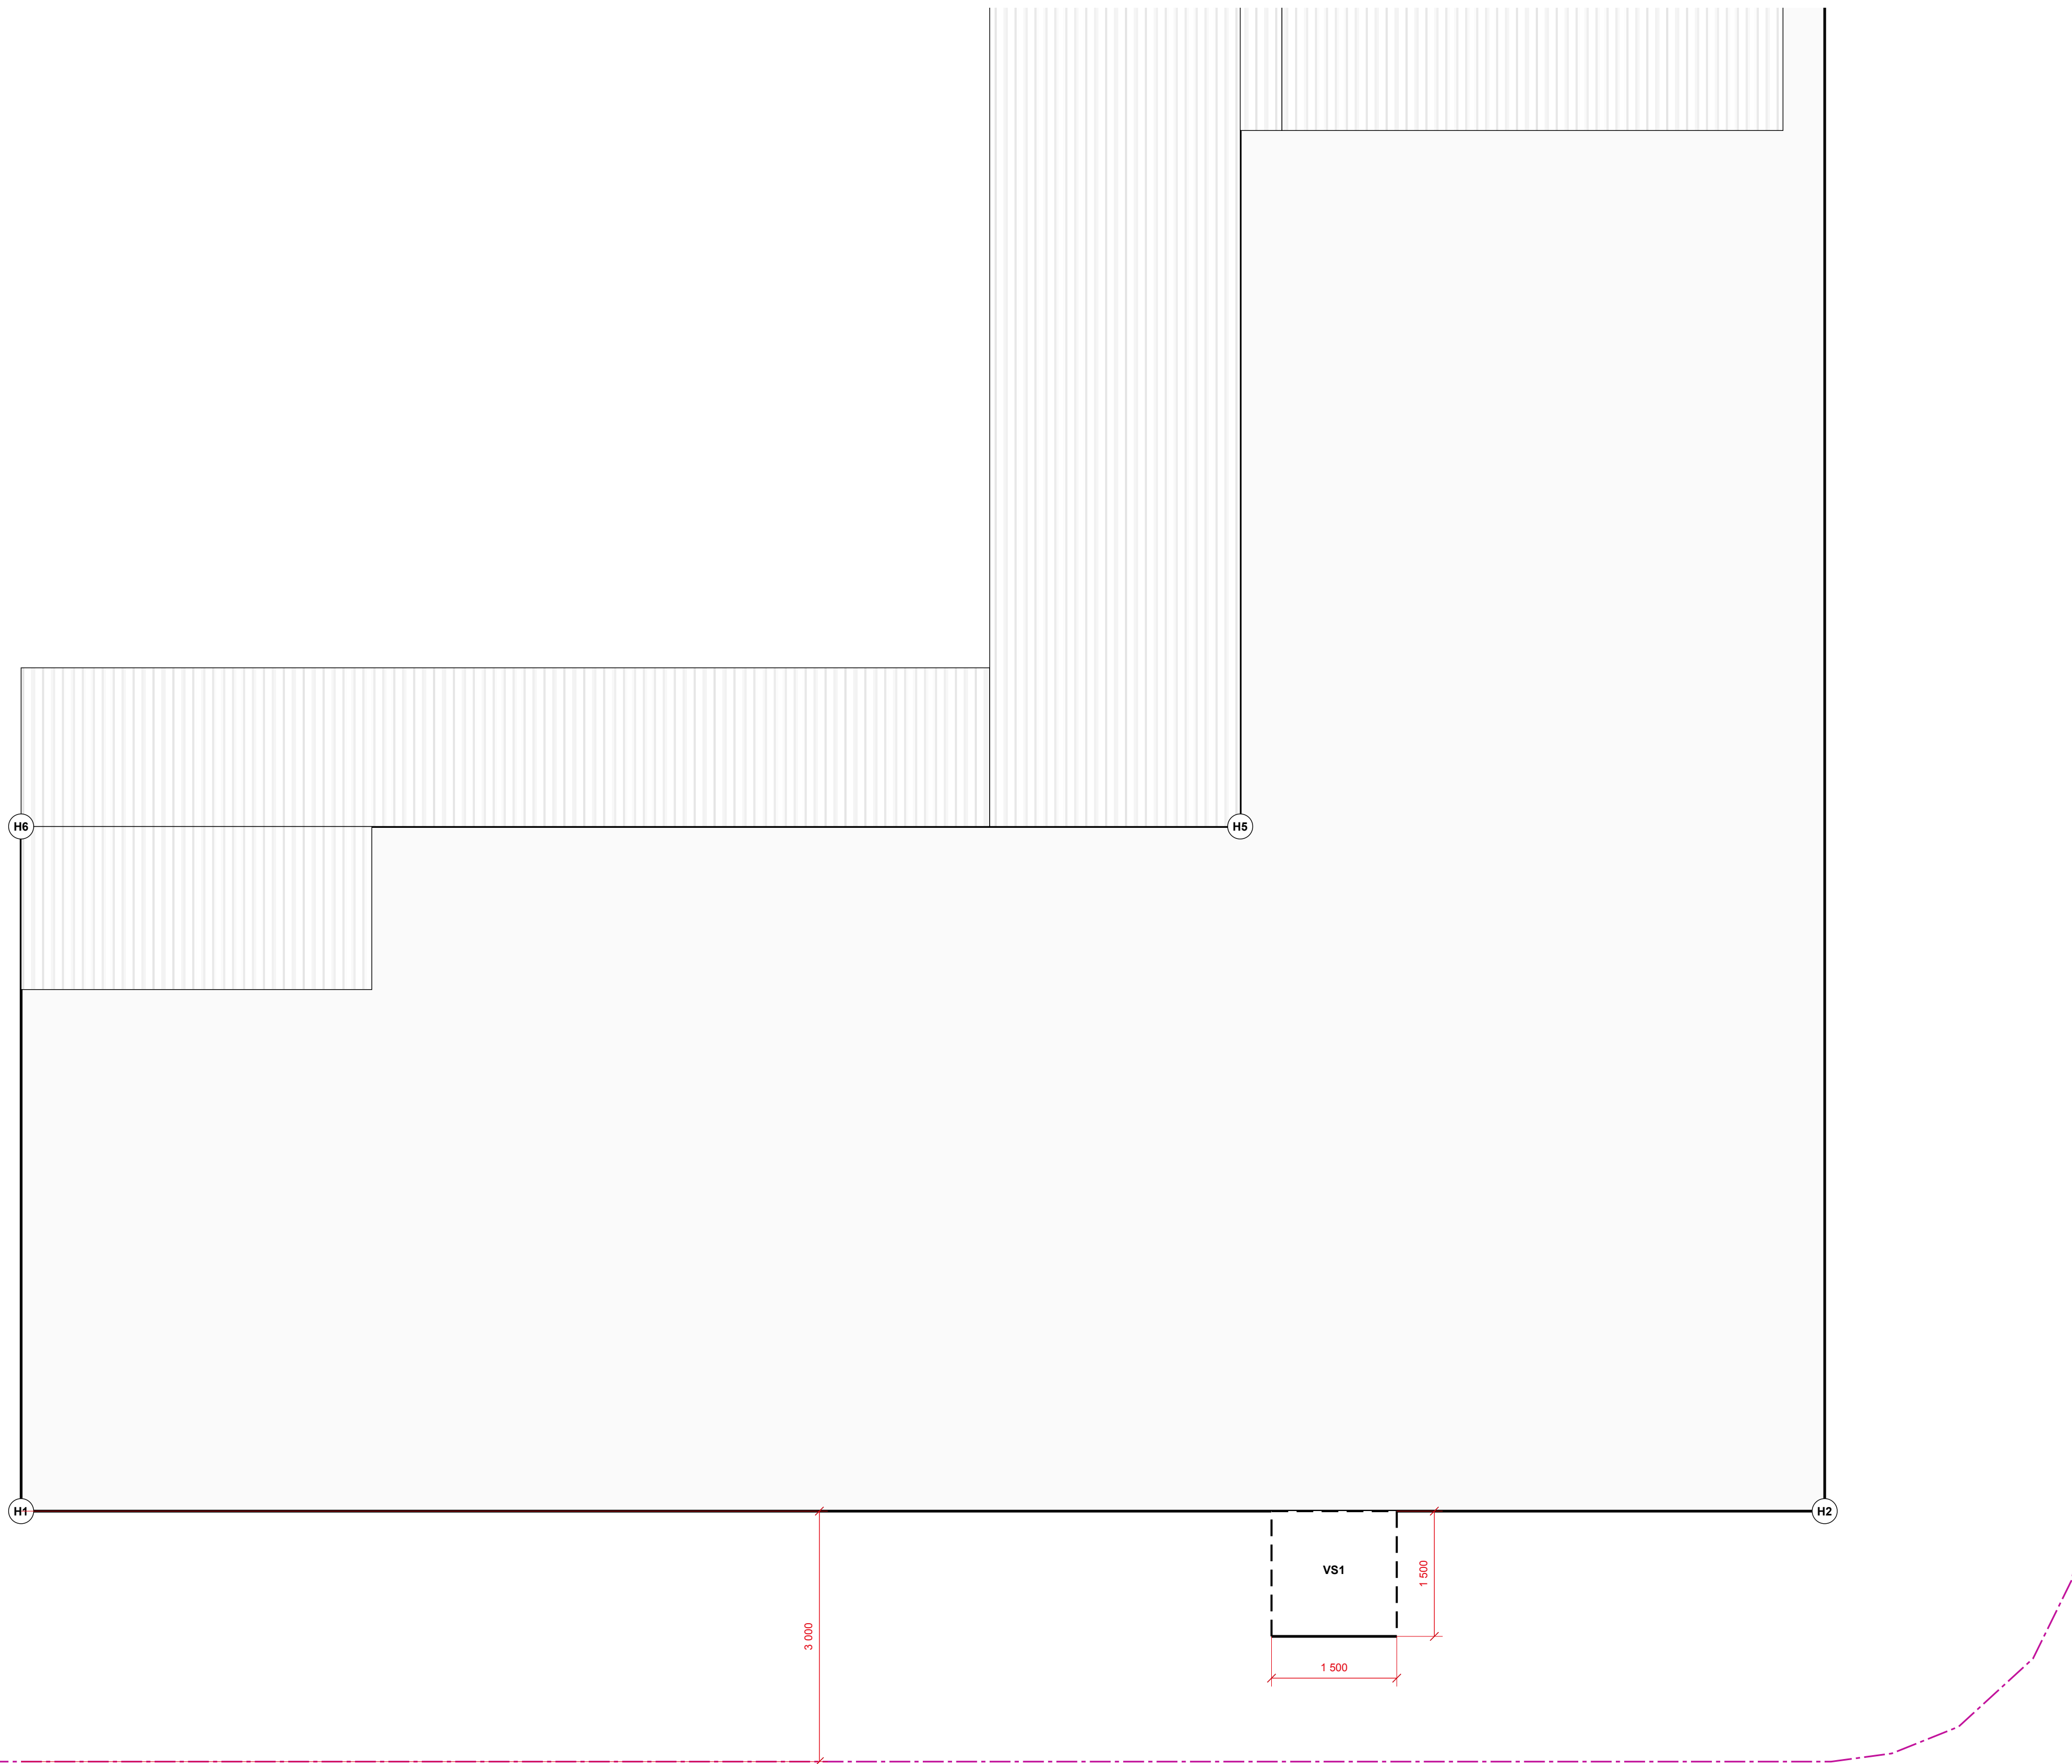

PARCELA 6012/26. Uličný aj pravý KOLMÝ odstup 3 000 mm. Jediný súradnicový rámec C/B/B.

Katastrálna hranica a požadované osadenie nie sú geodetické vytyčenie. Pred stavbou overiť hranice a výškopis.

VS1 · NÁVRH VSTUPU

Pri D2: podesta 1 500 × 1 500 mm v existujúcom prístupe. Čelo Y 1 500; dvere sa otvárajú dovnútra.

Jeden stupeň h = 150 mm je návrhový cieľ. Výšky podesty a prístupu, spád a prah sú otvorené; výšková väzba ZA-02. Nejde o zameraný ani realizačný stav.

Schod je pred podestou. Jeho výška sa meria od miestneho prístupu; neznamená podlahu 150 mm nad ulicou R0.

KONTROLA TLAČE 100 % - 1 000 mm ≈ 20 mm na papieri

1 : 50 - vypnúť „prispôbiť strane“

NOVOSTAVBA RD BŘEZÍ U MIKULOVA

PARCELA 6012/26 · HLAVNÝ NÁVRH C / B / B

Situácia osadenia · ulica

R0 = 184,200 m · M0 = PODLAHA MODELU · ΔFFL = M0 – R0 ZATIAĽ NEURČENÉ

Rozdelenie na dva nadväzujúce listy zachováva 1:50. Hranice a výškové osadenie treba geodeticky overiť. R05 zostáva otvorený.

STAV

NEVYDANÉ NA REALIZÁCIU

Chýbajúci návrh sa nesmie nahradiť mierkou výkresu.

VYPRACOVAL: digitálne dvojča · bez autorizačnej pečiatky

DÁTUM 2026-09-14 FORMÁT A1 841 × 594 mm MIERKA 1 : 50

ZDROJ 6cd4bc82841b · úplné odtlačky v model-snapshot.json