


Situácia osadenia · záhrada

ZÁHRADNÁ ČASŤ · nadväzuje SI-01 · prekrytie Y 17 500–21 000 mm

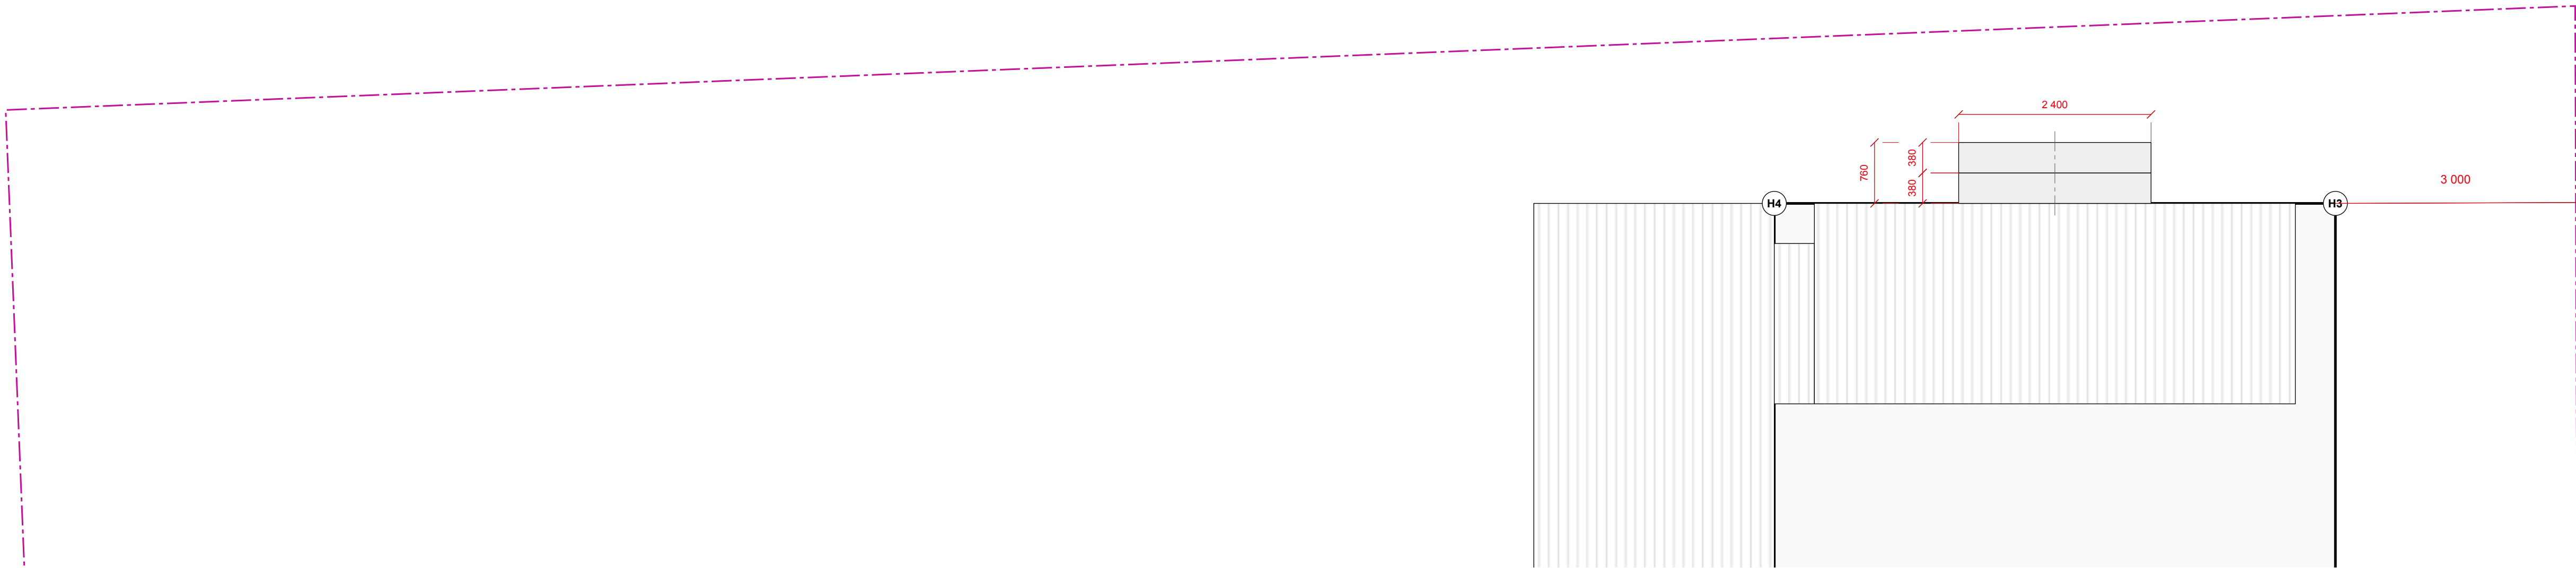

PARCELA 6012/26. Uličný aj pravý KOLMÝ odstup 3 000 mm. Jediný súradnicový rámec C/B/B.

Katastrálna hranica a požadované osadenie nie sú geodetické vytyčenie. Pred stavbou overiť hranice a výškopis.

Bod	X [mm]	Y [mm]	Prvok
H1	6 440	3 000	vonkajšie lico
H2	28 040	3 000	vonkajšie lico
H3	28 040	22 035	vonkajšie lico
H4	21 040	22 035	vonkajšie lico
H5	21 040	11 200	vonkajšie lico
H6	6 440	11 200	vonkajšie lico

Počiatok lokálneho rámca S-JTSK [mm]: X -606 705 098,323, Y -1 202 056 601,691. Posun oproti C3: 77,913 mm v X.

R0 = 184,200 m: najvyšší bod ulice pri pracovni podľa stavebníka. Spodná uličná rímsa má podmienený limit 188,700 m. Presné XY bodu, Bpv a rozdiel ΔFFL podlahy k R0 treba potvrdiť; bod sa preto neumiestňuje odhadom.

Štúdia Z7/Z22: pre samostatný dom uličná čiara 3 m. Overiť 7 m medzi obytnými domami, plochy zelene, spevnenie a dve parkovacie miesta. Podrobné zdroje a otvorené kontroly: UP-01.

Voda a odpad sa vedú nad nosnou doskou. Vývody a ich úrovne cez obvodovú konštrukciu musia byť určené v novom návrhu; žiadne dodatočné vŕtanie dosky.

Vytyčenie stupňov: spoločná os X 24 540 mm; prvé čelo Y 22 035 mm = os 6. Krajné líca X 23 340 / 25 740 mm. Odstupy od vonkajších líc kridla: 2 300 mm / 2 300 mm.

KONTROLA TLAČE 100 % - 1 000 mm ≈ 20 mm na papieri

1 : 50 - vypnúť „prispôbiť strane“

NOVOSTAVBA RD BŘEZÍ U MIKULOVA

PARCELA 6012/26 · HLAVNÝ NÁVRH C / B / B

Situácia osadenia · záhrada

R0 = 184,200 m · M0 = PODLAHA MODELU · ΔFFL = M0 – R0 ZATIAĽ NEURČENÉ

Rozdelenie na dva nadväzujúce listy zachováva 1:50. Hranice a výškové osadenie treba geodeticky overiť. R05 zostáva otvorený.

STAV

NEVYDANÉ NA REALIZÁCIU

Chýbajúci návrh sa nesmie nahradiť mierkou výkresu.

VYPRACOVAL: digitálne dvojča · bez autorizačnej pečiatky

DÁTUM 2026-09-14 FORMÁT A1 841 × 594 mm MIERKA 1 : 50

ZDROJ 6cd4bc82841b · úplné odtlačky v model-snapshot.json