


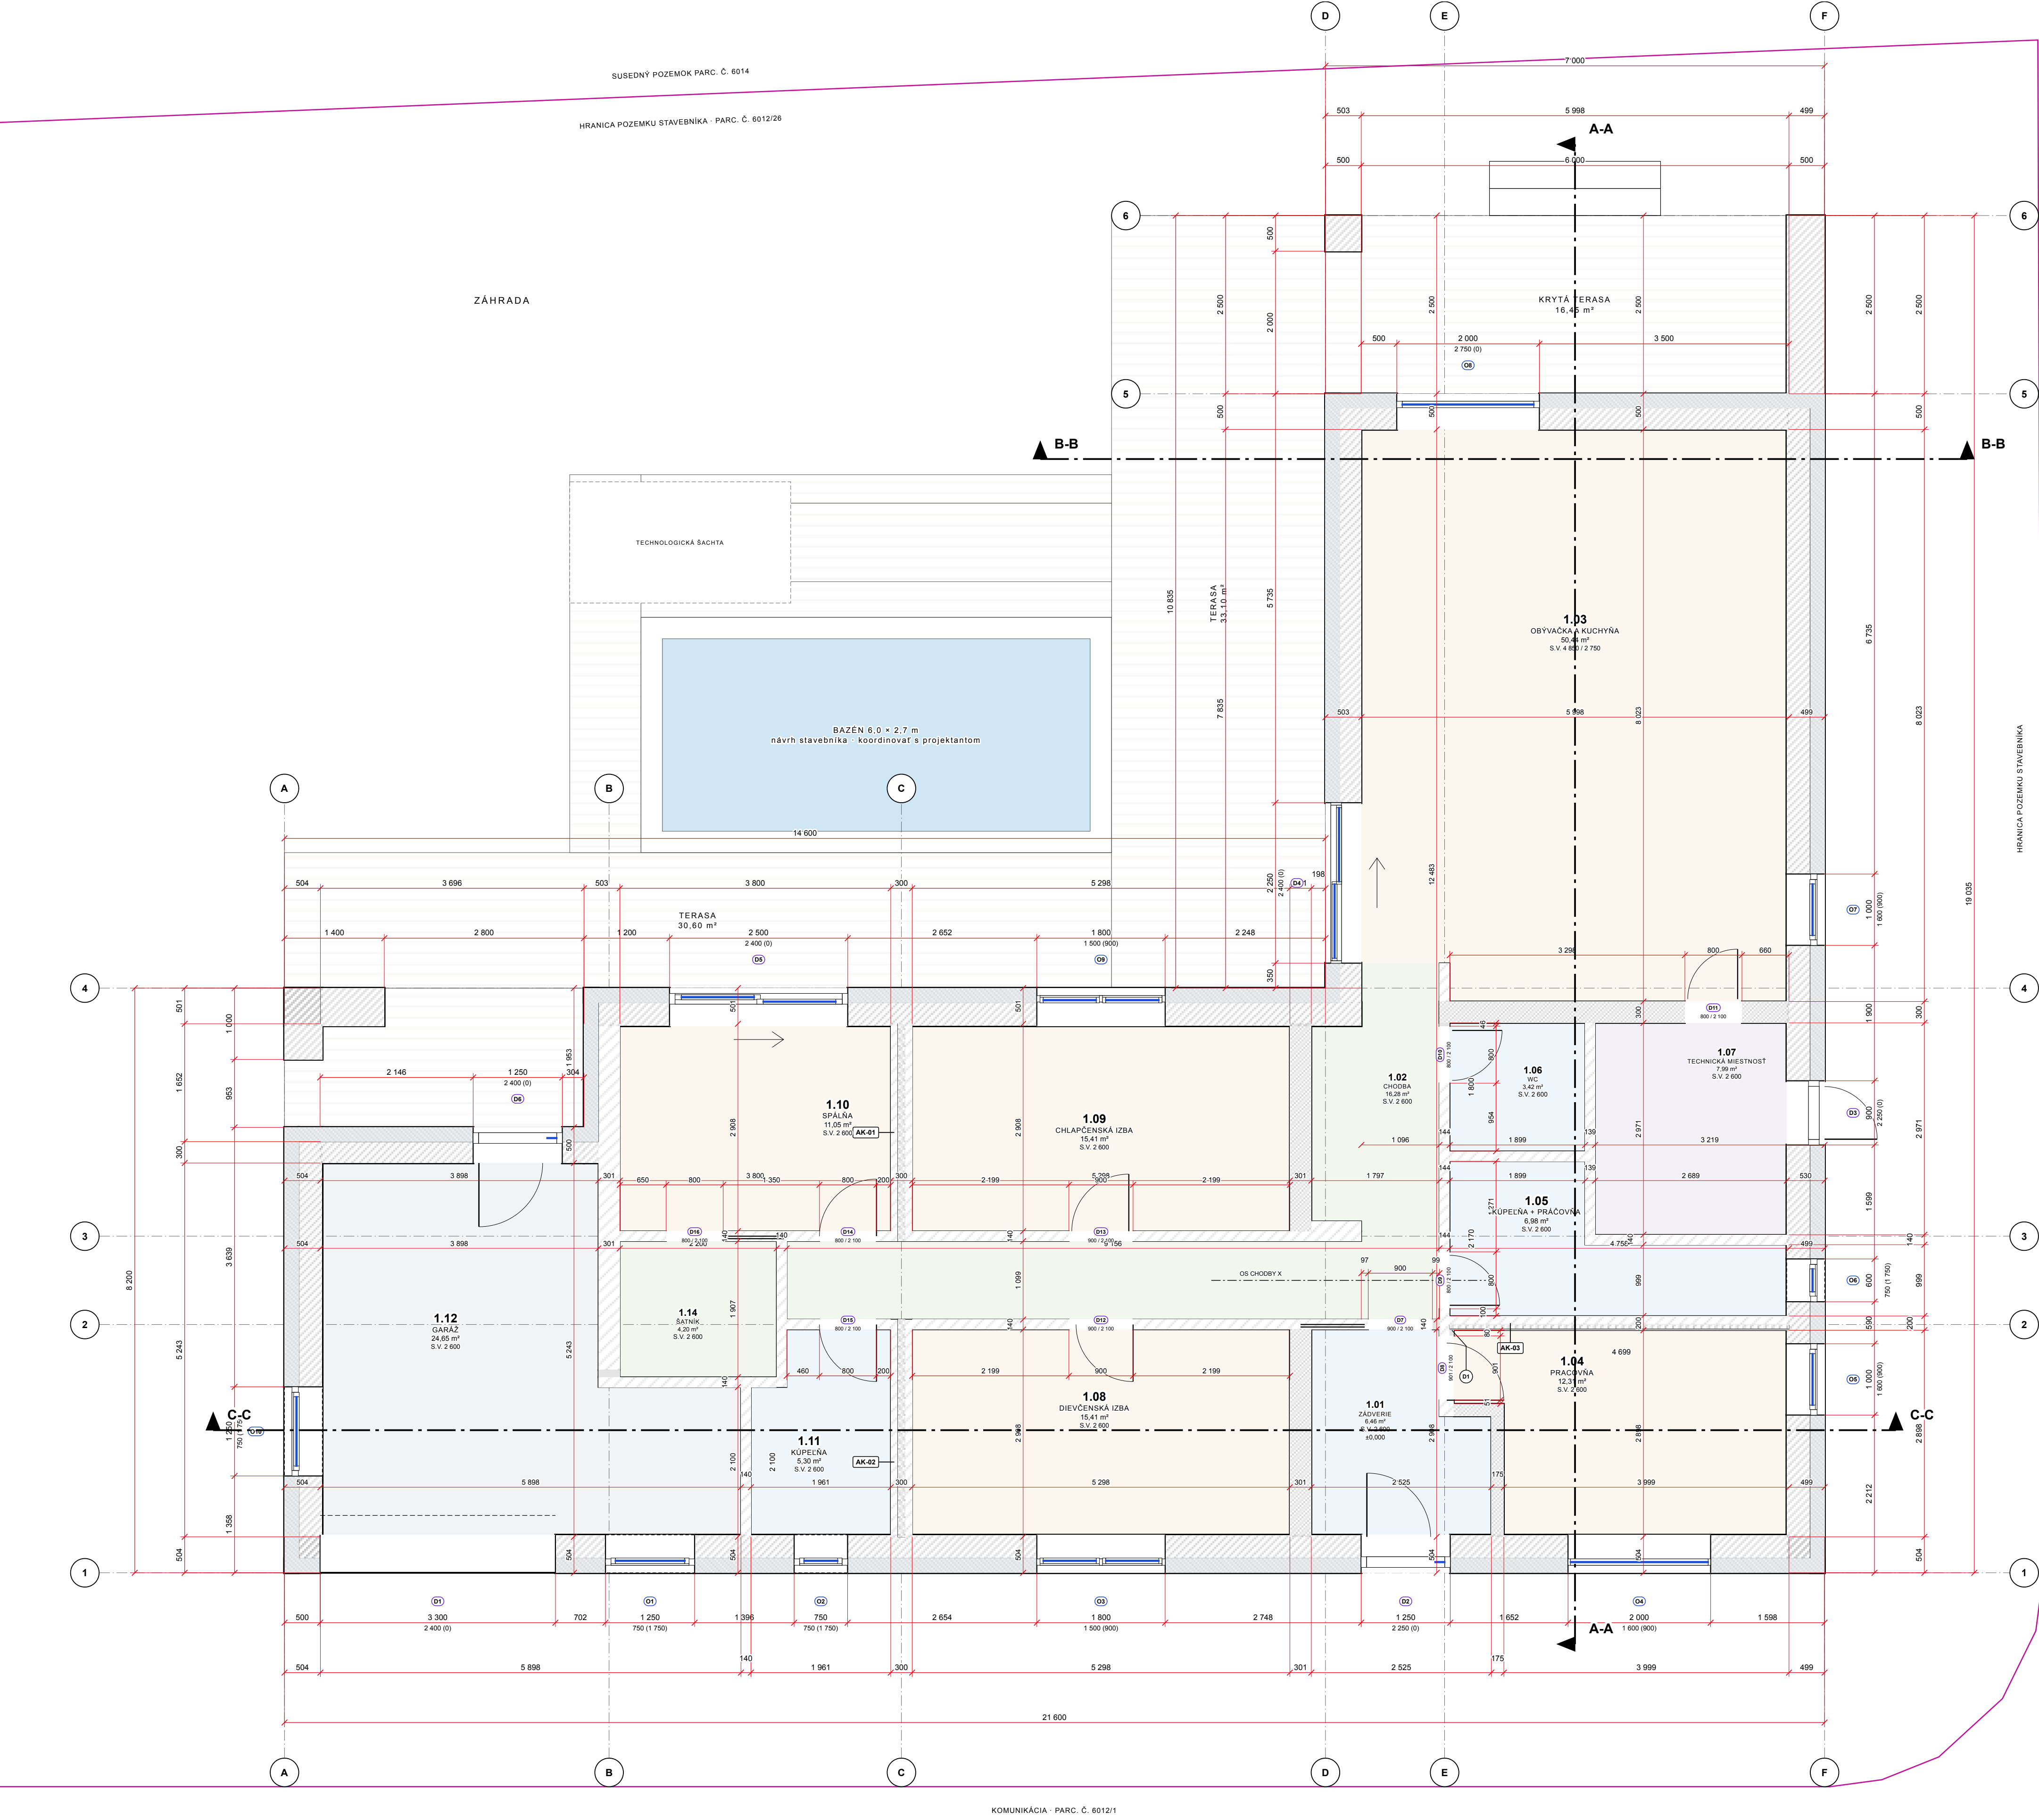

LEGENDA

KÓTY A OSI

Radý pri fasáde: 1. otvor – šírka nad čiarou, výška (parapet) pod čiarou - 2. líce priľahlých stien - 3. celkový rozmer

Refazce cez miestnosti: svetlé šírky a hrúbky stien za sebou - červené čísla pri stenách = svetlé rozmery miestnosti

Poloha dverí: odstupy stavebného otvoru od stien miestnosti, do ktorej sa krídlo otvára

Modulové osi: písmená A–F po šírke (→), čísla 1–6 po hĺbke (↑); C–D / 1–2 = pole medzi osami – jednoznačná poloha aj v čiernobielej tlači

Kóty v mm podľa 3D modelu, spravidla bez omietok a obkladov: AK-03 / H200: 200 mm vrátane 2 × 15 mm

PŮVODNÉ ±0,000 TOHTO LISTU = M0 PODLAHY; R0 ULICE = 184,200 m; ROZDIEL ΔFFL ZATIAŤ NEURČENÝ.

DOPLNENÉ STOPY A-A, B-B, C-C - geometria a kódy bez zmeny - nové konštrukcie NEVYDANÉ NA REALIZÁCIU

OTVORY

Okno alebo pevné presklenie - rozmery v tabuľke otvorov

otvorená brána, posuvná stena - otvok = otváranie krídla, šípka = posun

oskosenie v otvore - čiarkovaný obrys = parapet nad 1 500 mm

900 / 2 100 vnútorné dvere: šírka / výška stavebného otvoru, písané na strane, kam sa krídlo neotvára

Šírky a výšky sú stavebné otvory (bez rámov). Parapet a nadpražie od čistej podlahy ±0,000 = podlažia 1. NP.

MIESTNOSTI

1.03 chodba - číslo - účel - plocha čistej podlahy - S.V. = svetlá výška

Obytné miestnosti

Hygienické zázemie

Komunikácie a šatník

Technická miestnosť

Garáž

drevená terasa 1.13 (80,15 m²) - bazén a šachtá = návrh stavebníka, nie je súčasťou D1

POZNÁMKY

Výkres je exportom aktívneho 3D modelu variantu C (revízia C-2026-09-07) v konvenciách D1.1.002. Obvodová stena 500 mm, líce podtlah v modeli 499-504 mm od vonkajšieho líca. Nejde o geometrické zameranie; statiku, TZB, komín a požiarne riešenie potvrdí projektant.

LEGENDA MIESTNOSTÍ 1. NP

OZN.	ÚČEL MIESTNOSTI	PLOCHA m²	S.V. mm	PODLAHA	STENY	STROP	OSI
1.01	ZÁDVERIE	6.46	2 600	KERAMICKÁ DLAŽBA	VÁPENOCEM. OMÍETKA	SDK PODHEAD	D-E / 1-2
1.02	CHODBA	16.28	2 600	VINYL	VÁPENOCEM. OMÍETKA	SDK PODHEAD	C-D / 3-4
1.03	OBYVACIA A KUCHYŇA	50.44	4 850 / 2 750	VINYL	VÁPENOCEM. OMÍETKA	SDK PODHEAD - ŠIKMÝ	E-F / 4-5
1.04	PRACOVŇA	12.31	2 600	VINYL	VÁPENOCEM. OMÍETKA	SDK PODHEAD	E-F / 1-2
1.05	KUPEĽNA + PRACOVŇA	6.98	2 600	KERAMICKÁ DLAŽBA	KER. OBKLAD v. 2 100	SDK PODHEAD - VĽHKÉ PR.	E-F / 3
1.06	WC	3.42	2 600	KERAMICKÁ DLAŽBA	KER. OBKLAD v. 2 100	SDK PODHEAD - VĽHKÉ PR.	E-F / 3-4
1.07	TECHNICKÁ MIESTNOSŤ	7.99	2 600	EPOXIDOVÁ STIERKA	KER. OBKLAD v. 2 100	SDK PODHEAD - VĽHKÉ PR.	E-F / 3-4
1.08	DIEVČENSKÁ IZBA	15.41	2 600	VINYL	VÁPENOCEM. OMÍETKA	SDK PODHEAD	C-D / 1-2
1.09	CHLAPEČSKÁ IZBA	15.41	2 600	VINYL	VÁPENOCEM. OMÍETKA	SDK PODHEAD	C-D / 3-4
1.10	SPÁLŇA	11.05	2 600	VINYL	VÁPENOCEM. OMÍETKA	SDK PODHEAD	B-C / 3-4
1.11	KUPEĽNA	5.30	2 600	KERAMICKÁ DLAŽBA	KER. OBKLAD v. 2 100	SDK PODHEAD - VĽHKÉ PR.	B-C / 1-2
1.12	GARAŽ	24.65	2 600	EPOXIDOVÁ STIERKA	VÁPENOCEM. OMÍETKA	SDK PODHEAD	A-B / 1-2
1.14	ŠATNÍK	4.20	2 600	VINYL	VÁPENOCEM. OMÍETKA	SDK PODHEAD	B-C / 2
1.13	TERASA (3 ČASTI)	80.15	—	DREVENÁ TERASOVÁ PODLAHA	—	—	A-D / 4-6
2.	ČISTÁ PODLAHA 13 MIESTNOSTÍ	179.87	—	—	—	—	—

LEGENDA MATERIÁLOV

SO30, SO50 - Nosné obvodové múrivo z keramických tvaroviek hr. 300 mm, na systémovú murovaciu maltu; obvodová stena celkom 500 mm. Murované piliere a voľné úseky stien na terasách a v lodži (SO50) sú plné múrivo hr. 500 mm bez zateplenia

T120 - Kontaktný zatepľovací systém (ETICS) z minerálnej vlny hr. 200 mm na vonkajšom líci obvodového múriva, s tenkovrstvovou omietkou

SN30, SN20 - Nosné vnútorné múrivo z keramických tvaroviek hr. 300 / 200 mm, na systémovú murovaciu maltu

SP30, SP20, SP14 - Nenosné priečkové múrivo z keramických tvaroviek hr. 300 / 200 / 140 mm, na systémovú murovaciu maltu (vrátane puzdra posuvných dverí)

SP10, SP6 - Sadrokartónové systémové priečky a predsteny hr. 100 / 60 mm, napr. Rigips W112, s výplňou z minerálnej vlny

SA30 - AK-01 spáľňa / chlapčenská izba; AK-02 kúpeľňa / dievčenská izba. LeierPLAN 10 P10 100 + minerálna vata 100 + LeierPLAN 10 P10 100 mm. Celkom 300 mm bez omietok a obkladov. Statika a akustické napojenie na posúdenie; Rw zostavý nedoložené.

H200 - AK-03 pracovňa / sprcha. Od sprchy: VC omietka 15 + LeierPLAN 10 100 + omietka 15 + dutina W623 45 (pružné závesy, vata 40) + 2 × 12.5 Silentboard = 200 mm; finálne povrchy navyše. Požiadavka Rw ≥ 51 dB; predbežný výpočet = 58 dB, presnú zostavu a napojenia potvrdí.

ZÁKLADNÉ ÚDAJE

ÚDAJ	HODNOTA
Pódorys	L - hlavné krídlo ulica-záhrada + krídlo s krytou terasou
Vonkajšie rozmery	21 600 × 19 035 mm - hlavné krídlo hĺbka 8 200 - krídlo šírka 7 000
Zastavaná plocha	262,97 m² po vonkajšie líce stien
Otvory v obvodě	10 okien a presklení - 6 dverí, brán a posuvných stien - 10 vnútorných dverí
Výšky	±0,000 = čistá podlažia 1. NP - S.V. 2 600 pod SDK podtlahom - obyvatka 2 750 pri stene, 4 850 pod hrebeňom

TABUĽKA OTVOROV

KÓD	OTVOR	TYP	MIEST.	ŠÍRKA	VÝŠKA	PARAPET	NADPR. / FASÁDA - OSI
D1	Sekčná garážová brána	sekčná brána	1.12	3 300	2 400	0	2 400 S - A-B
O1	Okno FRONT-02	okno	1.12	1 250	750	1 750	2 500 S - A-B
O2	Okno FRONT-03	okno	1.11	750	750	1 750	2 500 S - B-C
O3	Dvojkrižové okno oproti dverám	okno	1.08	1 800	1 500	900	2 400 S - C-D
D2	Hlavné vstupné dvere	dvere	1.01	1 250	2 250	0	2 250 S - D-E
O4	Okno FRONT-07	okno	1.04	2 000	1 600	900	2 500 S - E-F
O5	Bočné okno EAST-01	okno	1.04	1 000	1 600	900	2 500 E - E-F
O6	Bočné okno EAST-02	okno	1.05	600	750	1 750	2 500 E - E-F
D3	Dvere technickej miestnosti	dvere	1.07	900	2 250	0	2 250 E - E-F
O7	Bočné okno EAST-04	okno	1.03	1 000	1 600	900	2 500 E - E-F
O8	Pevné presklenie terasy	pevné presklenie	1.03	2 000	2 750	0	2 750 NN2 - E-F
D4	Terasové posuvné presklenie 2 250	posuvné presklenie	1.03	2 250	2 400	0	2 400 WW - E-F
O9	Dvojkrižové okno oproti dverám	okno	1.09	1 800	1 500	900	2 400 N - C-D
D5	Terasové presklenie 2500	posuvné presklenie	1.10	2 500	2 400	0	2 400 N - B-C
O10	Bočné garážové okno WEST-GARAGE-01	okno	1.12	1 250	750	1 750	2 500 W - A-B
D6	Garáž → krytý zárez	dvere	1.12	1 250	2 400	0	2 400 L - A-B
D7	Zádverie → centrálna chodba	posuvné dvere do puzdra	1.02	900	2 100	0	2 100 int. - C-D
D8	Zádverie → pracovňa	vnútorné dvere	1.04	901	2 100	0	2 100 int. - E-F
D9	Dvere chodba → kúpeľňa 1.05	vnútorné dvere	1.05	800	2 100	0	2 100 int. - E-F
D10	Dvere chodba → WC	vnútorné dvere	1.06	800	2 100	0	2 100 int. - E-F
D11	Dvere obytný priestor → technická miestnosť	vnútorné dvere	1.07	800	2 100	0	2 100 int. - E-F
D12	Chodba → detská izba do ulice	vnútorné dvere	1.08	900	2 100	0	2 100 int. - C-D
D13	Dvere chodba → izba 1.09	vnútorné dvere	1.09	900	2 100	0	2 100 int. - C-D
D14	Spáľňa za novou priečkou	vnútorné dvere	1.10	800	2 100	0	2 100 int. - B-C
D15	Otvorený vstup z chodby → kúpeľňa	vnútorné dvere	1.11	800	2 100	0	2 100 int. - B-C
D16	Spáľňa → šatník	posuvné dvere do puzdra	1.14	800	2 100	0	2 100 int. - B-C

012345m

1:50 (A1) 1:100 (A3)

↑

S

±0,000 = ČISTÁ PODLAHA 1. NP

STAVEBNÍK David Zita, Hana Ivčičová - Dmholet

PODKLAD D1.1.002 Pódorys 1. NP - DPSZ 04/2026 - Ing. arch. Jiří Bradáč, Ing. arch. Vladimír Muzkař

VYPRACOVANÉ Digitálne dvojča - export z aktívneho 3D modelu variantu C - revízia C-2026-09-07

PODKLAD PRE REALIZÁCIU - EXPORT Z DIGITÁLNEHO DVOJČATA

NÁZOV A Miesto stavby

NOVOSTAVBA RD BŘEZÍ U MIKULOVA

PARC. Č. 6012/26, K.Ú. BŘEZÍ U MIKULOVA, 691 81 BŘEZÍ U MIKULOVA

OBJEKT RD BŘEZÍ U MIKULOVA - VARIANT C

CAST D1.1 ARCHITECTONICKO-STAVEBNÉ ŘEŠENÍ

VÝKRES

FORMÁT A1 - 841 × 594 mm

DATUM 14. 08. 2026

STUPEŇ DT - L3

REVIZIA C-2026-09-07

MIERKA 1: 50

VERZIA F - TB - 15 kW + 800 l

ČÍSLO PRÍLOHY

C-L3