


Južná (uličná) fasáda

ROVINA Y = 3 000 mm · čítanie rastúcich súradníc X

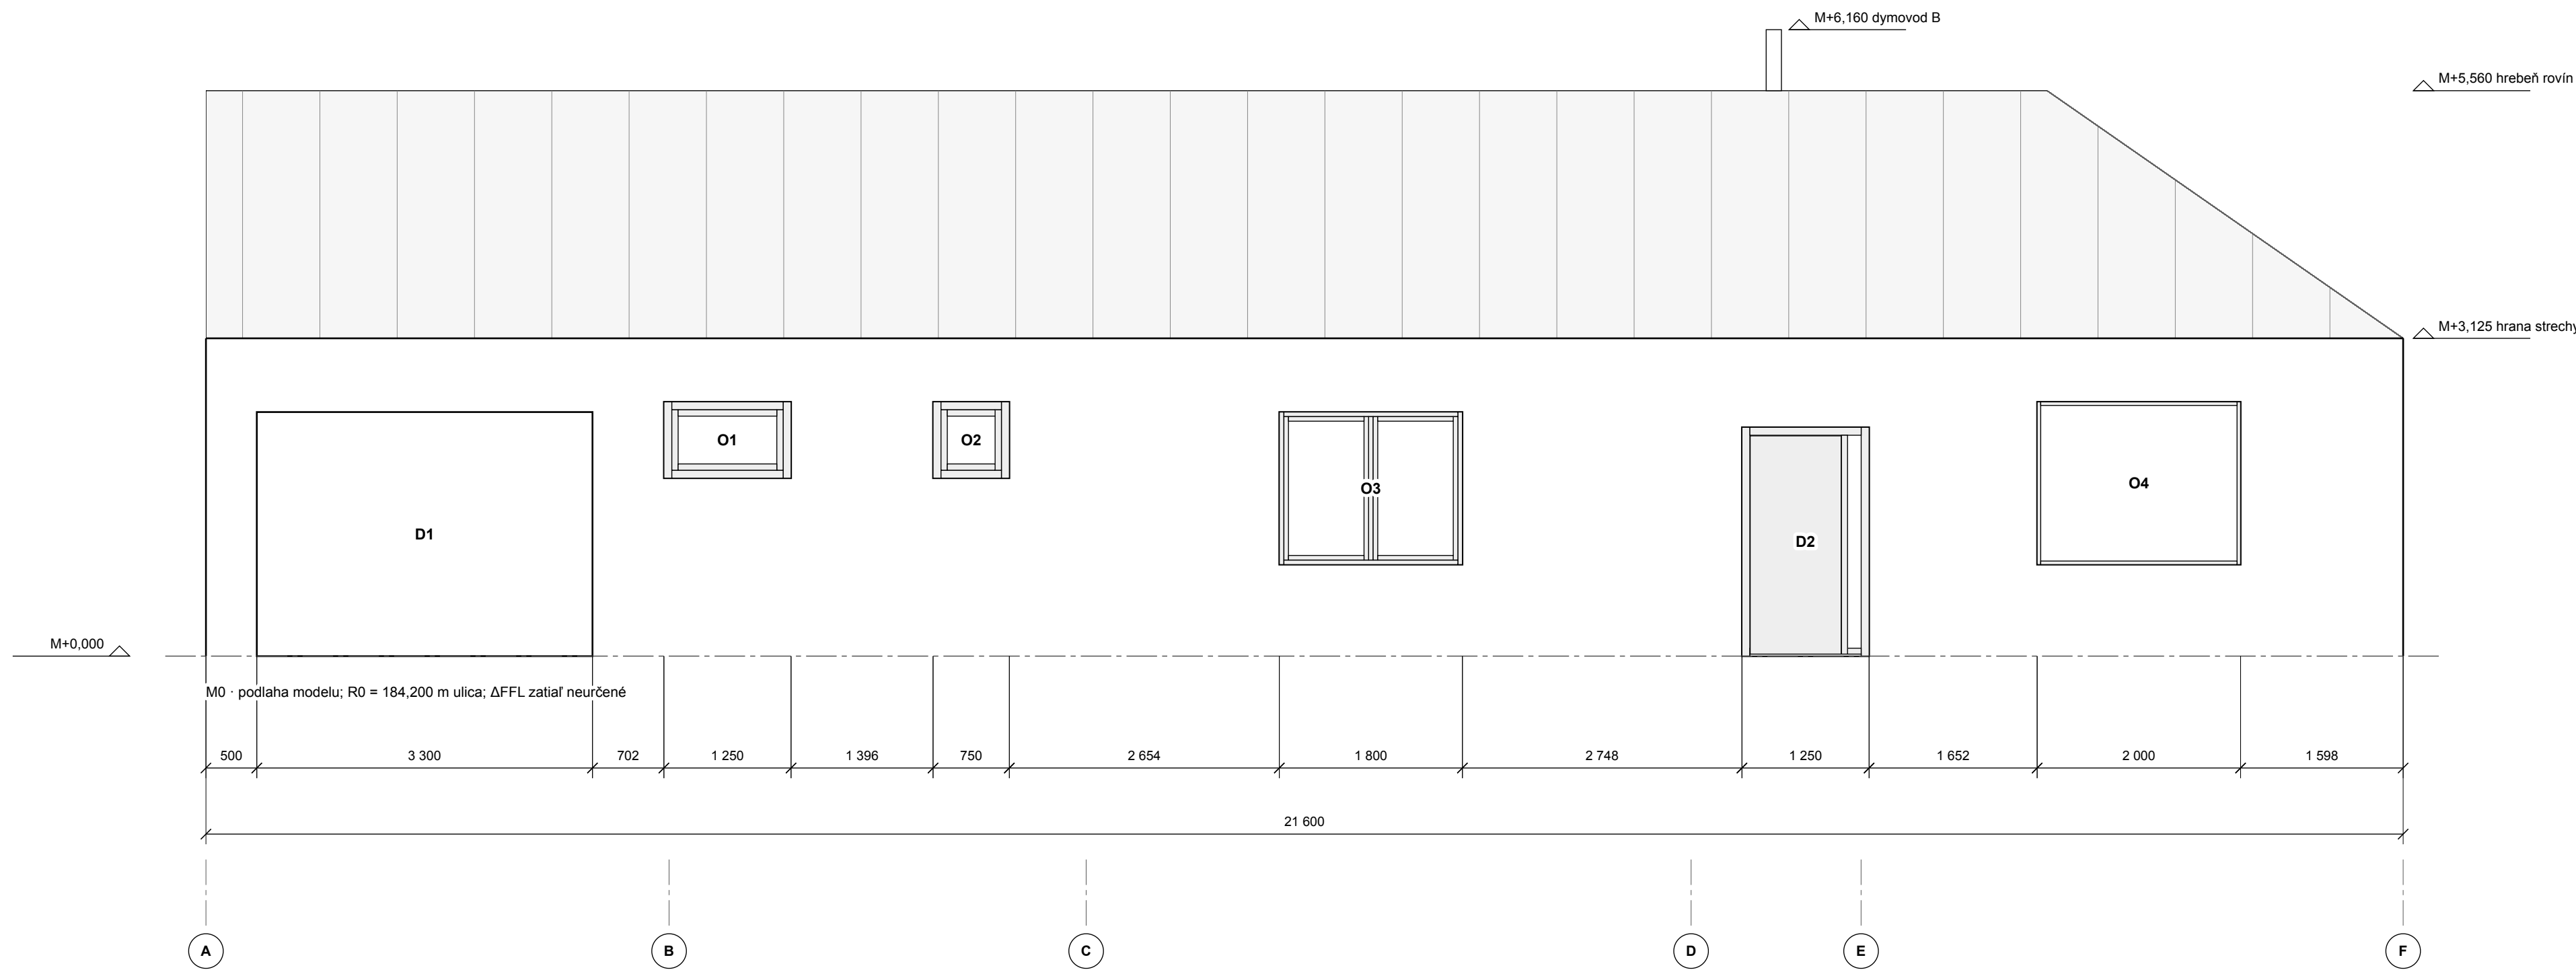

VYTYČOVACIE ÚDAJE OTVOROV TEJTO ROVINY

Kód / identifikátor	Od / do [mm]	Š × V [mm]	Parapet / nadpražie
D1 / GARAGE-DOOR	X 6 940 / 10 240	3 300 × 2 400	0 / 2 400
O1 / Výplň otvoru FRONT-02	X 10 942 / 12 192	1 250 × 750	1 750 / 2 500
O2 / Výplň otvoru FRONT-03	X 13 588 / 14 338	750 × 750	1 750 / 2 500
O3 / Výplň otvoru FRONT-05	X 16 992 / 18 792	1 800 × 1 500	900 / 2 400
D2 / Výplň otvoru FRONT-ENTRY	X 21 540 / 22 790	1 250 × 2 250	0 / 2 250
O4 / Výplň otvoru FRONT-07	X 24 442 / 26 442	2 000 × 1 600	900 / 2 500

ZNAČKY A MATERIÁLY

-  Murivo / keramické prvky
-  ETICS / minerálna vlna
-  Betón – len ak je určený návrhom
-  Drevený obklad

Čiarkovane: prerušené / neurčené konštrukcie.

M = výška k podlahe modelu. Dĺžky v mm.

K ulici RO: z = M + ΔFFL. ΔFFL neurčené.

Obvodový plášť SO30 + TI20: nosné murivo 300 mm a ETICS 200 mm. Voľné piliere SO50: 500 mm plné murivo. Skladby a detaily DT/SK.

KONTROLA TLAČE 100 % - 1 000 mm ≈ 20 mm na papieri

1 : 50 - vypnúť „prispôbiť strane“

NOVOSTAVBA RD BŘEZÍ U MIKULOVA

PARCELA 6012/26 · HLAVNÝ NÁVRH C / B / B

Južná (uličná) fasáda

R0 = 184,200 m · M0 = PODLAHA MODELU · ΔFFL = M0 – R0 ZATIAĽ NEURČENÉ

Presná modelová projekcia. R05/R06: chýba skutočný terén, sokel, finálne povrchy a realizačné detaily. Rozmery otvorov sú modelové stavebné otvory; výrobný rozmer určí dodávateľ.

STAV

NEVYDANÉ NA REALIZÁCIU

Chýbajúci návrh sa nesmie nahradiť mierkou výkresu.

VYPRACOVAL: digitálne dvojča · bez autorizačnej pečiatky

DÁTUM 2026-09-14 FORMÁT A1 841 × 594 mm MIERKA 1 : 50

ZDROJ 6cd4bc82841b · úplné odtlačky v model-snapshot.json