


Záhradná (severná) fasáda

ROVINA Y = 11 200 mm - čítanie klesajúcich súradníc X

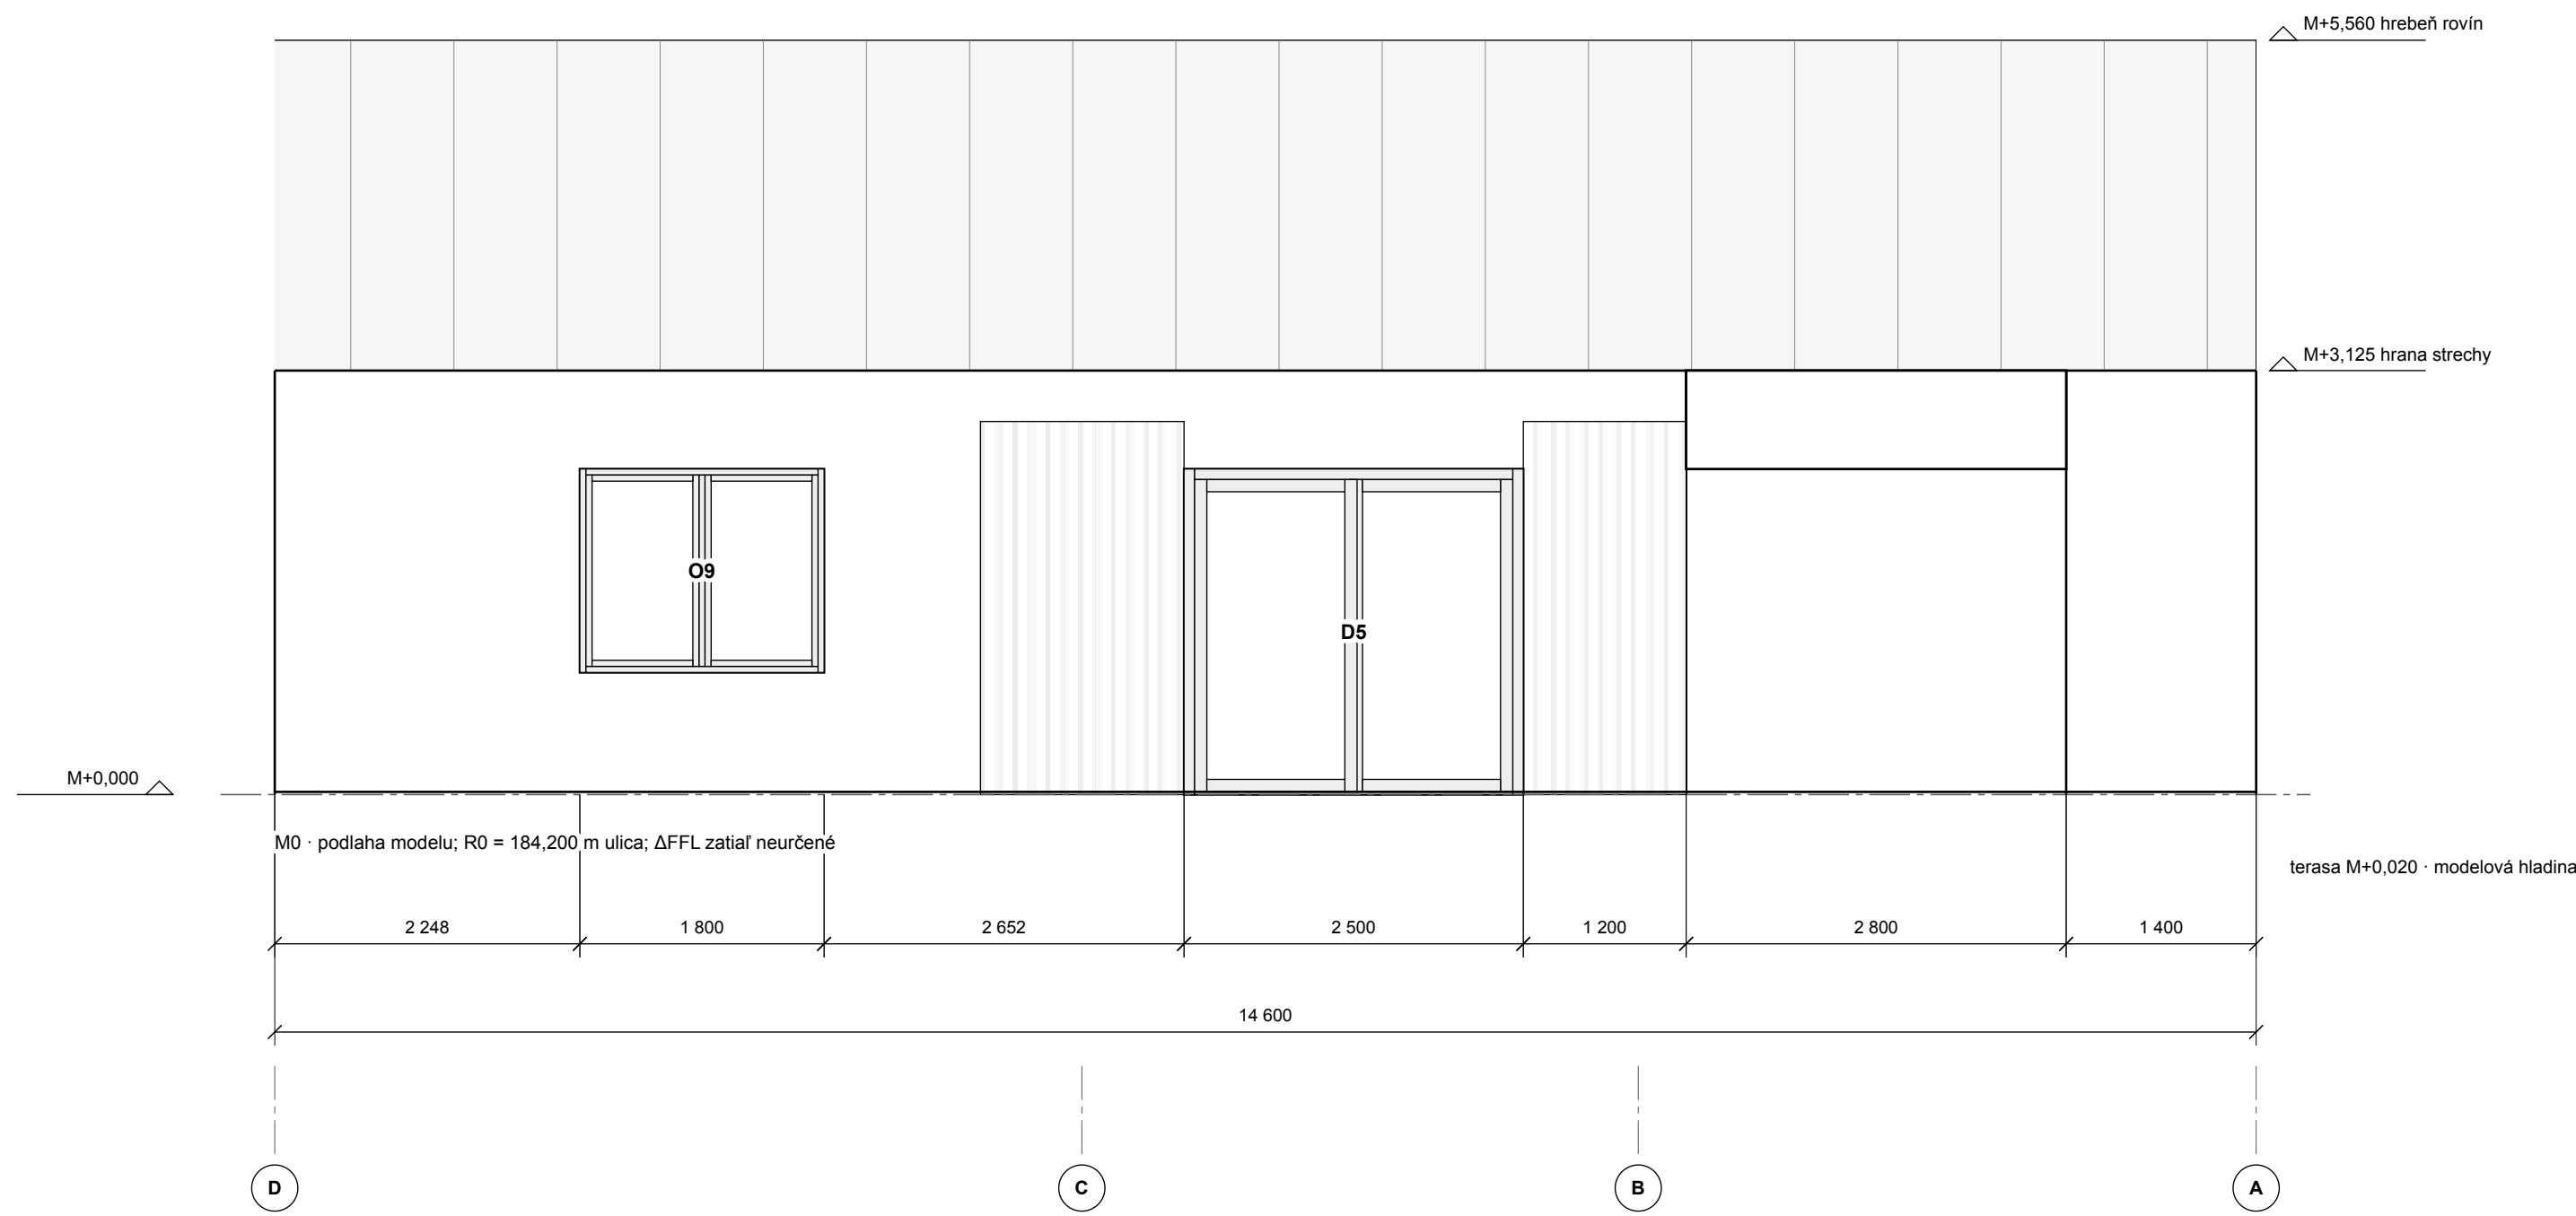

VYTYČOVACIE ÚDAJE OTVOROV TEJTO ROVINY

Kód / identifikátor	Od / do [mm]	Š × V [mm]	Parapet / nadpražie
O9 / Vypĺň otvoru GARDEN-03	X 16 992 / 16 792	1 800 × 1 500	900 / 2 400
D5 / Terasové presklenie 2500	X 11 840 / 14 340	2 500 × 2 400	0 / 2 400

ZNAČKY A MATERIÁLY

- Murivo / keramické prvky
ETICS / minerálna vlna
Betón – len ak je určený návrhom
Drevený obklad

Čiarkovane: prerušené / neurčené konštrukcie.

M = výška k podlahe modelu. Dĺžky v mm.

K ulici RO: z = M + ΔFFL. ΔFFL neurčené.

Obvodový plášť SO30 + TI20: nosné murivo 300 mm a ETICS 200 mm. Voľné piliere SO50: 500 mm plné murivo. Skladby a detaily DT/SK.

KONTROLA TLAČE 100 % - 1 000 mm ≈ 20 mm na papieri

1 : 50 - vypnúť „prispôbiť strane“

NOVOSTAVBA RD BŘEZÍ U MIKULOVA

PARCELA 6012/26 - HLAVNÝ NÁVRH C / B / B

Záhradná (severná) fasáda

R0 = 184,200 m - M0 = PODLAHA MODELU - ΔFFL = M0 - R0 ZATIAĽ NEURČENÉ

Presná modelová projekcia. R05/R06: chýba skutočný terén, sokel, finálne povrchy a realizačné detaily. Rozmery otvorov sú modelové stavebné otvory; výrobný rozmer určí dodávateľ.

STAV

NEVYDANÉ NA REALIZÁCIU

Chýbajúci návrh sa nesmie nahradiť mierkou výkresu.

VYPRACOVAL: digitálne dvojča - bez autorizačnej pečiatky

DÁTUM 2026-09-14 FORMÁT A1 841 × 594 mm MIERKA 1 : 50

ZDROJ 6cd4bc82841b - úplné odtlačky v model-snapshot.json