


Západný štít garáže

ROVINA X = 6 440 mm · čítanie klesajúcich súradníc Y

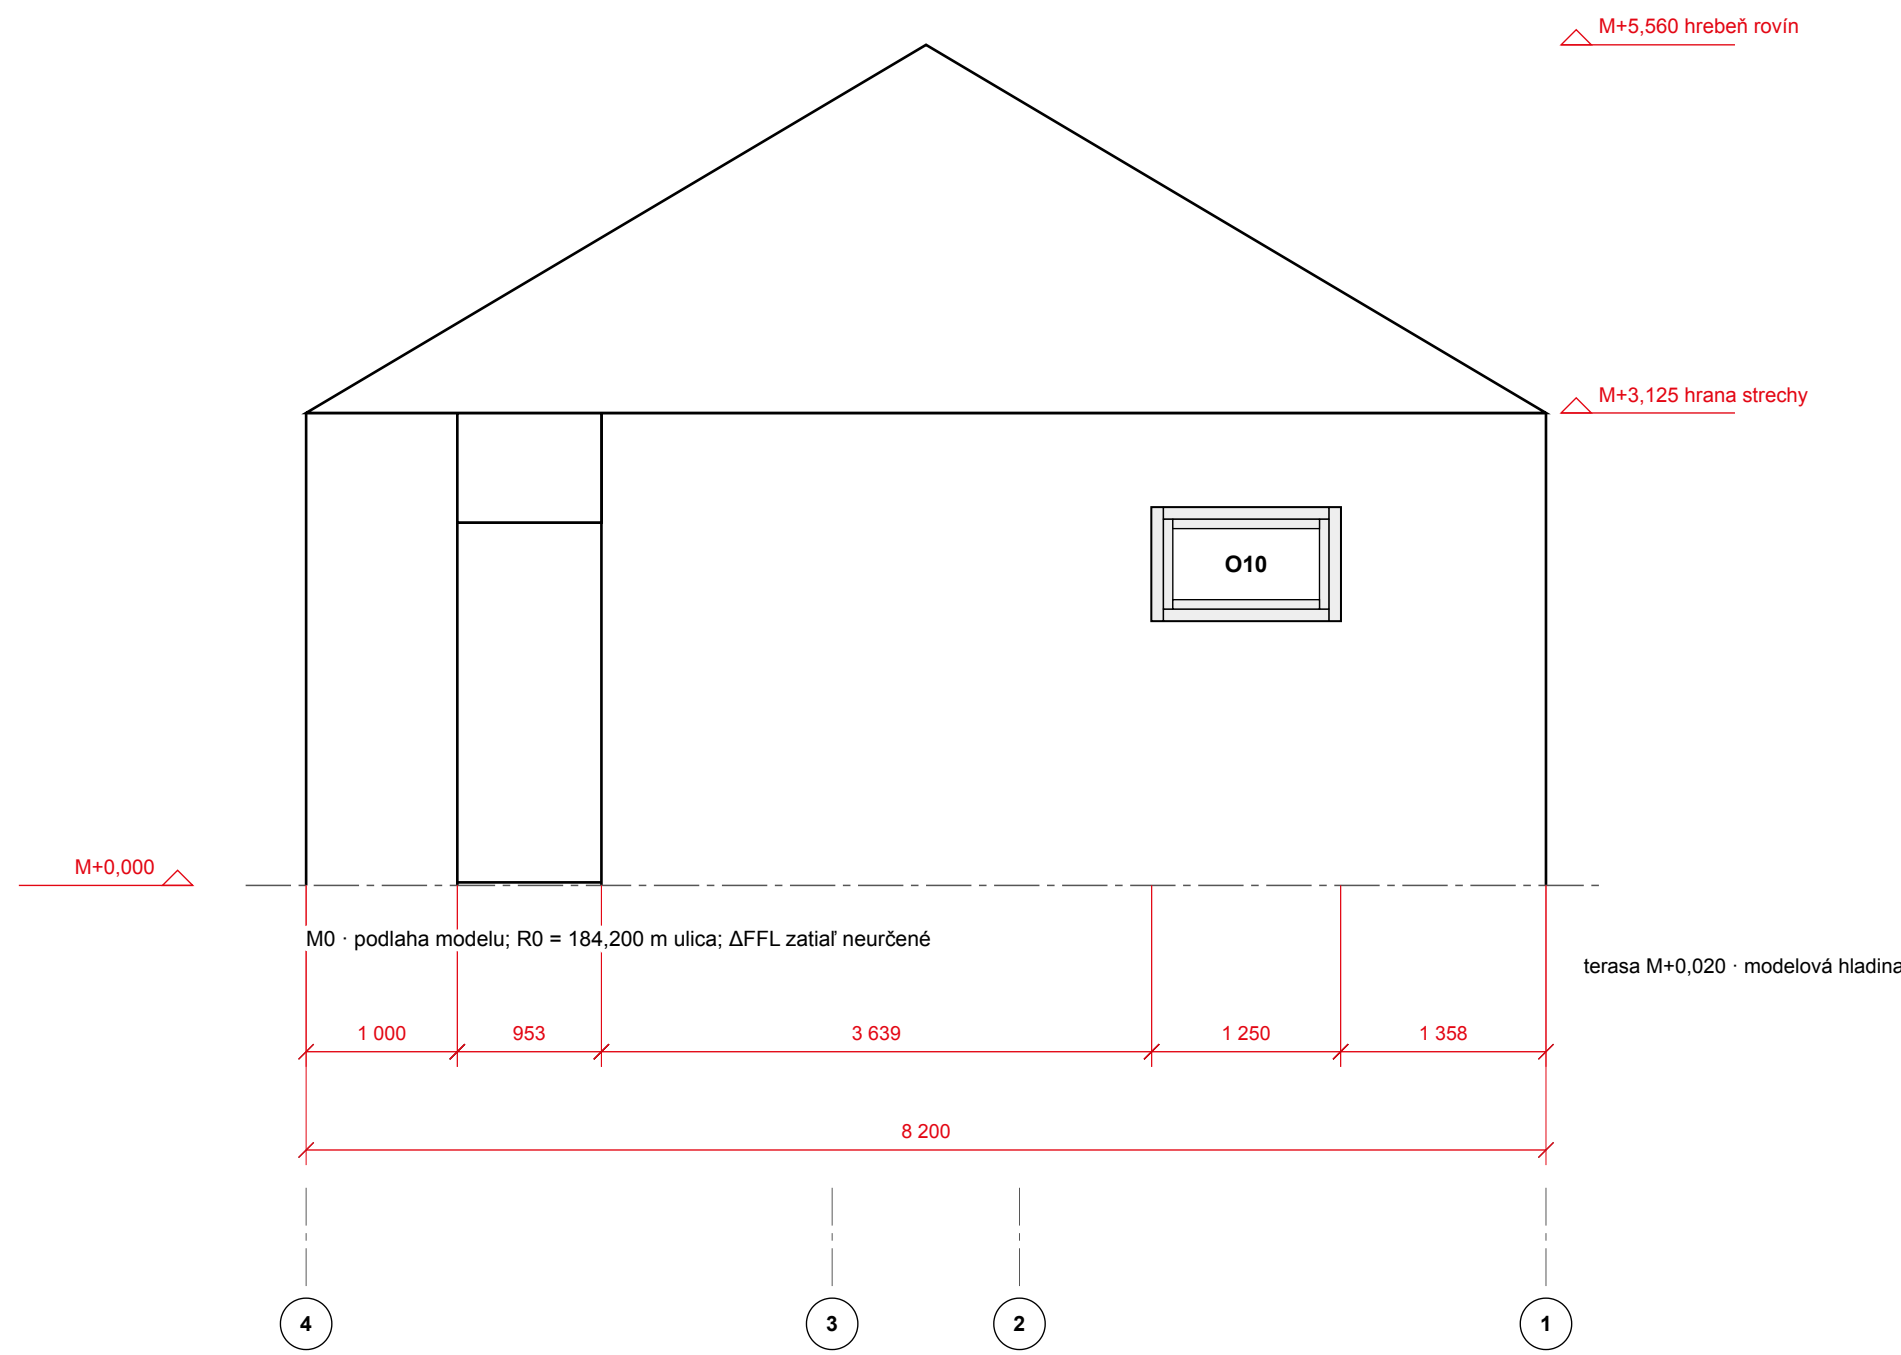

VYTYČOVACIE ÚDAJE OTVOROV TEJTO ROVINY

Kód / identifikátor	Od / do [mm]	Š × V [mm]	Parapet / nadpražie
O10 / Bočné garážové okno WEST-GARAGE-01	Y 4 358 / 5 608	1 250 × 750	1 750 / 2 500

ZNAČKY A MATERIÁLY

- Murivo / keramické prvky
■ ETICS / minerálna vlna
■ Betón – len ak je určený návrhom
■ Drevený obklad

Čiarkovane: prerušené / neurčené konštrukcie.

M = výška k podlahe modelu. Dĺžky v mm.

K ulici R0: z = M + ΔFFL. ΔFFL neurčené.

Obvodový plášť SO30 + TI20: nosné murivo 300 mm a ETICS 200 mm. Voľné piliere SO50: 500 mm plné murivo. Skladby a detaily DT/SK.

KONTROLA TLAČE 100 % - 1 000 mm ≈ 20 mm na papieri

1 : 50 - vypnúť „prispôbiť strane“

NOVOSTAVBA RD BŘEZÍ U MIKULOVA

PARCELA 6012/26 · HLAVNÝ NÁVRH C / B / B

Západný štít garáže

R0 = 184,200 m · M0 = PODLAHA MODELU · ΔFFL = M0 – R0 ZATIAĽ NEURČENÉ

Presná modelová projekcia. R05/R06: chýba skutočný terén, sokel, finálne povrchy a realizačné detaily. Rozmery otvorov sú modelové stavebné otvory; výrobný rozmer určí dodávateľ.

STAV

NEVYDANÉ NA REALIZÁCIU

Chýbajúci návrh sa nesmie nahradiť mierkou výkresu.

VYPRACOVAL: digitálne dvojča · bez autorizačnej pečiatky

DÁTUM 2026-09-14 FORMÁT A1 841 × 594 mm MIERKA 1 : 50

ZDROJ 6cd4bc82841b · úplné odtlačky v model-snapshot.json