



Lodžia · zadná stena garáže

ROVINA Y = 9 247 mm · čítanie klesajúcich súradníc X

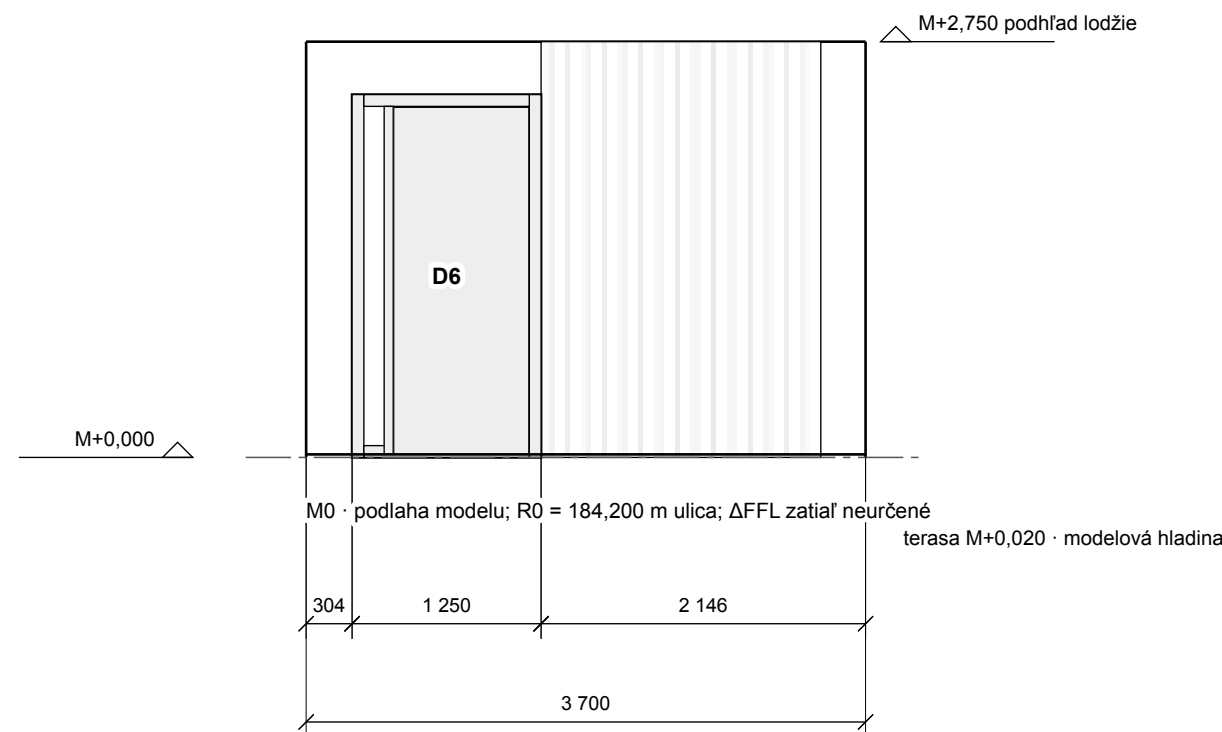

BOČNÉ LÍCE LODŽIE

X 10 640 · Y 9 247–11 200

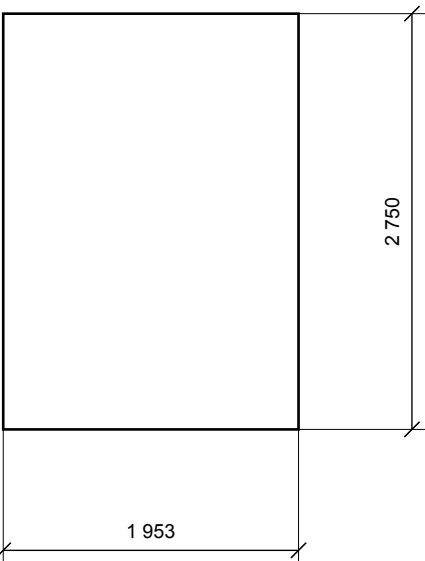

VYTYČOVACIE ÚDAJE OTVOROV TEJTO ROVINY

Kód / identifikátor	Od / do [mm]	Š × V [mm]	Parapet / nadpražie
D6 / LOGGIA-DOOR	X 9 086 / 10 336	1 250 × 2 400	0 / 2 400

ZNAČKY A MATERIÁLY

- Murivo / keramické prvky
- ETICS / minerálna vlna
- Betón – len ak je určený návrhom
- Drevený obklad

Čiarkovane: prerušené / neurčené konštrukcie.

M = výška k podlahe modelu. Dĺžky v mm.

K ulici R0: z = M + ΔFFL. ΔFFL neurčené.

Obvodový plášť SO30 + TI20: nosné murivo 300 mm a ETICS 200 mm. Voľné piliere SO50: 500 mm plné murivo. Skladby a detaily DT/SK.

Bočná stena lodžie: X 10 640, Y 9 247–11 200; bez otvorov.

KONTROLA TLAČE 100 % - 1 000 mm ≈ 20 mm na papieri

1 : 50 - vypnúť „prispôbiť strane“

NOVOSTAVBA RD BŘEZÍ U MIKULOVA

PARCELA 6012/26 · HLAVNÝ NÁVRH C / B / B

Lodžia · zadná stena garáže

R0 = 184,200 m · M0 = PODLAHA MODELU · ΔFFL = M0 – R0 ZATIAĽ NEURČENÉ

Presná modelová projekcia. R05/R06: chýba skutočný terén, sokel, finálne povrchy a realizačné detaily. Rozmery otvorov sú modelové stavebné otvory; výrobný rozmer určí dodávateľ.

STAV

NEVYDANÉ NA REALIZÁCIU

Chýbajúci návrh sa nesmie nahradiť mierkou výkresu.

VYPRACOVAL: digitálne dvojča · bez autorizačnej pečiatky

DÁTUM 2026-09-14 FORMÁT A1 841 × 594 mm MIERKA 1 : 50

ZDROJ 6cd4bc82841b · úplné odtlačky v model-snapshot.json