


B-B · Pričný rez katedrálovým stropom

Y = 18 620 mm : stopa na D1.1.002-C-RE · Obývačka 1.03, skutočný profil podhľadu, dymovod B a celá západná terasa.

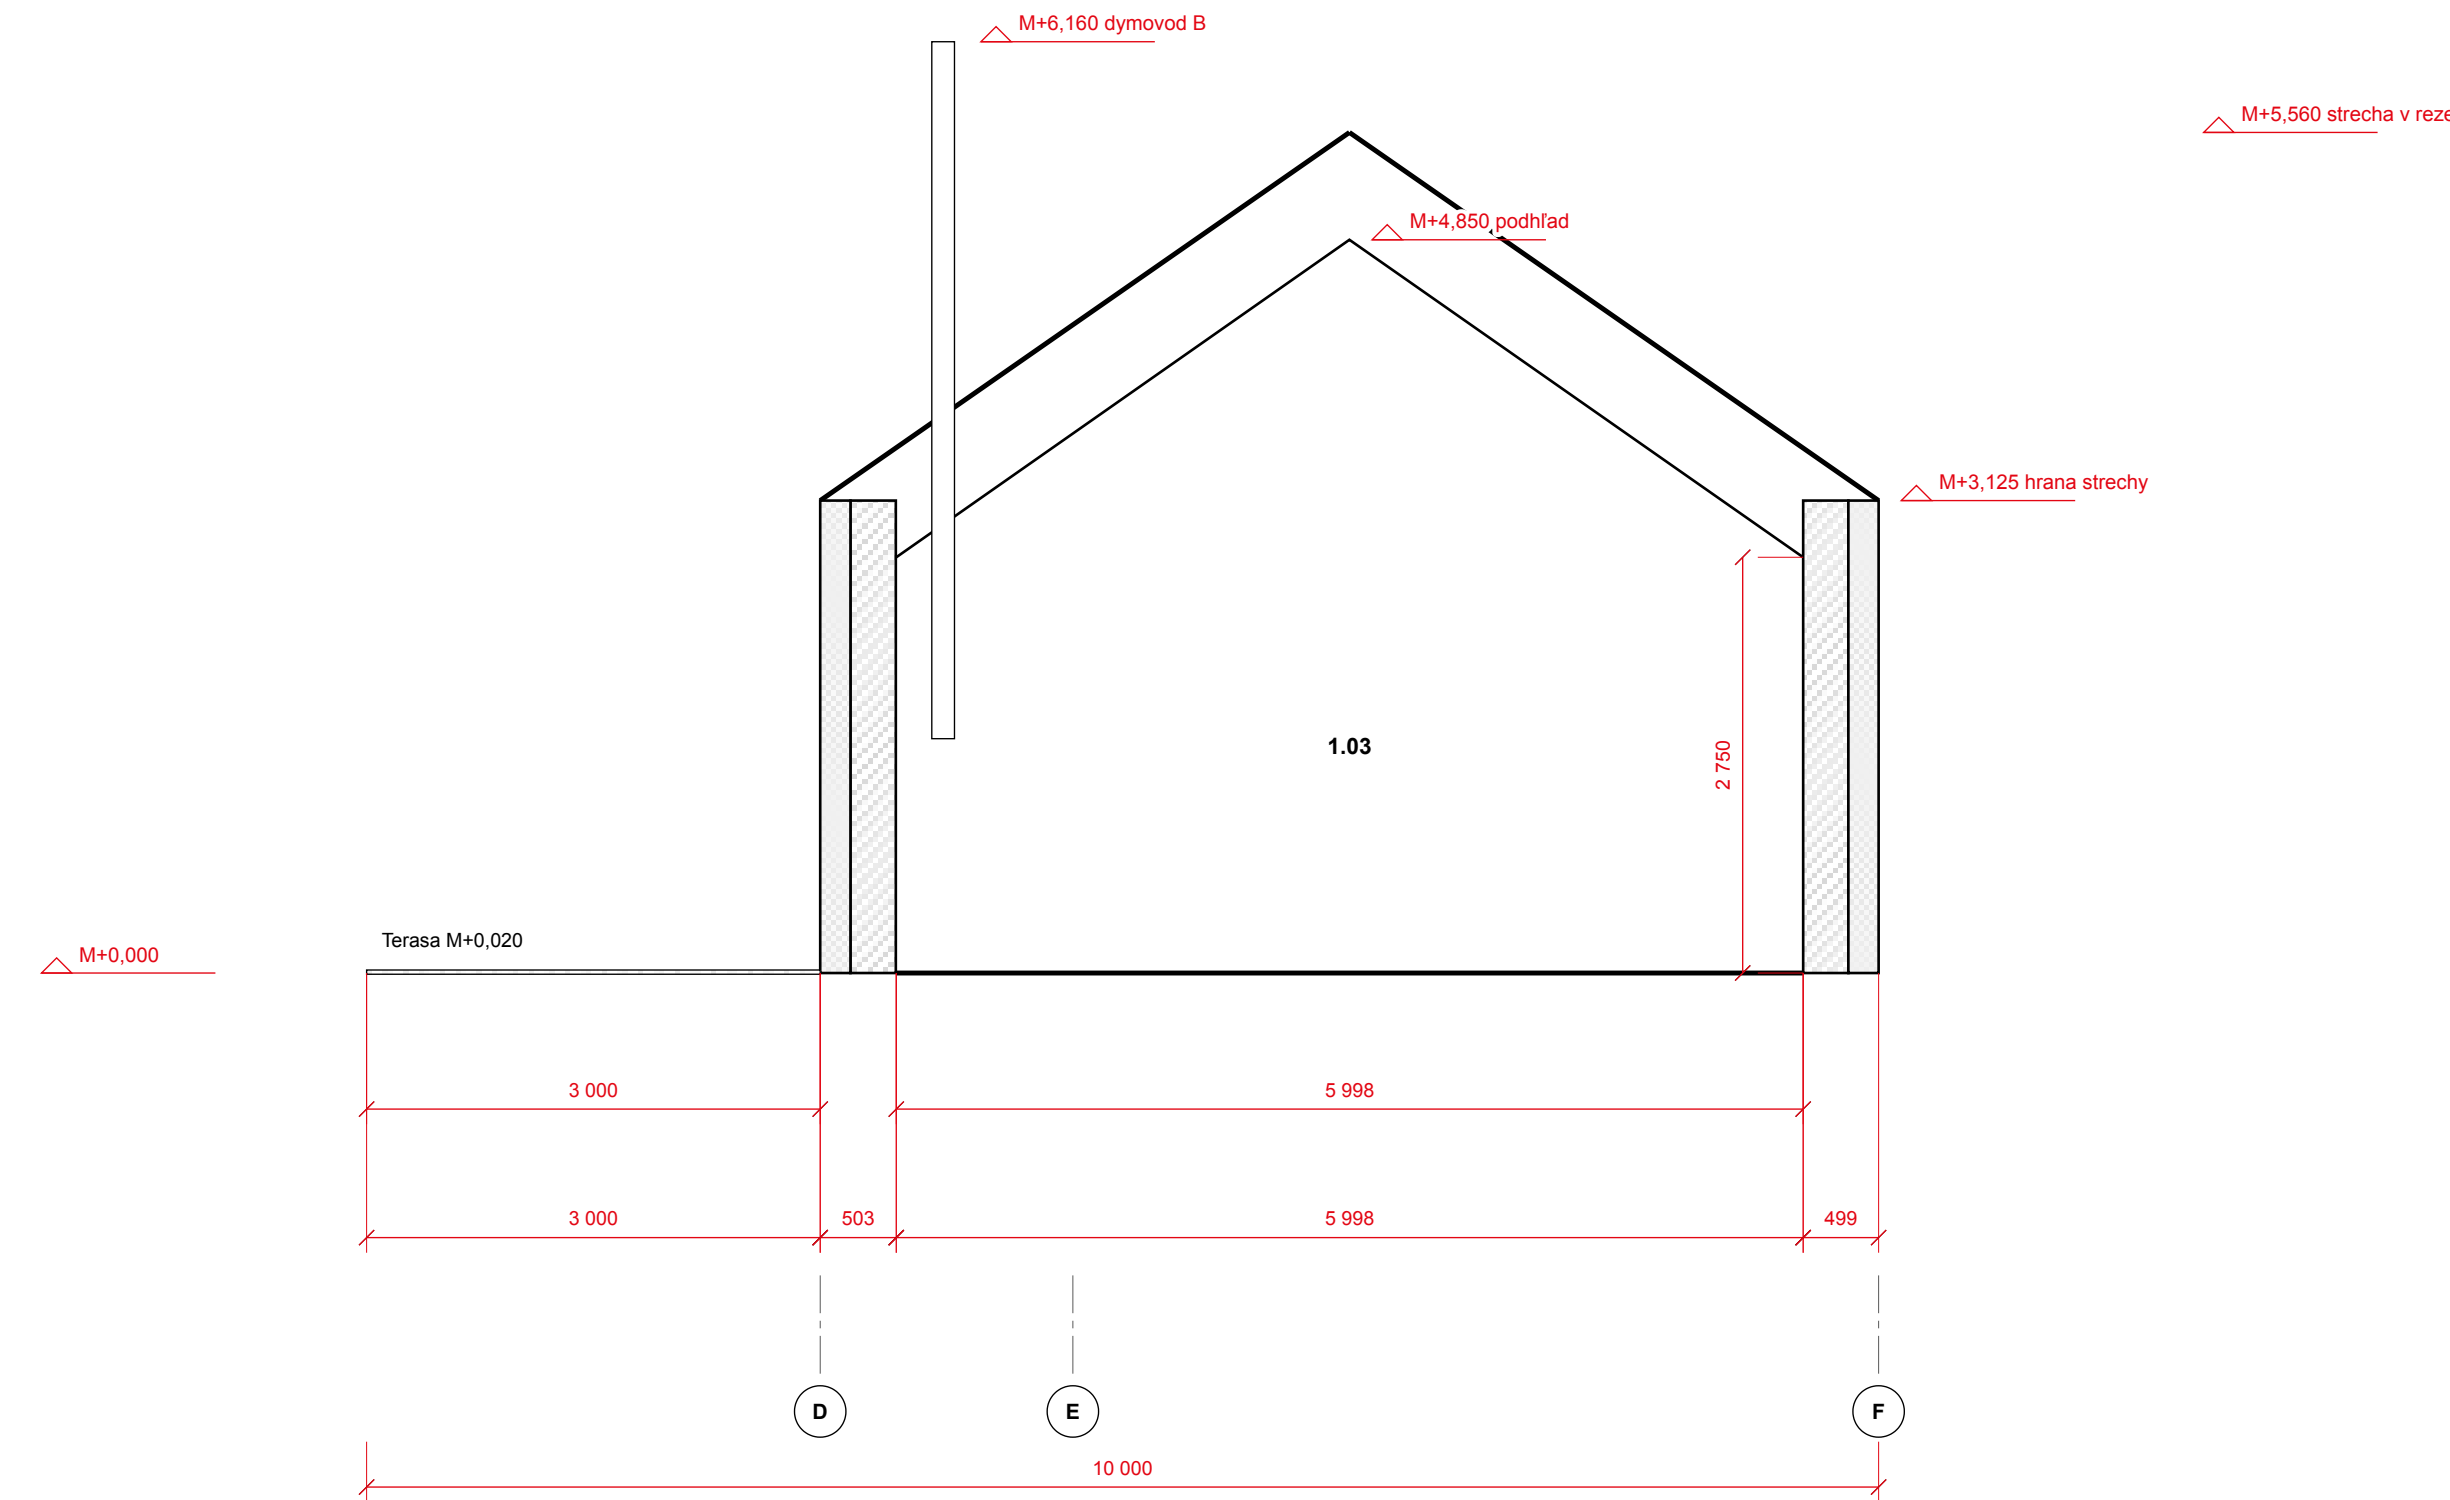

POD NOSNOU DOSKOU SA NIČ NEPREBERÁ Z ARCHÍVNEJ STATIKY.

Nové zadanie: horný monolit 350 × 600 mm, vnútorné rebrá a doska 150–200 mm; detail ZA-02. Nivelačia, výstuž a nosná skladba zatiaľ neurčené. R0 = 184,200 m na ulici; všetky výšky M sú k pôvodnej podlahe modelu.

KOORDINÁCIA NOVÝCH KONŠTRUKCIÍ

Prvok	Záväzný geometrický podklad / chýbajúci návrh
Podlaha M0	Vodovod a kanalizácia nad nosnou doskou. Podlahové vykurovanie mimo garáže, technickej a sprchy; TZ-01. Bez dodatočných vrtov do dosky.
Drevený strop a povala	Povala iba na odkladanie, bez betónovej stropnej dosky/nadbetonávky. Skladovacie a bodové zariadenia musí určiť výpočet. Katedrála 1.03 zostáva otvorená, svetlé výšky 2 750 / 4 850 mm.
Nosné línie a základy	Nový monolitický návrh podľa ZA-02, geotechniky a reakcií nosnej sústavy. Výstuž, rebrá a pracovné škáry sa nepreberajú zo starého projektu.

ZNAČKY A MATERIÁLY

- Murivo / keramické prvky
- ETICS / minerálna vlna
- Betón – len ak je určený návrhom
- Drevený obklad

Čiarkovane: prerušené / neurčené konštrukcie.
M = výška k podlahe modelu. Dĺžky v mm.
K ulici R0: z = M + ΔFFL. ΔFFL neurčené.

KONTROLA TLAČE 100 % - 1 000 mm ≈ 20 mm na papieri

1 : 50 - vypnúť „prispôbiť strane“

NOVOSTAVBA RD BŘEZÍ U MIKULOVA

PARCELA 6012/26 · HLAVNÝ NÁVRH C / B / B

B-B · Pričný rez katedrálovým stropom

R0 = 184,200 m · M0 = PODLAHA MODELU · ΔFFL = M0 – R0 ZATIAĽ NEURČENÉ

Rozmery nadzemnej architektonickej geometrie z modelu. Základy, nosná skladba podlahy a strechy, vence a krov zostávajú otvorené R01-R04; list nie je realizačný rez.

STAV

NEVYDANÉ NA REALIZÁCIU

Chýbajúci návrh sa nesmie nahradiť mierkou výkresu.

VYPRACOVAL: digitálne dvojča · bez autorizačnej pečiatky

DÁTUM 2026-09-14 FORMÁT A1 841 × 594 mm MIERKA 1 : 50

ZDROJ 6cd4bc82841b · úplné odtlačky v model-snapshot.json