


Pôdorys strechy

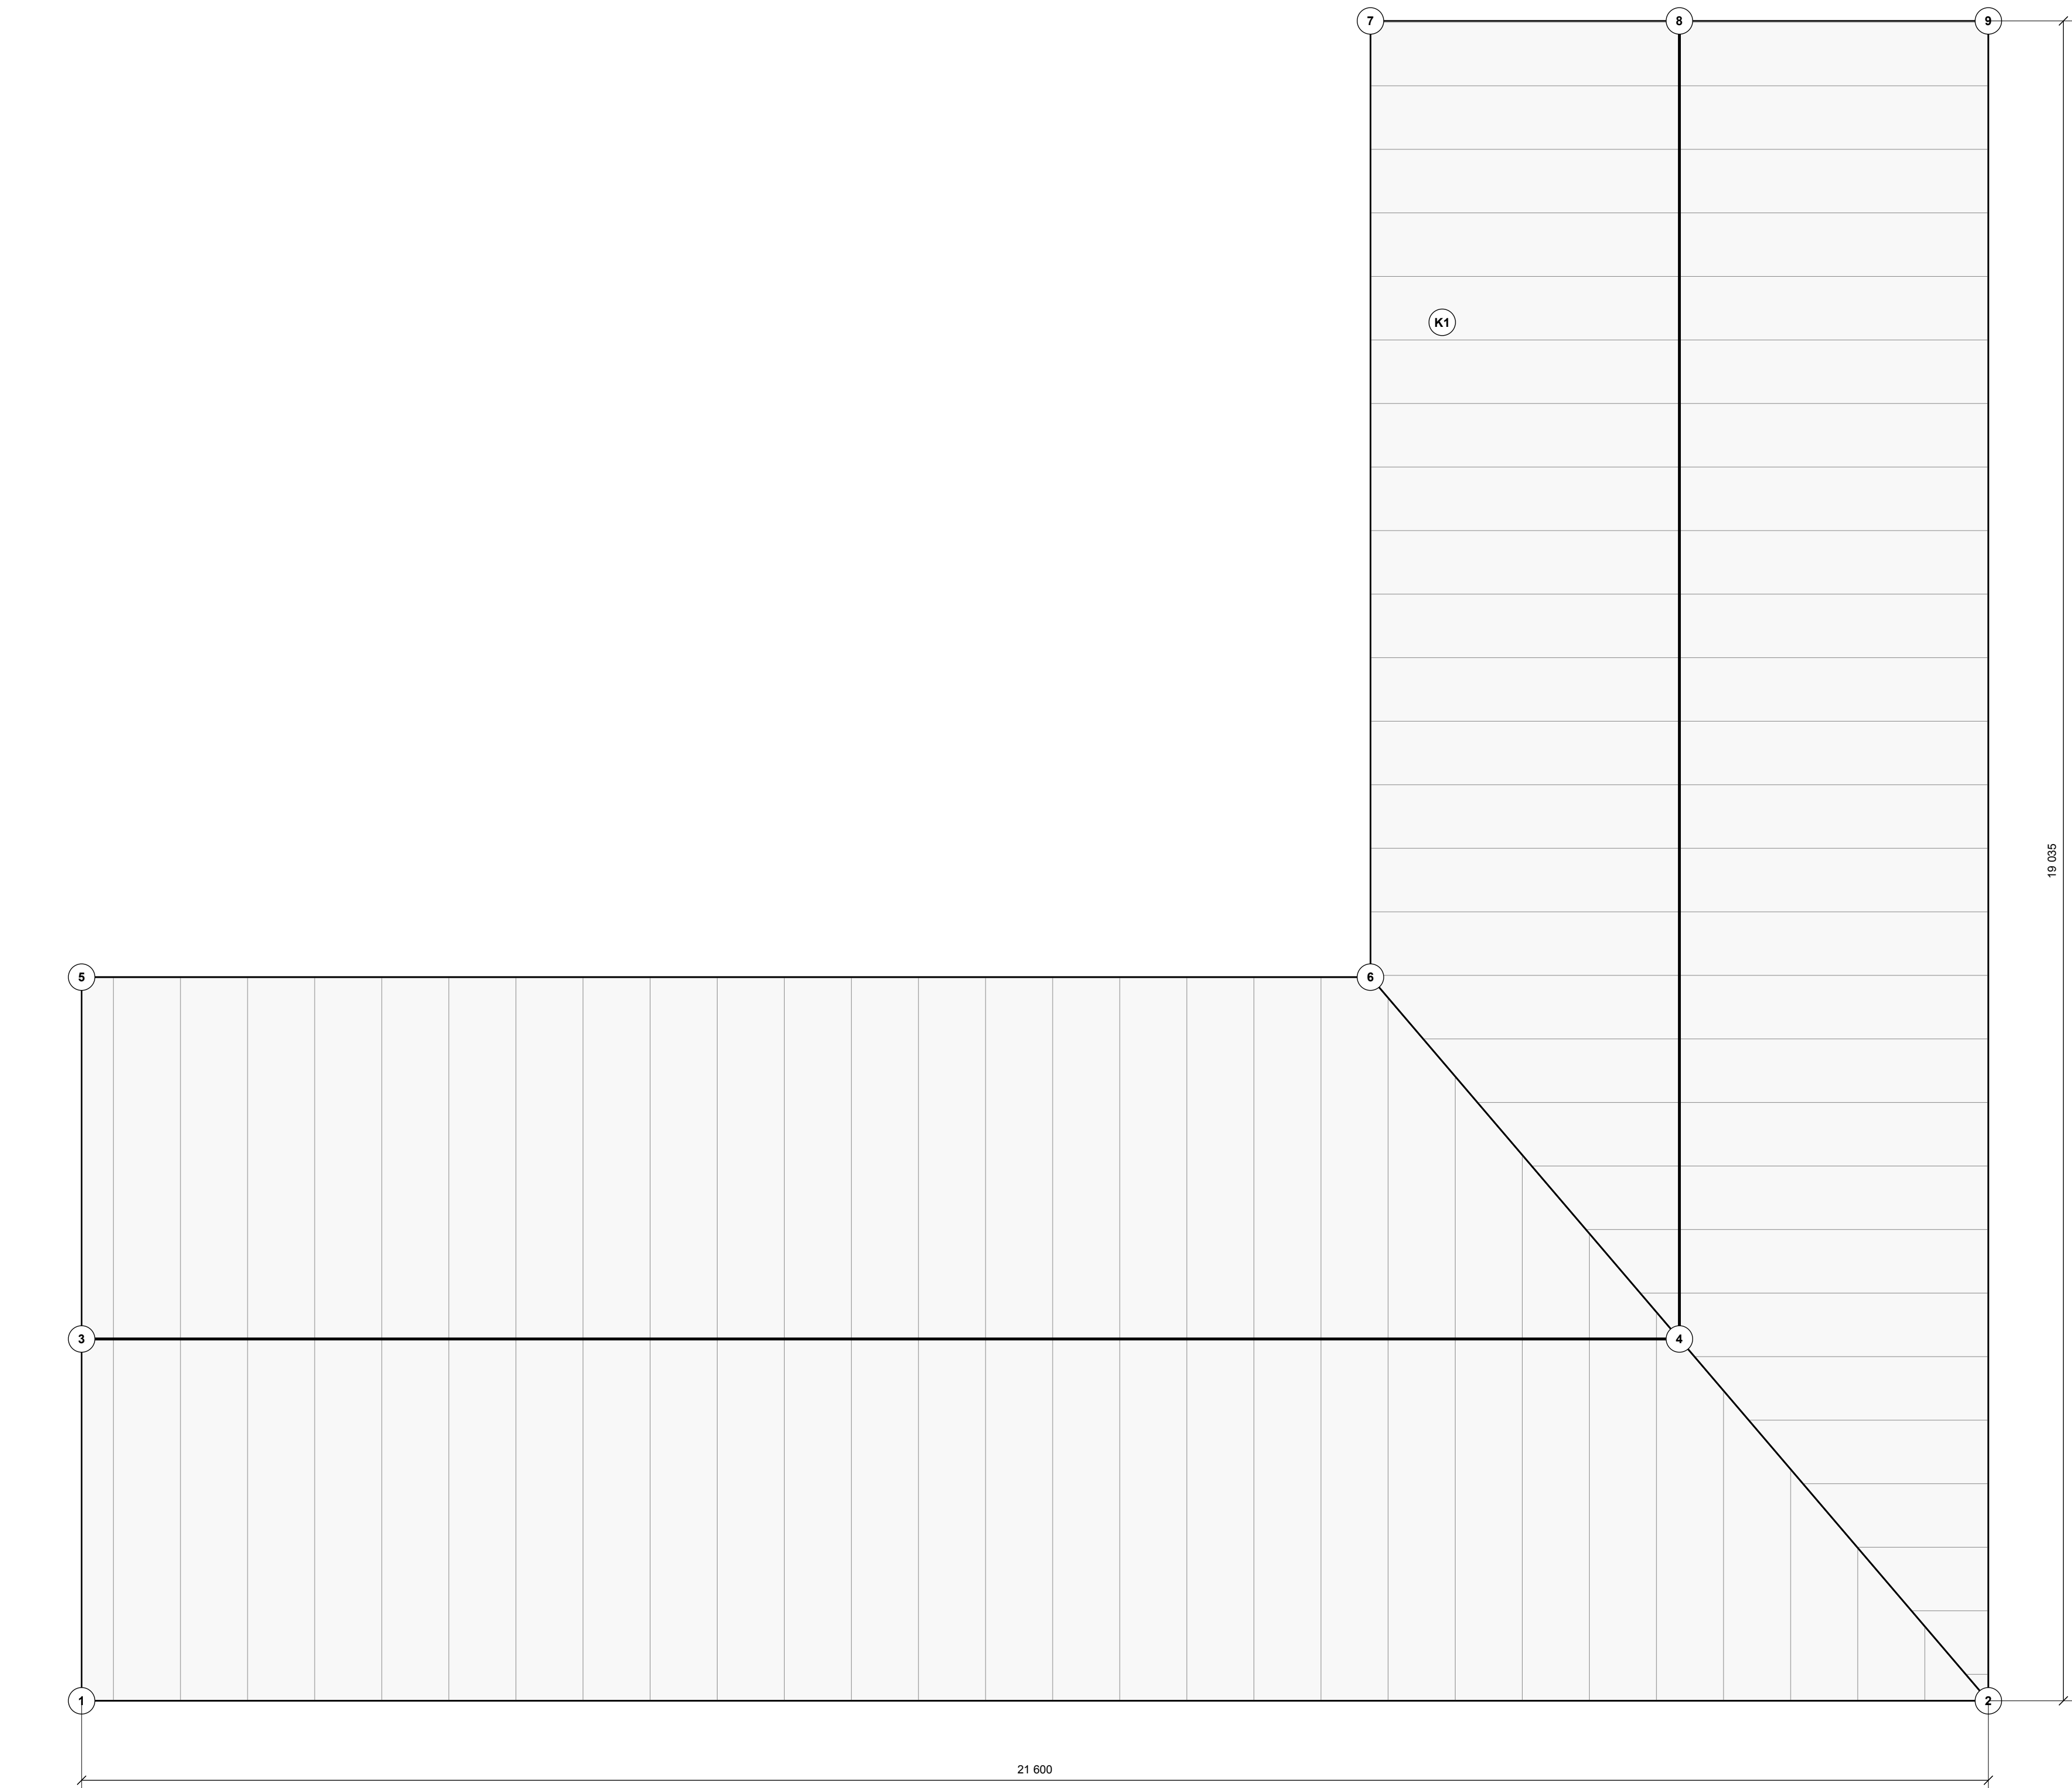

Bod	X [mm]	Y [mm]	Z [mm]	Ref.
1	6 440	3 000	3 125	ST
2	28 040	3 000	3 125	ST
3	6 440	7 100	5 560	ST
4	24 540	7 100	5 560	ST
5	6 440	11 200	3 125	ST
6	21 040	11 200	3 125	ST
7	21 040	22 035	3 125	ST
8	24 540	22 035	5 560	ST
9	28 040	22 035	3 125	ST

GEOMETRIA STRECHY Z MODELOVÝCH VRCHOLOV

Hlavný trakt: atan((5560 - 3125) / 4100) = 30.706180°. Kridlo: 34.826887°. Pôvodné štítiky 30°/34° nie sú presným sklonom tejto geometrie. Obal sa nemení.

K1: FLUE-LIVING-103-B; X 21 853, Y 18 620, Ø 150 mm, ukončenie M+6,160. Kotoľňa B zatiaľ nemá modelovanú vonkajšiu trasu dymovodu.

Falcové línie zobrazujú existujúci modelový raster krytiny. Nie sú rozmiestnením krokiev. Úžľabie, nárožie, hrebeň a odkvapné hrany sú z tej istej geometrie ako 3D.

Nové zadanie: falcovaný plech, nulový architektonický presah. Krytá terasa je zapustená hmota, nie presah. Koncová rovina strechy sa viaže na lice čela terasy; lemovanie a žľab potrebujú finálny detail.

Poväť iba na odkladanie vecí. Drevené pôdne väzňiky v pravidelnom trakte, samostatné drevené polia pri uzle L a osobitná katedrála. Bez betónového stropu a nadbetonávky. Prierezy, skladovacie zaťaženie, spoje a kotvenie vyžadujú výpočet.

KONTROLA TLAČE 100 % - 1 000 mm ≈ 20 mm na papieri

1 : 50 - vypnúť „prispôbiť strane“

NOVOSTAVBA RD BŘEZÍ U MIKULOVA

PARCELA 6012/26 · HLAVNÝ NÁVRH C / B / B

Pôdorys strechy

R0 = 184,200 m · M0 = PODLAHA MODELU · ΔFFL = M0 – R0 ZATIAĽ NEURČENÉ

Geometrické vrcholy, hrany a presahy z lib/twin-roof.ts. Návrh krovu a strešného plášťa je samostatná otvorená časť R04. Čísla bodov sú doplnkové, existujúce osi zostávajú.

STAV

NEVYDANÉ NA REALIZÁCIU

Chýbajúci návrh sa nesmie nahradiť mierkou výkresu.

VYPRACOVAL: digitálne dvojča · bez autorizačnej pečiatky

DÁTUM 2026-09-14 FORMÁT A1 841 × 594 mm MIERKA 1 : 50

ZDROJ 6cd4bc82841b · úplné odtlačky v model-snapshot.json