


Podlahové vykurovanie a rozsah povaly

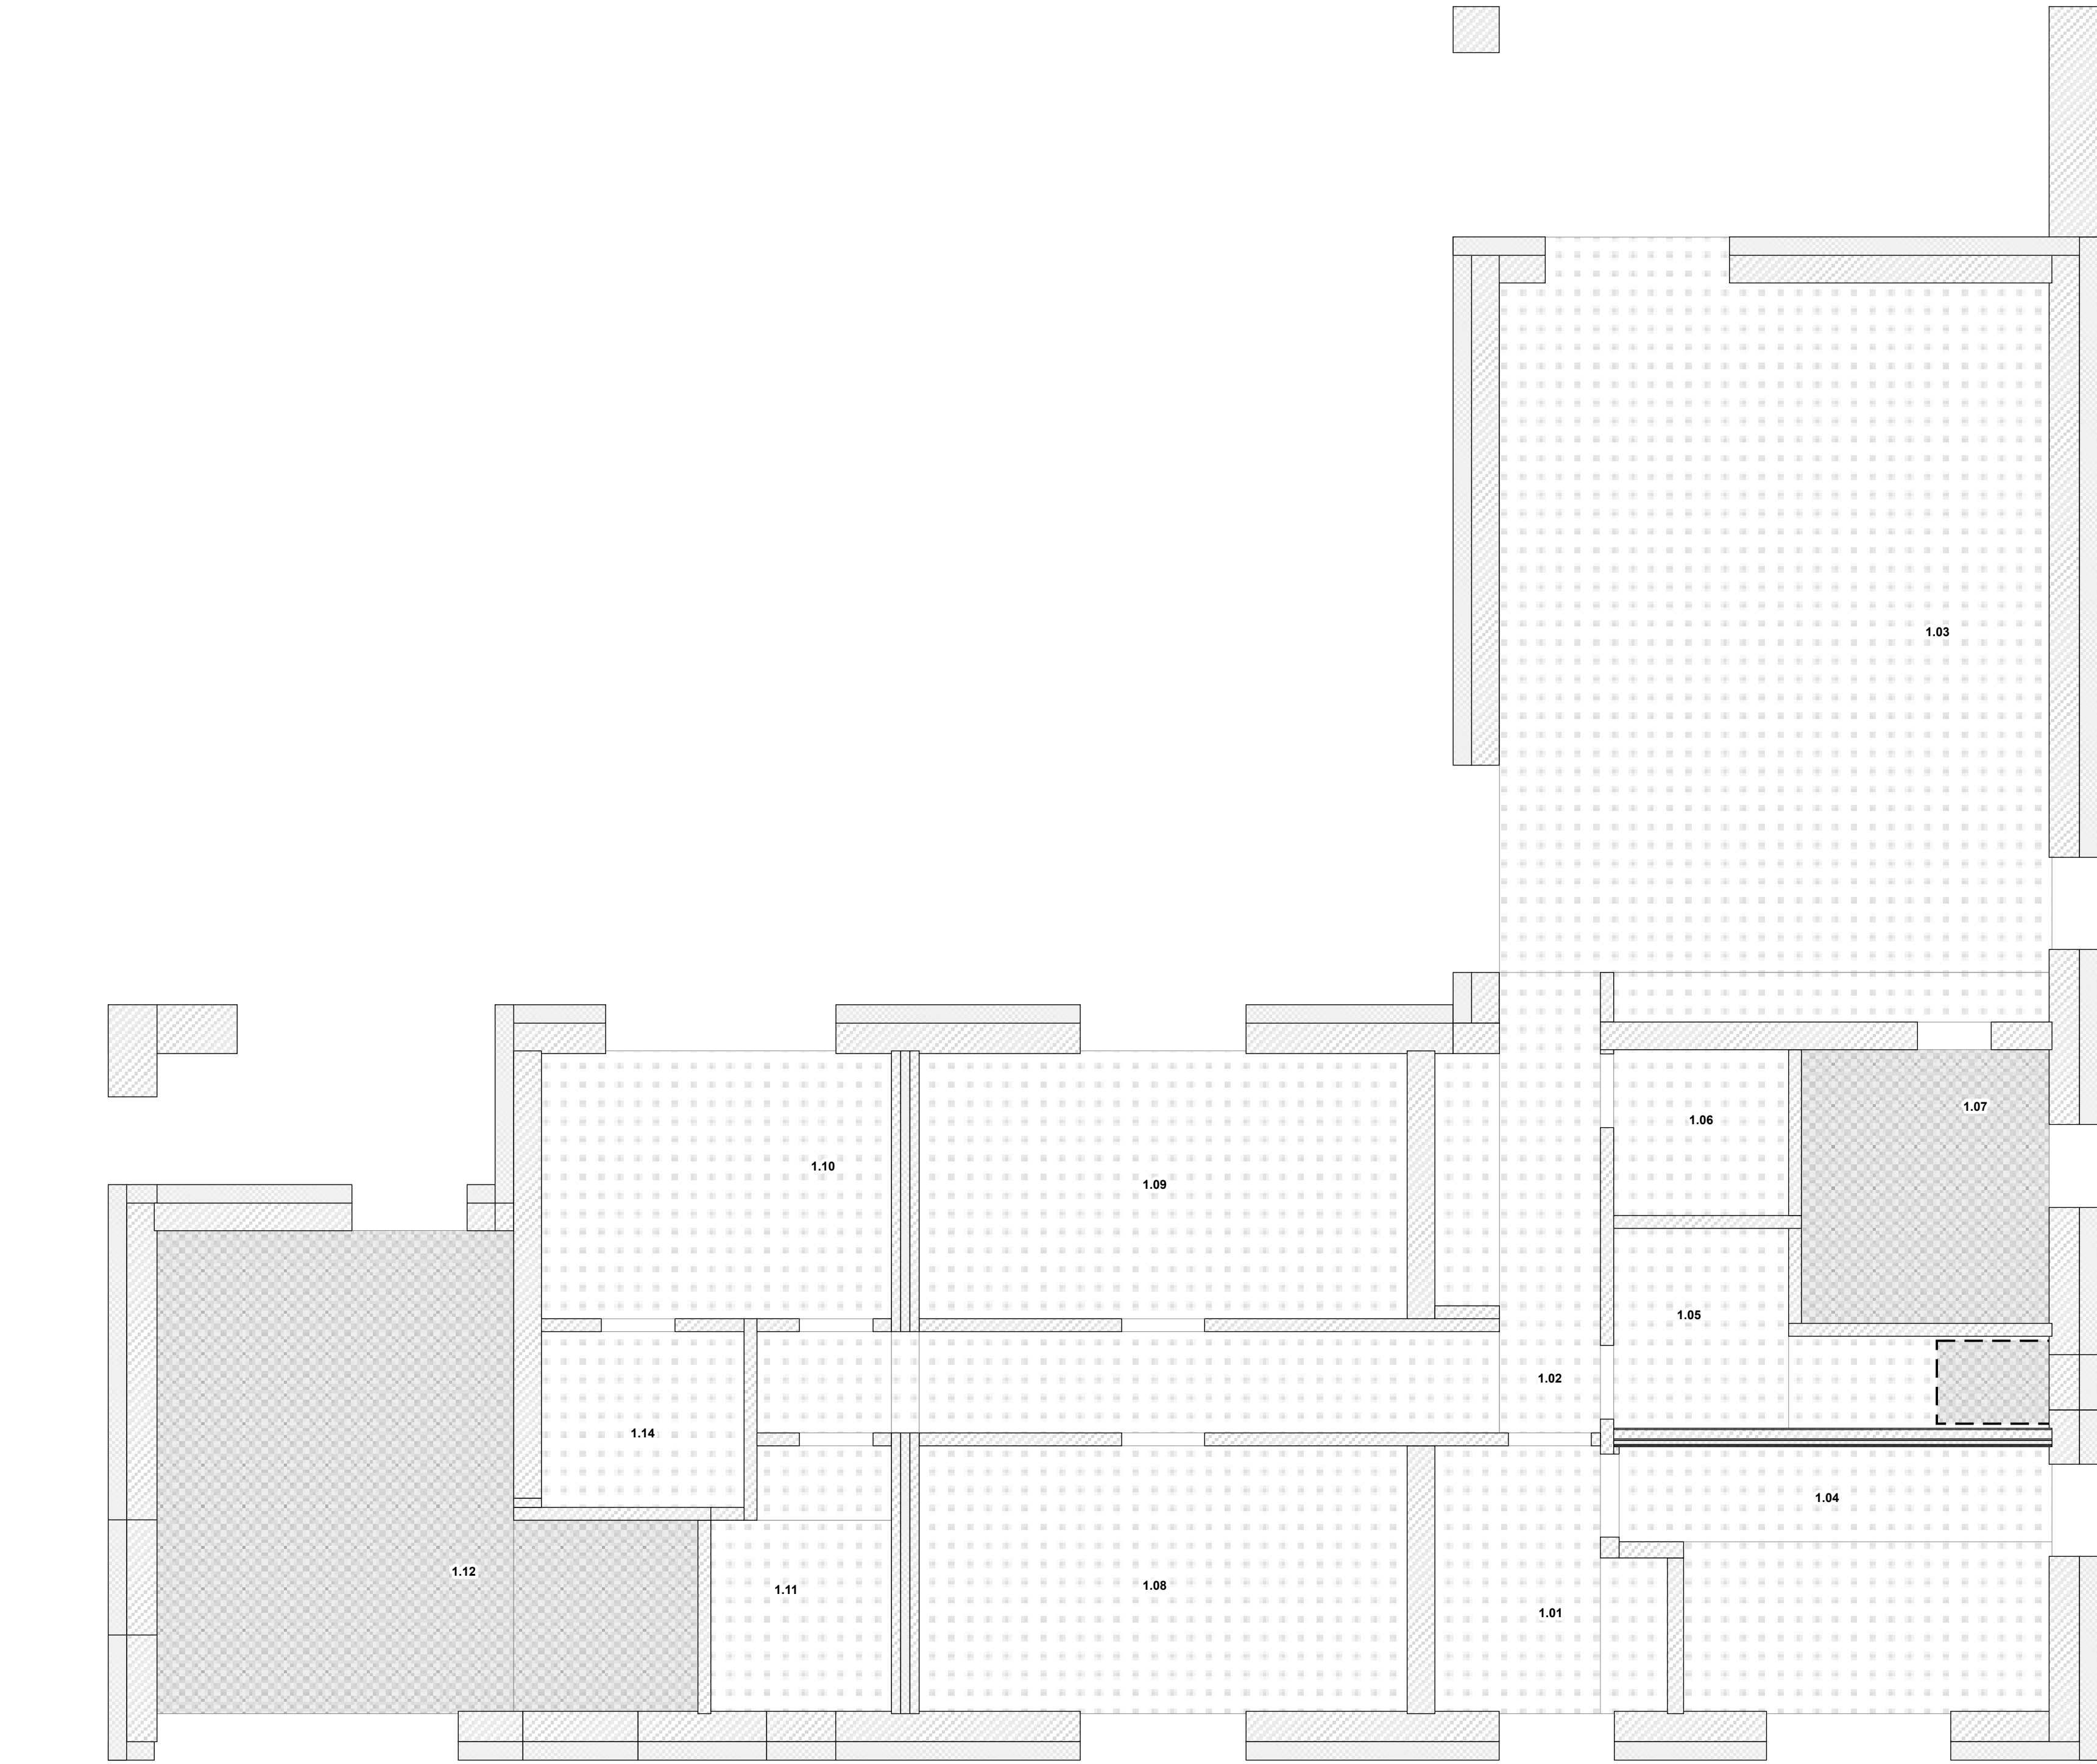

VODA A ODPAD NAD NOSNOU DOSKOU - ŽIADNE DODATOČNÉ VRTY DO DOSKY

Výšky trasovania, priemery, spády, izolačné hrúbky, vývody cez obvod a skladby vykurovaných aj nevykurovaných podláh zostávajú súčasťou nového profesijného návrhu.

KONTROLA TLAČE 100 % - 1 000 mm ≈ 20 mm na papieri

1 : 50 - vypnúť „prispôbiť strane“

NOVOSTAVBA RD BŘEZÍ U MIKULOVA

PARCELA 6012/26 - HLAVNÝ NÁVRH C / B / B

Podlahové vykurovanie a rozsah povaly

R0 = 184,200 m · M0 = PODLAHA MODELU · ΔFFL = M0 - R0 ZATIAĽ NEURČENÉ

Pôdorysná geometria bez zmeny. Nové požiadavky stavebníka sú zakreslené k miestnostiam; list nie je výpočtom kúrenia ani statickým návrhom pochôdzného stropu.

ROZSAH PODLAHOVÉHO VYKUROVANIA

Miestnosť	Rozsah zadania
1.01	Podlahové vykurovanie
1.02	Podlahové vykurovanie
1.03	Podlahové vykurovanie
1.04	Podlahové vykurovanie
1.05	Áno; okrem sprchovej plochy
1.06	Podlahové vykurovanie
1.07	Bez podlahového vykurovania
1.08	Podlahové vykurovanie
1.09	Podlahové vykurovanie
1.10	Podlahové vykurovanie
1.11	Podlahové vykurovanie
1.12	Bez podlahového vykurovania
1.14	Podlahové vykurovanie

Priestor s požadovaným vykurovaním

Vylúčený priestor / sprcha

Sprcha z modelu: X 26 291–27 541; Y 6 652–7 552 mm. Slovo „sprcha“ je vyložené ako sprchová plocha; vylúčenie celej kúpeľne 1.05 nebolo zadané.

Bodkovaná plocha znamená požadovaný rozsah vykurovania, nie kľadačský plán rúrok. Nábytok, steny a zariadenia, tepelné straty, okruhy, rozstupy a regulácia musia vstúpiť do samostatného výpočtu.

POVALA: potvrdená iba na odkladanie vecí. Drevené stropy a záklop, bez betónovej stropnej dosky a nadbetónávky. Rozsah zahŕňa garáž aj technickú; nad 1.03 zostáva otvorená katedrála. Skladovacie a bodové zaťaženia ešte treba navrhnuť.

STAV

NEVYDANÉ NA REALIZÁCIU

Chýbajúci návrh sa nesmie nahradiť mierkou výkresu.

VYPRACOVAL: digitálne dvojča - bez autorizačnej pečiatky

DÁTUM 2026-09-14 FORMÁT A1 841 × 594 mm MIERKA 1 : 50

ZDROJ 6cd4bc82841b - úplné odtlačky v model-snapshot.json