


Monolitické založenie · rozmery a väzby

MONOLIT DO ODNÍMATEĽNÉHO DEBNENIA · ZADANIE STAVEBNÍKA


Horný pás 350 × 600 mm je daný rozmer. Podľa doplnenia stavebníka je doska vylíata aj s lodžiou a krytou terasou. Lica, výšky a výstuž treba zamerať; nepoužíva sa stratené debnenie.

Z1 · HORNÝ OBVODOVÝ MONOLIT · 1 : 10

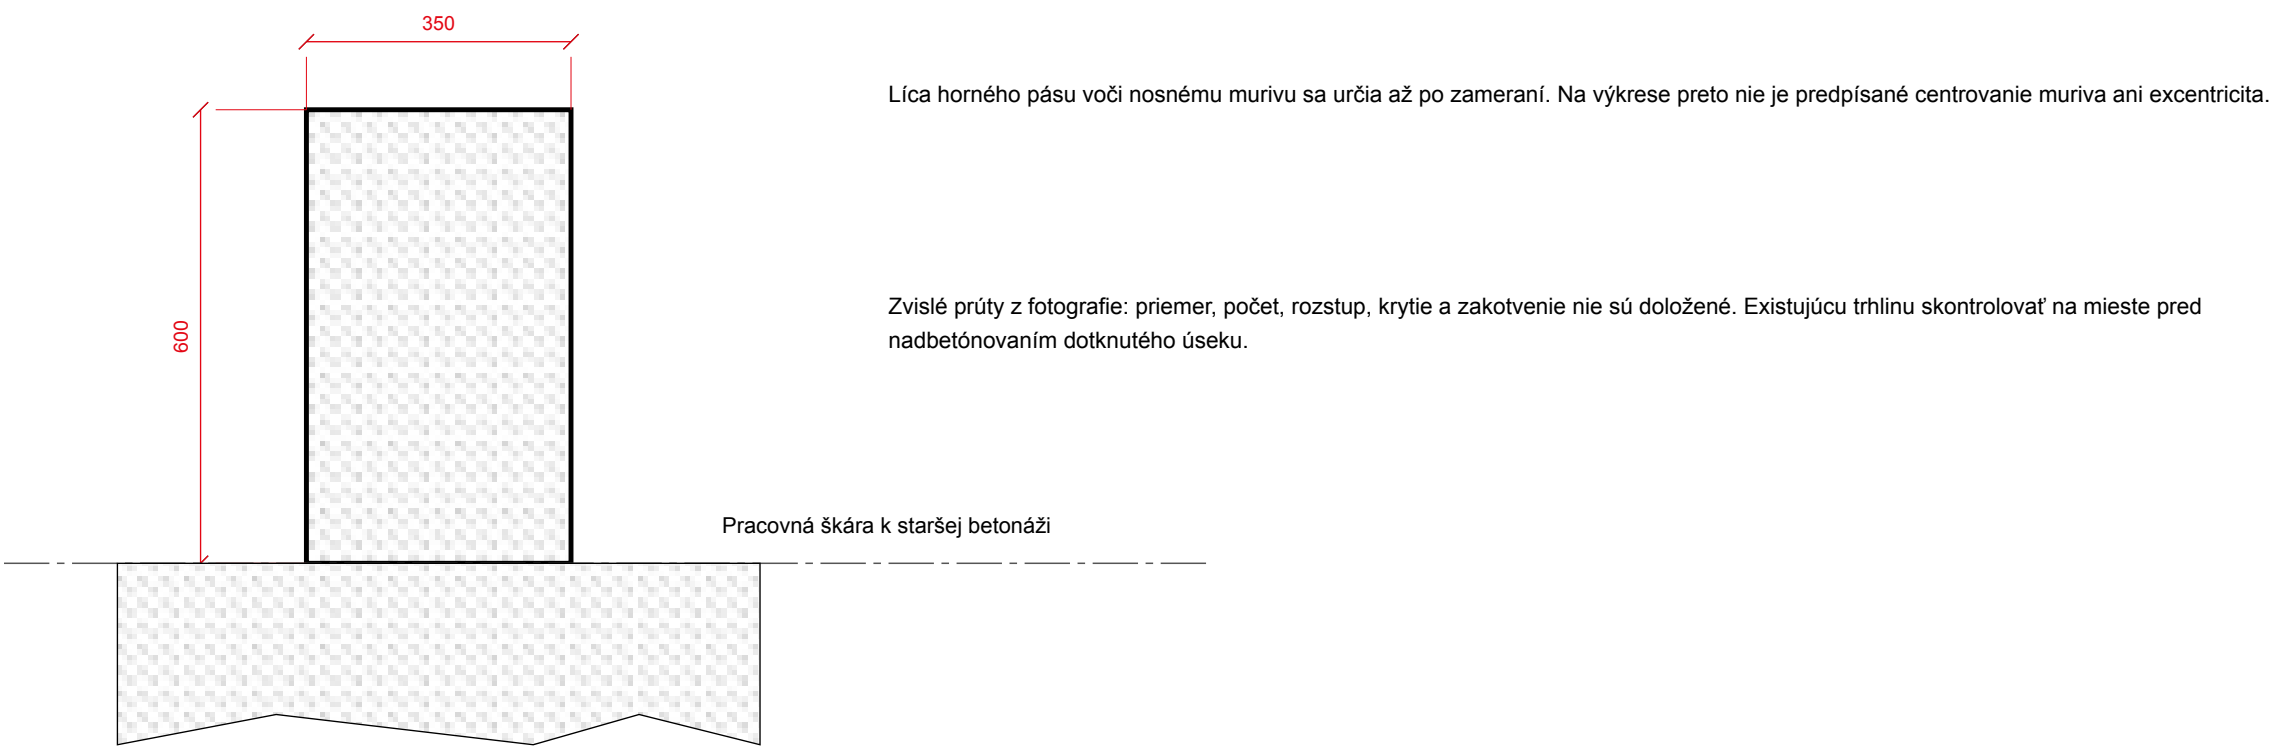

Spodný pás: 600 mm v zemi podľa stavebníka.
Šírka, spodok a horné líce voči R0 zatiaľ nezamerané.
Prerušený obrys spodného pásu neurčuje jeho šírku ani výšku.

D1 · NOSNÁ DOSKA A INŠTALÁCIE · 1 : 10

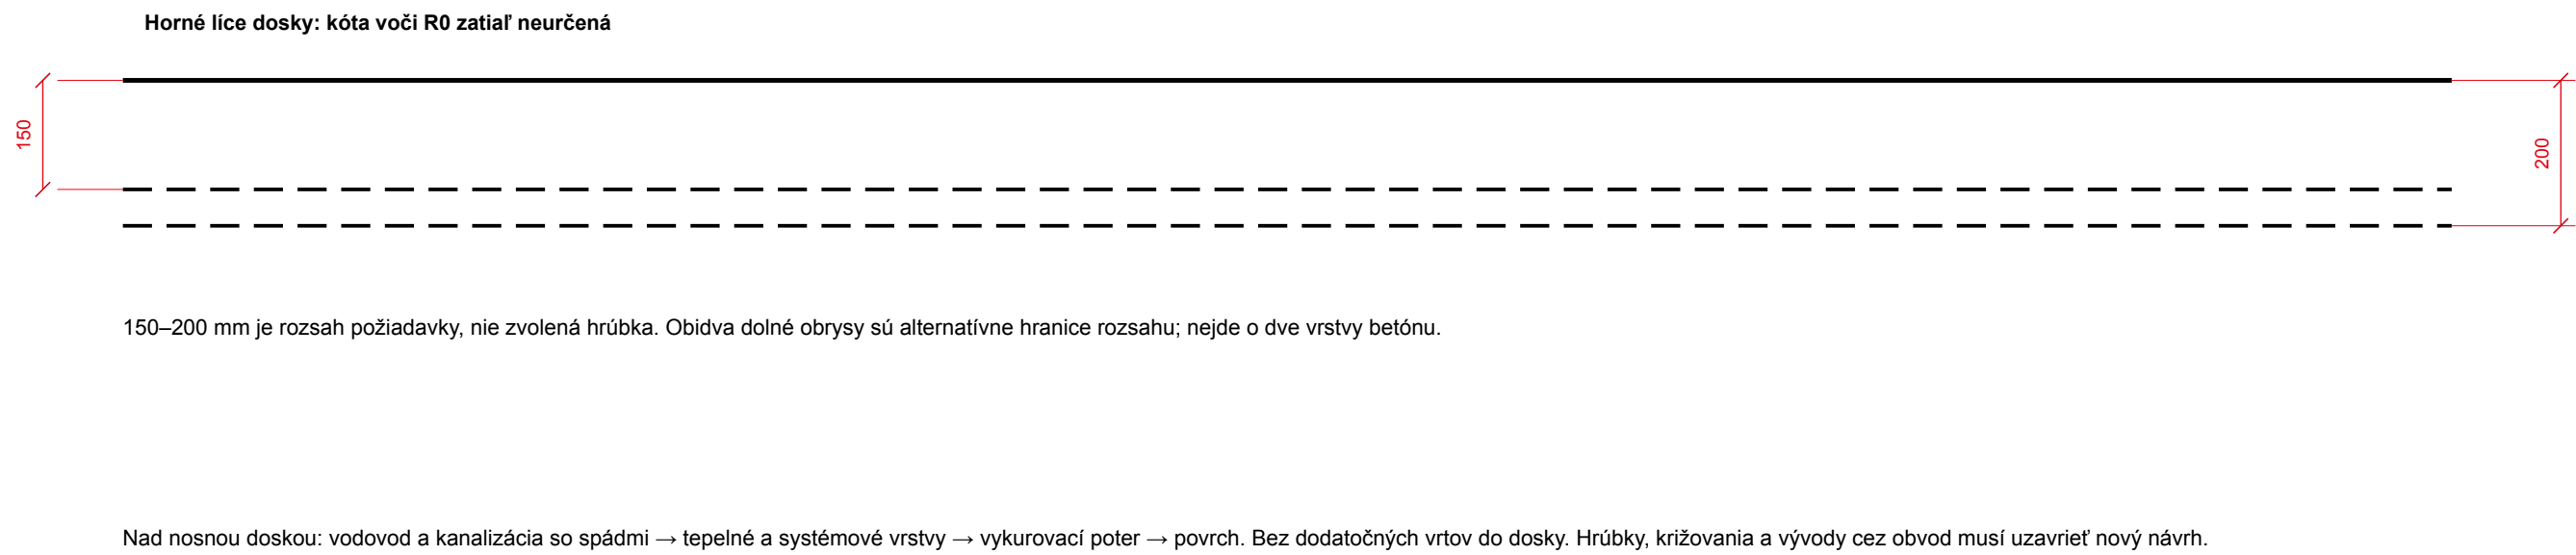

VNÚTORNÉ REBRÁ A ZÁKLADOVÁ PÔDA

Prvok / rozhodnutie	Záväzné zadanie / nadväznosť	Čo ešte určuje návrh
R1–R7 · vnútorné trasy	Monolitické, v horných 600 mm podľa stavebníka. Musia mať konkrétnu cestu prenosu zafarbenia do únosného podkladu alebo podpor.	Polohy, šírk, uloženie, výstuž a spoje podľa reakcií stien, stropu a krovu.
Zásyp pod doskou	Stavebník požaduje zhrnutú zeminu. Vhodnosť existujúcej zeminy, vlhkosť, hutnenie po vrstvách a výsledná únosnosť nie sú overené.	Geotechnické posúdenie a merateľné podmienky prevzatia podkladu.
Betón C16/20	Požadovaný pre pokračovanie; fotografie ani názov triedy nepotvrdzujú dodanú zmes alebo vhodnosť pre všetky prvky.	Doklad o dodávke, expozičné triedy, krytie a statická únosnosť. Sokel posúdiť samostatne.
Škály a monolit	Spodný pás už bol betonovaný. Nová horná časť bude mať pracovnú škáru; monolitický systém neznamená betonáž bez škály.	Priprava a posúdenie styku, prenos šmyku, zakotvenie a postup betonáže.
Ťažké priečky SA30	AK-01/02 zafaržujú dosku aj ako nenosné priečky. Ich vlastná hmotnosť je vyčíslená na ZA-01; kandidátka trasa R7 na ZA-03.	Posúdiť existujúcu dosku a podopretie oboch plášťov. SA30 ani H200 neslúžia ako potvrdené podpory strechy alebo stropu.

VÝŠKA PODLAHY SA NAVRHNE Z NADVÄZUJÚCICH ÚROVNÍ

Všetko v mm: $\Delta FFL = zE + 600 + j + p$

zE = zameraný vrch existujúceho spodného pásu nad R0; j = vrch dosky mínus vrch nového pásu; p = úplná podlahová skladba nad doskou.

Možný styk dosky s pásom	Výšková väzba; styk a únosnosť musí určiť návrh
Horné líca dosky a nového pásu zarovnané	j = 0; hrúbka dosky sa k vrchu pásu znova nepripočíta.
Celá doska uložená nad novým pásom	j = hrúbka dosky; 150–200 mm je zatiaľ len požadovaný rozsah.

KONTROLA TLAČE 100 % - 200 mm = 20 mm na papieri

1 : 10 - vypnúť „prispôbiť strane“

NOVOSTAVBA RD BŘEZÍ U MIKULOVA

PARCELA 6012/26 · HLAVNÝ NÁVRH C / B / B

Monolitické založenie · rozmery a väzby

R0 = 184,200 m · M0 = PODLAHA MODELU · ΔFFL = M0 – R0 ZATIAĽ NEURČENÉ

Rozmery 350/600/150–200 mm pochádzajú zo zadania stavebníka. Zameranie a statické overenie chýbajú. Nejde o výkres výstuže ani pokyn na pokračovanie betonáže.

STAV

NEVYDANÉ NA REALIZÁCIU

Chýbajúci návrh sa nesmie nahradiť mierkou výkresu.

VYPRACOVAL: digitálne dvojča · bez autorizačnej pečiatky

DÁTUM 2026-09-14 FORMÁT A1 841 × 594 mm MIERKA 1 : 10

ZDROJ 6cd4bc82841b · úplné odtlačky v model-snapshot.json