


Základy domu v priestore

Celý obrys vrátane lodžie a krytej terasy · ulica dole, garáž vľavo

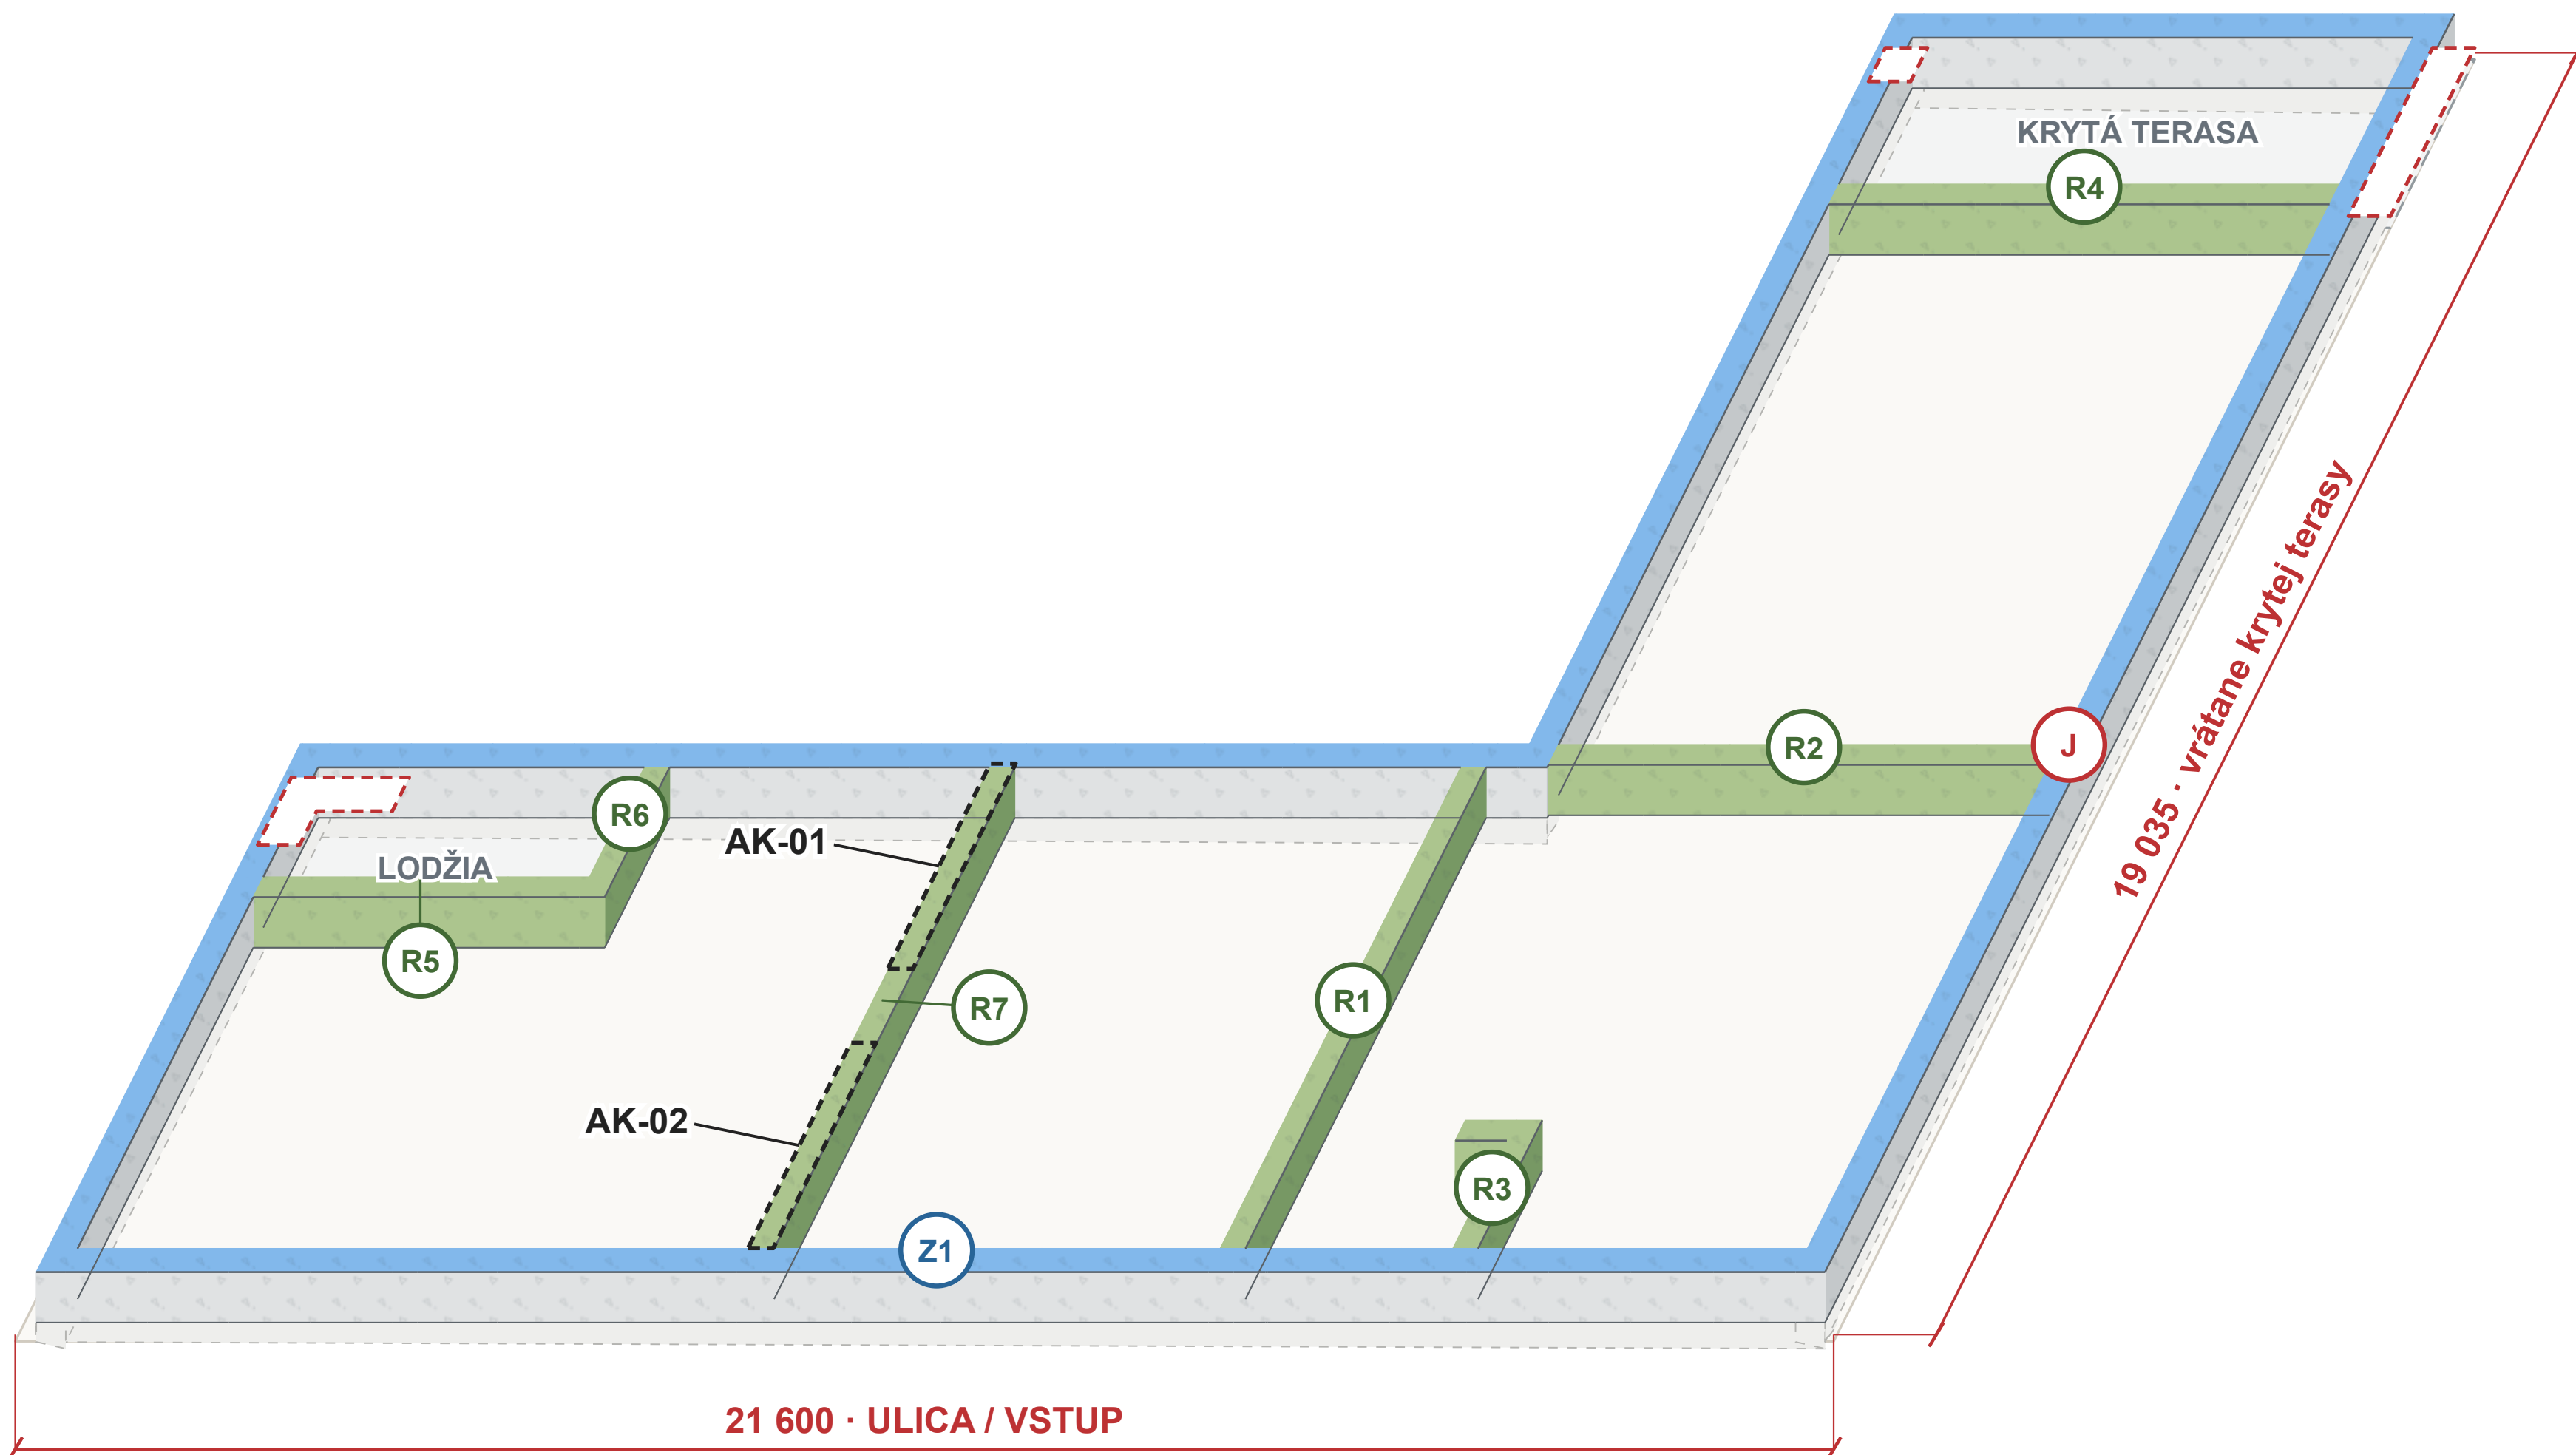

R7 · PODOPRETIE VLASTNEJ HMOTNOSTI SA30 NA VÝPOČET

AK-01 + AK-02: 456,25 kg/m muriva bez omietky, spolu 2 781,3 kg. Povrchy a ďalšie vrstvy navyše. Čiarkovane sú označené iba zaťažené úseky; chodba ostáva voľná.


Doska vrátane terás je podľa stavebníka vyliata; tu je odkrytá. R7 je návrh na posúdenie existujúcej dosky, nie pokyn na jej rezanie alebo betónáž.

NÁVRH NA KOORDINÁCIU · NEVYDANÉ NA REALIZÁCIU

ČO V OBRÁZKU VIDIŠ

- Z1** **Obvod vrátane oboch terás**
350 × 600 mm podľa zadania. Líca a skutočné rozmery treba zamerať.
- R** **R1 až R7 · návrhové trasy**
R1–R6 podľa stien a terás. R7 pod vlastnou hmotnosťou SA30. Výška 600 mm; šírka, uloženie a výstuž na výpočet.
- J** **Napojenie rebra na obvod**
Označené miesto na návrh spojenia. Obrázok nepredpisuje priemery, počty ani kotvenie prútov.

J · PRINCÍP NAPOJENIA

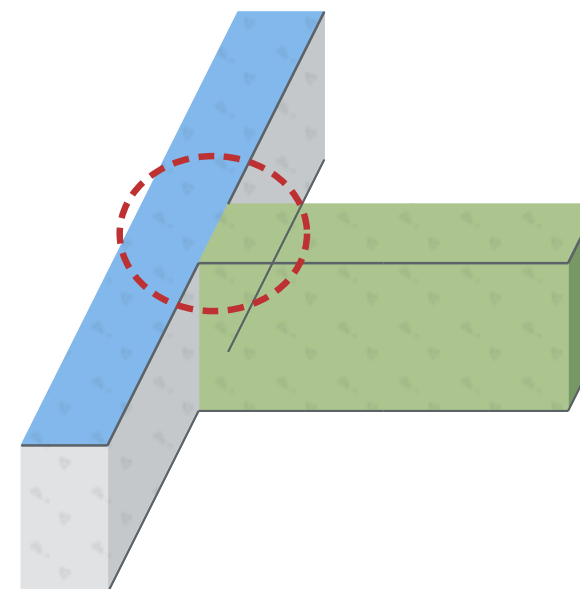

Zväčšený princíp bez mierky. Šírka rebra je grafická. Čiarkované obrysy na terasách označujú nadzemné podpery.

Spodný pás: podľa stavebníka 600 mm v zemi. Jeho náznak je prerušovaný; šírka a kóty výkopu zostávajú neurčené.

Axonometria bez odmeriavania · súradnice z modelu C/B/B

KONTROLA TLAČE 100 % · úsečka 20 mm na papieri

Axonometria bez mierky; z obrázka neodmeriavať rozmery.

NOVOSTAVBA RD BŘEZÍ U MIKULOVA

PARCELA 6012/26 · HLAVNÝ NÁVRH C / B / B

Základy · priestorový pohľad na pásy a rebrá

R0 = 184,200 m · M0 = PODLAHA MODELU · ΔFFL = M0 – R0 ZATIAĽ NEURČENÉ

Celý L-obrys vrátane lodžie a krytej terasy. R7 dopĺňa kandidátny pás pod vlastnou hmotnosťou SA30; priečky zostávajú nenosné pre strechu a strop. R1–R7 nemajú potvrdené prierezy, uloženie ani výstuž. Podklad a zdroj hmotnosti: ZA-01.

STAV

NEVYDANÉ NA REALIZÁCIU

Chýbajúci návrh sa nesmie nahradiť mierkou výkresu.

VYPRACOVAL: digitálne dvojča · bez autorizačnej pečiatky

DÁTUM 2026-09-14 FORMÁT A1 841 × 594 mm MIERKA axonometria

ZDROJ 6cd4bc82841b · úplné odlišky v model-snapshot.json