

ŠTYRI REBRÁ - TECHNICKÝ PÔDORYS

C / B / B | 16. 9. 2026 | všetky kóty v mm | pracovná šírka rebier 350*

KOORDINAČNÝ VÝKRES Z MODELU - PRED VYTÝČENÍM POTVRDIŤ ZAMERANIE A NÁVRH ŠTYROCH REBIER

REFERENCIE A - D

A ľavé, B uličné, C pravé a D zadné vonkajšie líce navrhovaného horného obvodu širokého 350 mm. Sívá prerušovaná čiara.

Modrá značí iba rozsah už vyliateho spodného obvodu. Jeho skutočné hrany nie sú zamerané; šírka modrej čiary nie je kóta.


Červená = nové rebrá, pracovná šírka 350*

*350 mm = šírka betónového rebra, nie šírka výkopu ani spodnej pätky. Prevzatá zo staršej štúdie; pre 4 rebrá staticky nepotvrdená.

Pôdorys kótuje polohu osí voči hranám A-D. Presné vzdialenosti k obohm hranám rebra sú v tabuľke vpravo. Líce rebra = os ± 175 mm.

Mierka 1 : 100 pri tlači A3 / 100 %

Kontrolná úsečka 50 mm na papieri = 5 000 mm v modeli.

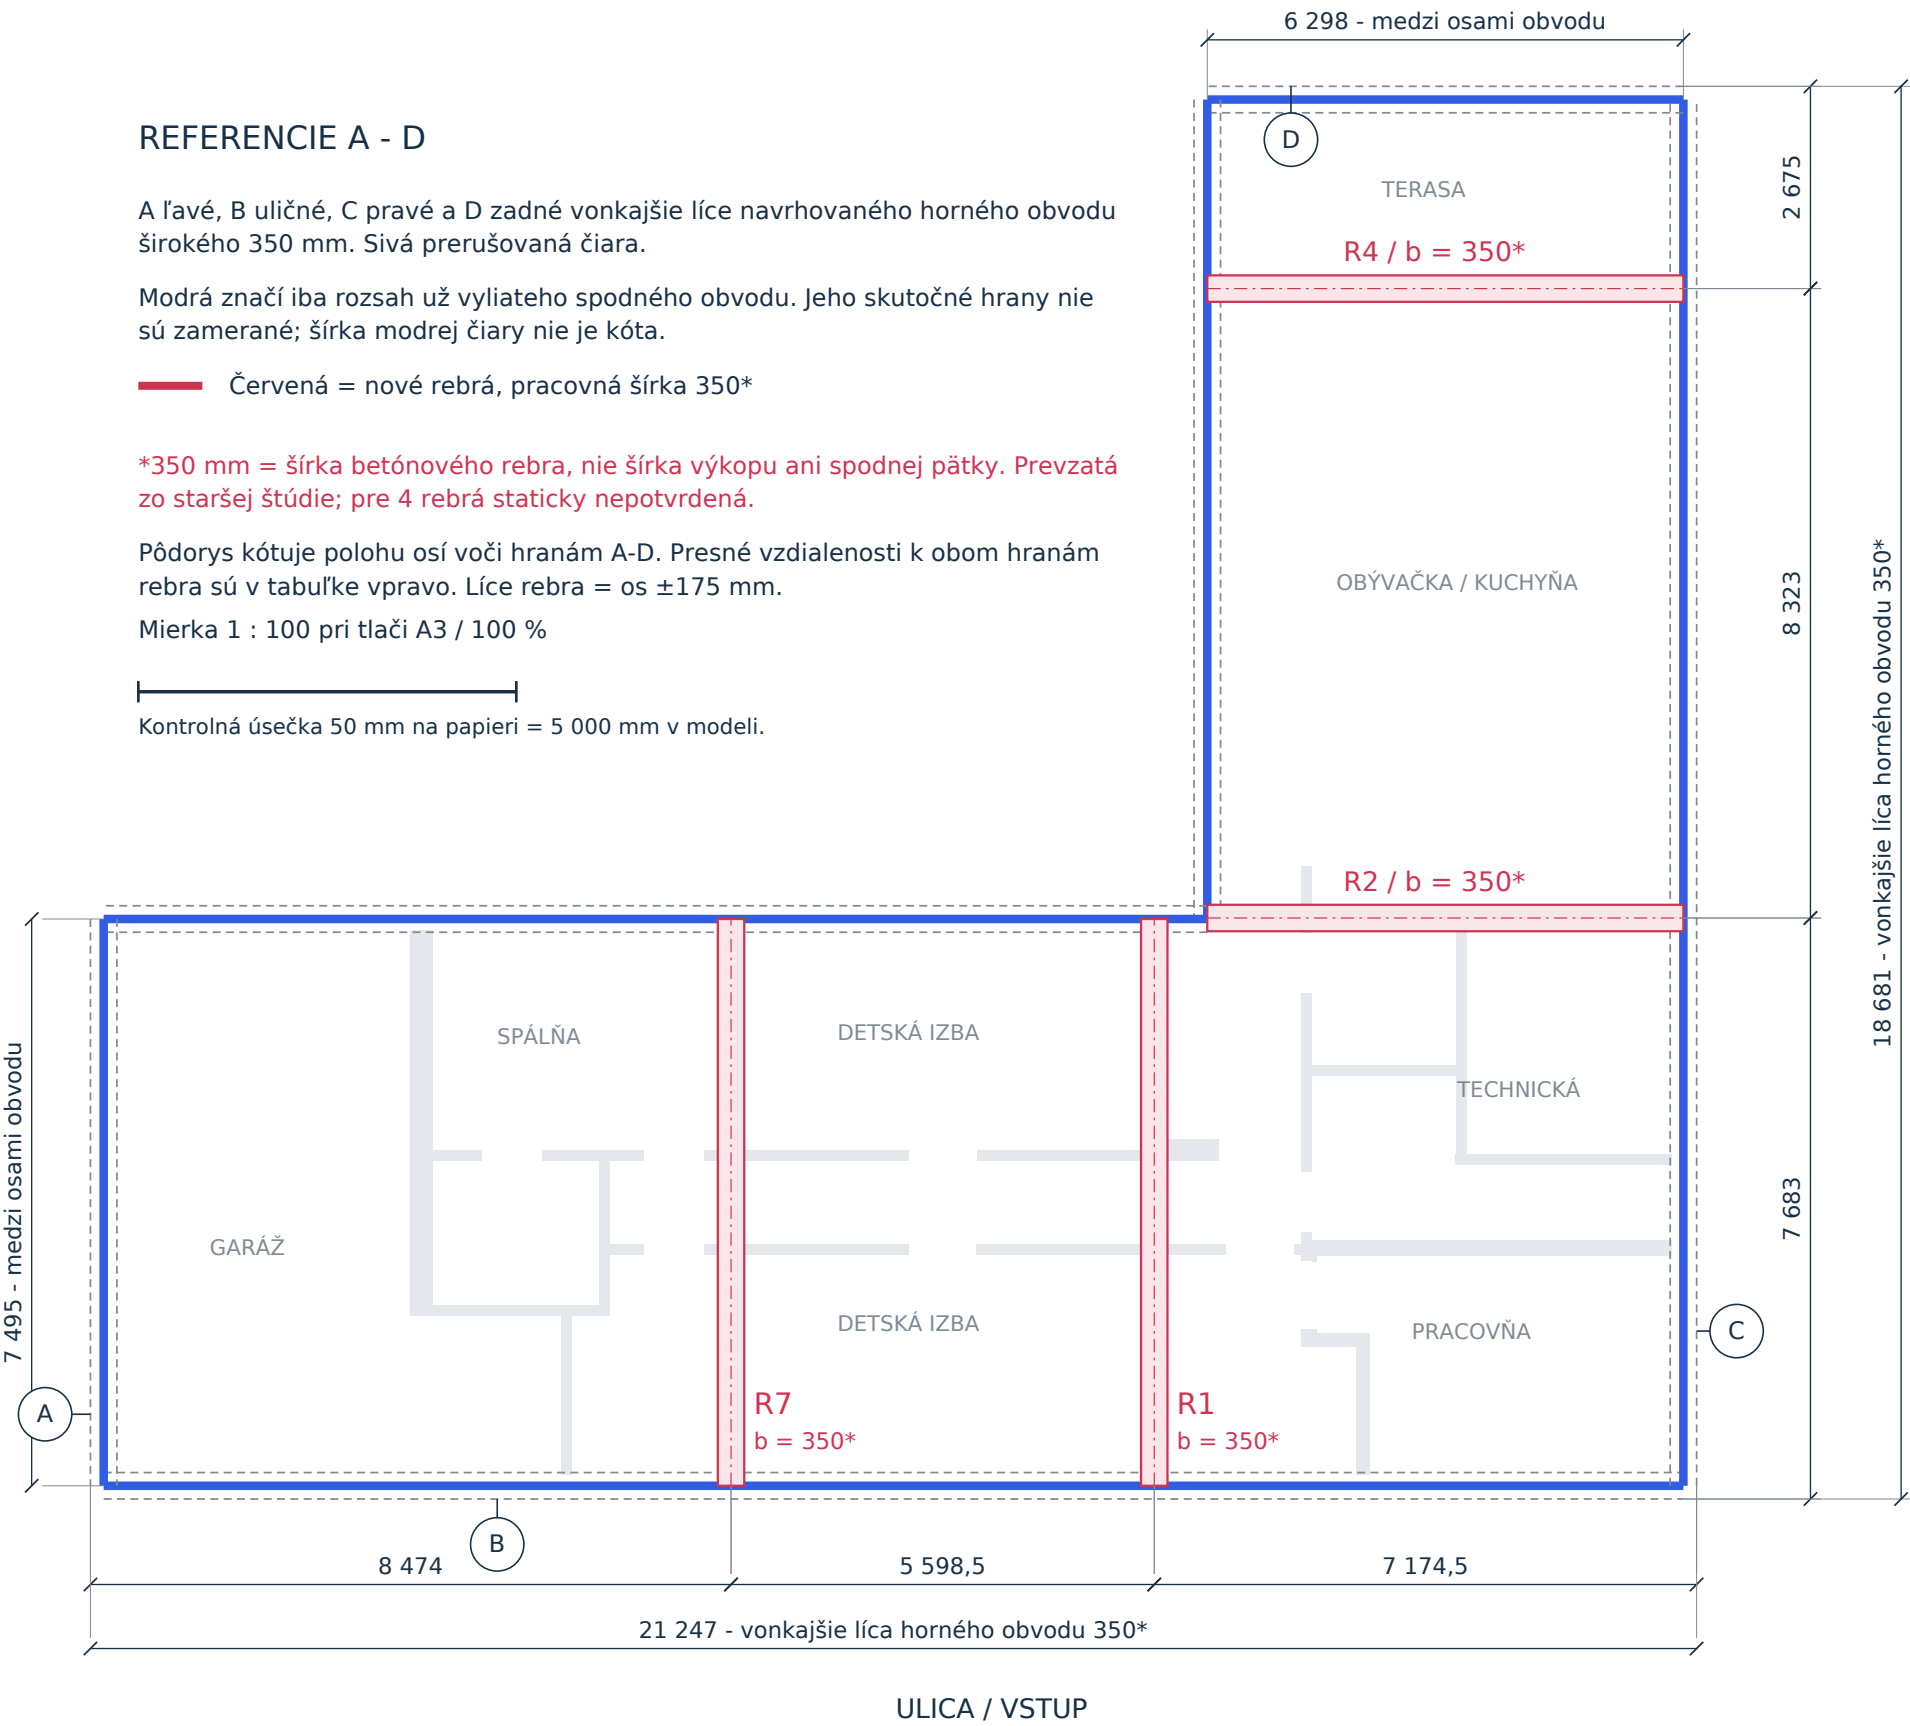

KÓTY OD OKRAJA PO REBRO

Všetko v mm. Meranie kolmo dovnútra od modelovej vonkajšej hrany A/B/C/D.

Rebro / od	Bližšia hrana	Os	Vzdialenejšia hrana
R7 / A	8 299	8 474	8 649
R1 / C	6 999,5	7 174,5	7 349,5
R2 / B	7 508	7 683	7 858
R4 / D	2 500	2 675	2 850

Príklad R7: od A po prvú hranu 8 299; ďalších 350 tvorí šírka rebra. Jeho os je od A 8 474.

R1 sa meria sprava od C smerom doľava. R4 sa meria zozadu od D smerom k ulici. R2 od B smerom do záhrady.


Rebro	Šírka*	Dĺžka medzi osami obvodu
R7	350	7 495
R1	350	7 495
R2	350	6 298
R4	350	6 298

Dĺžka medzi osami neurčuje kotevnú dĺžku ani koniec výstuže. Svetlé medzery medzi 350mm hornými pásmi: R1/R7 = 7 145; R2/R4 = 5 948.

Detail pri L-rohu: R1 a R2 nie sú jeden uzol. Ich osi sú v X vzdialené 701,5. R2 je v modeli o 13 mm smerom do záhrady oproti osi horného obvodu hlavného traktu; nevyrovnávať ich z obrázka.

Pred betonážou: preniesť model na zameraný obvod a potvrdiť prierezy, podopretie, výstuž a spoje pre zostavu štyroch rebier. Tento list nedokladá ich únosnosť.

PÔDORYSNÝ DETAIL ŠÍRKY / 1 : 10

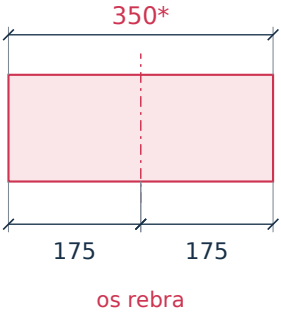

REFERENČNÉ HRANY A KONTROLA KÓT

C / B / B | 16. 9. 2026 | všetky kóty v mm | pracovná šírka rebier 350*

KOORDINAČNÝ VÝKRES Z MODELU - PRED VYTÝČENÍM POTVRDIŤ ZAMERANIE A NÁVRH ŠTYROCH REBIER

1 / ČO JE NAOZAJ OKRAJ A - D

Modelové líca horného 350mm obvodu sú odvodené z jeho osí. Nie sú to hrany fasády s izoláciou a nie sú to zamerané hrany už vyliateho pásu.

Referencia	Os horného obvodu	Modelové vonkajšie líce
A - ľavá	X = 6 794	X = 6 619
B - uličná	Y = 3 354	Y = 3 179
C - pravá	X = 27 691	X = 27 866
D - zadná	Y = 21 685	Y = 21 860

Súradnice referencií sú v lokálnom rámci modelu C/B/B. A je 179 mm vpravo od architektonického ľavého obrysu; B 179 mm za uličným obrysom; C 174 mm dovnútra od pravého obrysu; D 175 mm dovnútra od zadného obrysu.

2 / AK SA MERIA OD DNEŠNÉHO SPODNÉHO BETÓNU

Tabuľka nižšie platí iba vtedy, ak je dnešný pás súosý s modelom a má v mieste merania presne uvedenú šírku. Súososť sa nepotvrdila. Pri odchýlke sa kóty prepočítajú podľa zameraného líca.

Rebro / smer	Pás 400: do hrany / osi	Pás 380: do hrany / osi
R7 / A	8 324 / 8 499	8 314 / 8 489
R1 / C	7 024,5 / 7 199,5	7 014,5 / 7 189,5
R2 / B	7 533 / 7 708	7 523 / 7 698
R4 / D	2 525 / 2 700	2 515 / 2 690

Vzťah: vzdialenosť od vonkajšieho líca do osi rebra = vzdialenosť modelových osí + polovica skutočnej šírky referenčného pásu. Do bližšieho líca rebra odpočítať 175 mm. Pri nesúososti pridať zameranú podpísanú korekciu.

Pri páse 380 mm je jeho vonkajšie líce o 10 mm bližšie k vlastnej osi než pri páse 400 mm. Táto 10mm zmena nie je toleranciou stavby a nevyjadruje neznámu odchýlku polohy celého pásu.

3 / CELÉ REŤAZCE A NEZÁVISLÁ KONTROLA

Vodorovne A → os R7 → os R1 → C:
8 474 + 5 598,5 + 7 174,5 = 21 247
Zvisle B → os R2 → os R4 → D:
7 683 + 8 323 + 2 675 = 18 681

Voľná vzdialenosť medzi lícami*	mm
Vnútorne ľavé líce obvodu → R7	7 949
R7 → R1	5 248,5
R1 → vnútorné pravé líce obvodu	6 649,5
Vnútorne uličné líce obvodu → R2	7 158
R2 → R4	7 973
R4 → vnútorné zadné líce obvodu	2 150

*Pri všetkých horných obvodových pásoch aj rebrách širokých 350 mm. Reťazce sú geometrické, nepreukazujú podopretie dosky ani realizovateľnosť spojov.

4 / PRENOS NA STAVBU

- Zamerať skutočné vnútorné a vonkajšie líca vyliatych pásov, rohy, šírky a výšky.
- Skontrolovať súlad s modelovým rámcom a preniesť referencie A-D; určiť prípadné odchýlky.
- Po potvrdení 350mm prierezu vytýčiť os každého rebra a obe hrany ±175 mm.
- Skontrolovať väzbu na steny, pravé uhly a L-roh. Odsúhlasiť nosnú funkciu, podopretie a výstuž pred výkopom či betonážou.

Zdroj kót: inputs/client-agreed-layout.json + geometry.json. Pracovná šírka 350 mm: pôvodná štúdia foundation-results.json, R1-R7. Žiadne nové určenie výšky, spodnej pätky ani výstuže.

Rámec overenia pred realizáciou: JRC, Implementation of Design during Execution & Service Life (orientačný odborný podklad, nie schválenie tejto stavby).