

ŠTYRI REBRÁ - TECHNICKÝ PÔDORYS

C / B / B | 16. 9. 2026 | všetky kóty v mm | pracovná šírka rebier 350*

NOVÁ REFERENCIA: OBVODOVÉ ČIARY = PRIBLIŽNÉ STREDY BETÓNU; STARÉ KÓTY OD LÍC A-D SÚ PREKONANÉ

A - D TERAZ OZNAČUJÚ ČIARY, NIE HRANY

A ľavá, B uličná, C pravá a D zadná obvodová čiara. Podľa investora je betón približne vystredený na týchto čiarach. Garážový koniec bol predĺžený o 800 mm.

Modrá = nová deklarovaná referencia v rámci modelu C/B/B. Sivá prerušovaná = pôvodná os horného obvodu zo štúdie; s modrou sa nezhoduje.

Červená = nové rebrá, pracovná šírka 350*


*350 mm = šírka betónového rebra, nie šírka výkopu ani spodnej pätky. Prevzatá zo staršej štúdie; pre 4 rebrá staticky nepotvrdená.

Červené polohy rebier zostali z modelu; ich napojenia na novú modrú referenciu sú neuzavreté. Kóty vpravo sú od čiar A-D, nie od okraja vylieťeho betónu.

Mierka 1 : 100 pri tlači A3 / 100 %

Kontrolná úsečka 50 mm na papieri = 5 000 mm v modeli.

PRIAME KÓTY K HRANÁM A MEDZI REBRAMI: LIST ZK-03

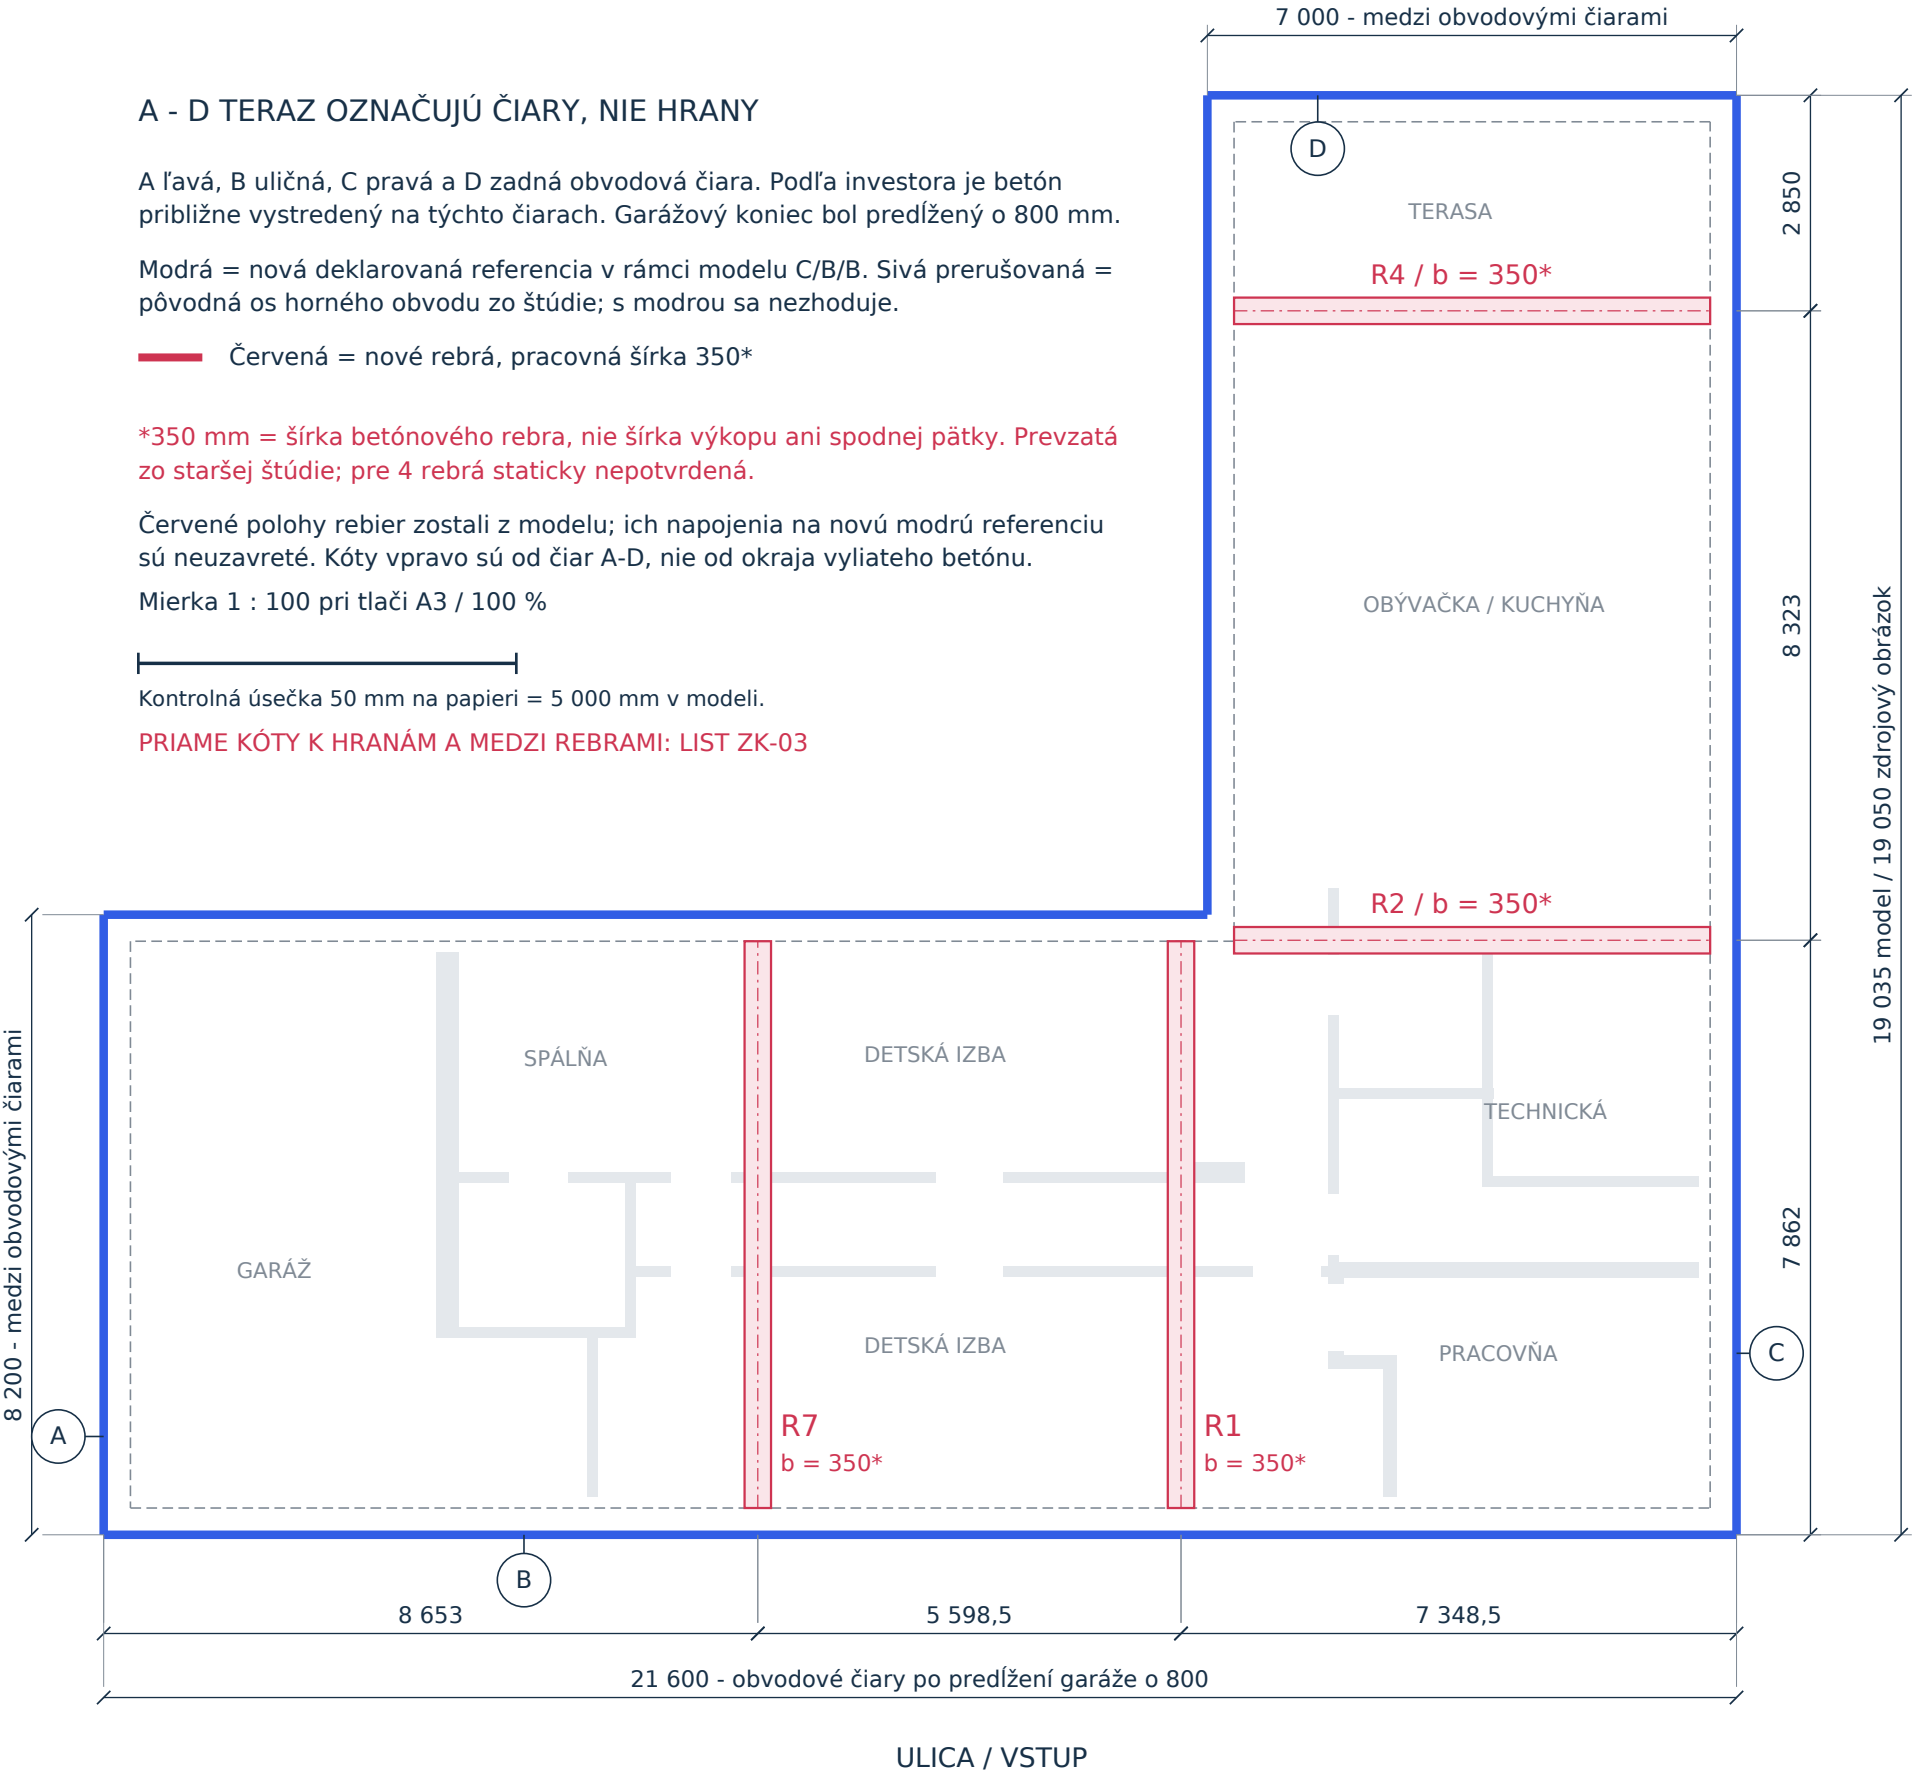

KÓTY OD OBVODOVEJ ČIARY

Všetko v mm. Kolmo dovnútra od čiar A/B/C/D po modelové rebro. Nejde o zamerané kóty od betónových hrán.

Rebro / čiara	Bližšia hrana	Os	Vzdialenejšia hrana
R7 / A	8 478	8 653	8 828
R1 / C	7 173,5	7 348,5	7 523,5
R2 / B	7 687	7 862	8 037
R4 / D	2 675	2 850	3 025

Príklad R7: od čiar A po prvú modelovú hranu 8 478; ďalších 350 tvorí pracovná šírka rebra. Jeho os je od A 8 653.

R1 sa meria sprava od C smerom doľava. R4 sa meria zozadu od D smerom k ulici. R2 od B smerom do záhrady.


Rebro	Šírka*	Stav napojenia
R7	350	Vyžaduje nové zosúladenie s obvodom.
R1	350	Vyžaduje nové zosúladenie s obvodom.
R2	350	Vyžaduje nové zosúladenie s obvodom.
R4	350	Vyžaduje nové zosúladenie s obvodom.

Zobrazené konce červených úsekov sú pôvodné modelové body, nie nové betonážne dĺžky. Medzery pri modrom obvode sú priznaný nesúlád podkladov, nie navrhnuté pracovné škáry.

L-roh: R2 má os Y10 862, modré zalomenie Y11 200: rozdiel338 mm. Ľavý koniec R2 preto nemá preukázané napojenie na nový modrý obvod. Nespojiť ho v kresbe bez návrhu detailu.

Nosná geometria zostáva otvorená: sivé osi horného obvodu sú od modrých čiar odsadené približne349-354 mm. Treba zosúladiť skutočný pás, horný betón a steny; jednoduchá zmena kót sama prenos síl nevyrieši.

PÔDORYSNÝ DETAIL ŠÍRKY / 1 : 10

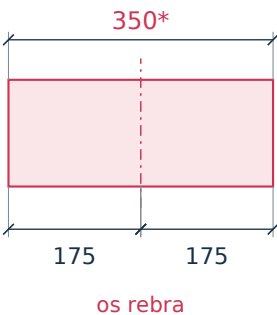

POTVRDENÝ VÝKLAD OBVODU A ROZDIELY

C / B / B | 16. 9. 2026 | všetky kóty v mm | pracovná šírka rebier 350*

NOVÁ REFERENCIA: OBVODOVÉ ČIARY = Približné stredy betónu; Staré kóty od líc A-D sú prekonané

1 / AKTUÁLNE POTVRDENIE INVESTORA

Betón je približne vystredený po čiarach obvodu na novom obrázku. Investor výslovne potvrdil predĺženie garážového konca o 800 mm: 20 800 + 800 = 21 600 mm. Ide o deklarovaný stav; presné líca a polohy zatiaľ nie sú zamerané.

Referencia	Koordináčna čiara v C/B/B	Význam
A - ľavá	X = 6 440	Približná os betónu
B - uličná	Y = 3 000	Približná os betónu
C - pravá	X = 28 040	Približná os betónu
D - zadná	Y = 22 035	Približná os betónu

Súradnice používajú rámec hlavného pôdorysu. Ich priradenie ku skutočným pásom zostáva koordináčné, nie geodeticky potvrdené. A-D už neoznačujú staré vonkajšie líca horného 350mm obvodu.

2 / ČIARA A SKUTOČNÝ OKRAJ BETÓNU

Pri presne vystredenom 400mm páse ležia hrany 200 mm od jeho osi; pri 380mm páse 190 mm. Používateľ však uviedol „približne v strede“, preto presný posun k skutočnému okraju nie je určený. Starú tabuľku od betónových líc nemožno použiť.

Kóty listu 1 sú vzdialenosti modelových osí a líc rebier od referenčných čiar. Nehovoria, kde presne leží zameraná hrana betónu. Šírka 350 mm je stále iba pracovný návrh zo staršej štúdie.

Pôvodné listy sú uložené v archive/before-centerline-clarification-20260916. Táto revízia ich nahrádza; pôvodný výpočet sa nemení na posúdenie novej nosnej geometrie.

3 / ZDROJOVÉ KÓTY A MODEL

Strana L-obvodu	Obrázok + predĺženie	Model C/B/B
Celková šírka	20 800 + 800	21 600
Celková hĺbka	19 050	19 035
Šírka pravého krídla	7 000	7 000
Vnúťorná dĺžka krídla	10 840	10 835
Návrat od garáže po L-roh	13 750 + 800 = 14 550	14 600
Ľavý bok pri garáži	8 200	8 200

Rozmery z obrázka sa pri pravouhlom L neuzatvárajú: 7 000 + 13 750 = 20 750, rozdiel 50 mm oproti 20 800; 8 200 + 10 840 = 19 040, rozdiel 10 mm oproti 19 050. Neopravujú sa potichu. Modelové kóty sú od zdrojových oddelené.

Koordináčné reťazce: 8 653 + 5 598,5 + 7 348,5 = 21 600; 7 862 + 8 323 + 2 850 = 19 035. Potvrdenie 800mm predĺženia rieši šírku, nie presnú polohu všetkých hrán.

4 / ČO TREBA ZOSÚLADIŤ

Pôvodné osi horného obvodu sú voči novým modrým čiaram odsadené dovnútra 349-354 mm. Pôvodný predpoklad súosého spodného a horného pásu preto nemožno prevziať. Treba zamerať priečne polohy betónu a stien a upraviť ich podopretie aj napojenie rebier.

Os R2 leží 338 mm pred zalomením L. Ani priame predĺženie jeho ľavého konca po X21 040 samo nezabezpečí napojenie na zvislý obvod, ktorý začína až na Y11 200. Tento detail zostáva otvorený.

Zdroj: inputs/client-agreed-layout.json, nový obrázok a potvrdenie predĺženia garáže. Model: geometry.json. Pracovná šírka 350 mm: staršia štúdia R1-R7. Výška, pätky a výstuž sa tu nanovo neurčujú.

PRIAME KÓTY K HRANÁM REBIER

C / B / B | 16. 9. 2026 | všetky kóty v mm | pracovná šírka rebier 350*

NOVÁ REFERENCIA: OBVODOVÉ ČIARY = PRIBLIŽNÉ STREDY BETÓNU; STARÉ KÓTY OD LÍC A-D SÚ PREKONANÉ


KÓTY PODĽA TVOJICH ČERVENÝCH ŠÍPOK

Červené kóty vedú po hrany rebier. Medzi rebrami je uvedená čistá medzera. Modrá čiara zostáva referenciou obvodu.

- Kóty k hranám / medzi hranami
- Modrá obvodová referencia

Horná kóta 6 122 ide od ľavej hrany R7 po zvislú modrú čiaru L. Kóta 173,5 udáva vodorovný rozdiel od pravej hrany R1 po tú istú čiaru premietnutú nadol.

Červené rebrá sa neposúvali. Šírka každého je pracovných 350 mm*. Os leží 175 mm od hrany.

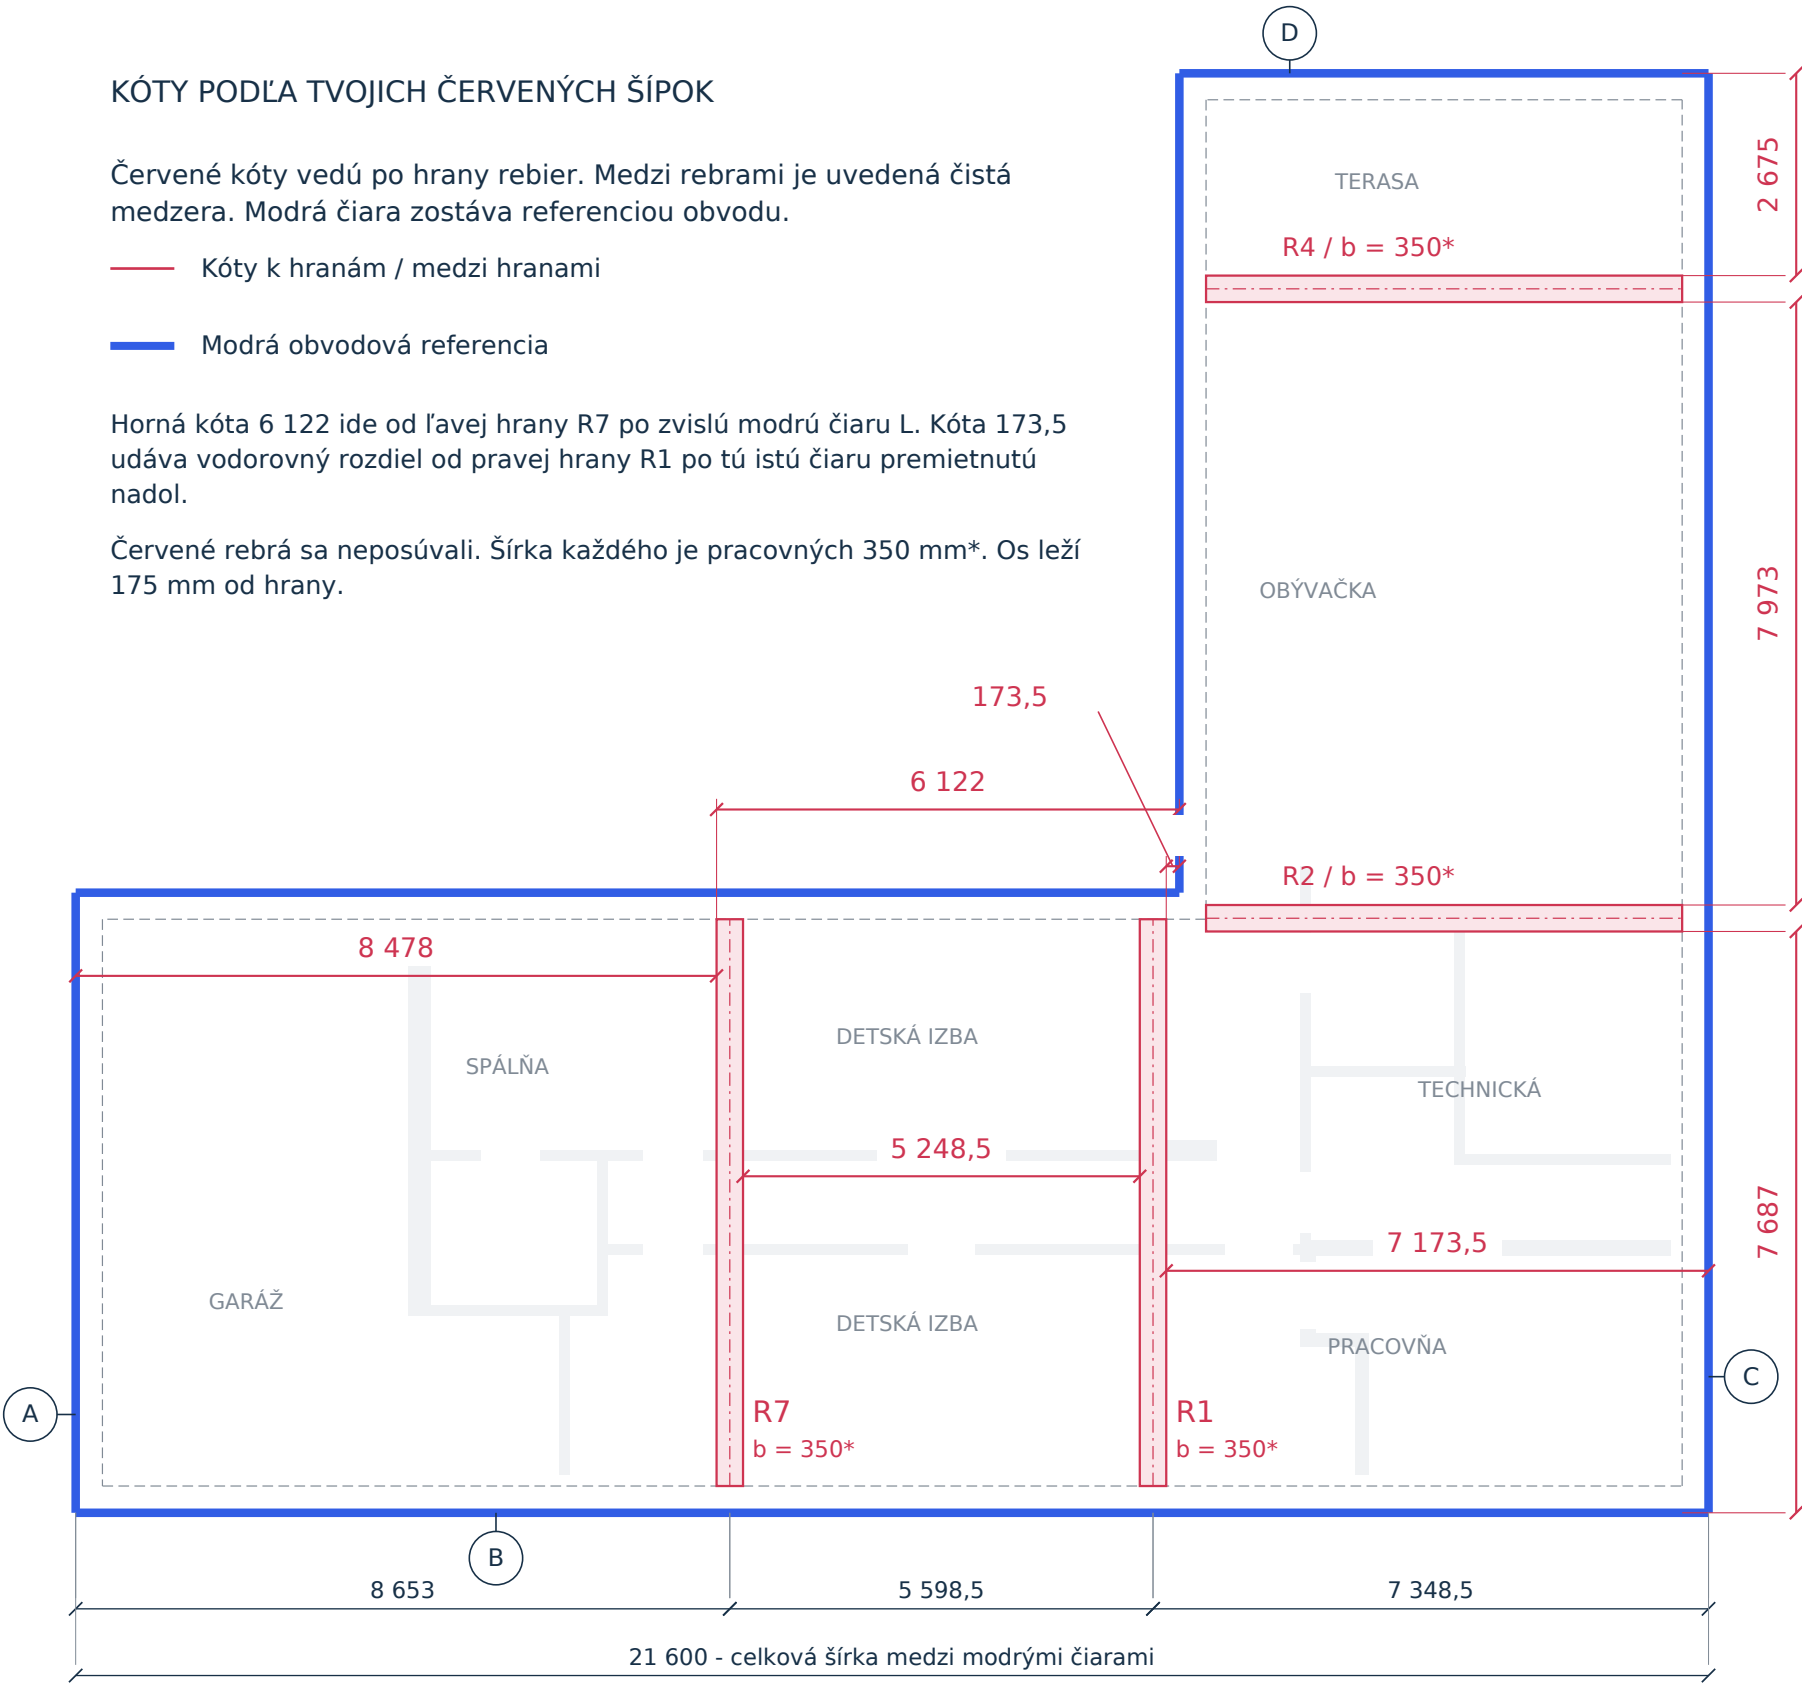

SPODNÝ REŤAZEC JE PO OSIACH REBIER

ODKIAĽ - KAM / VŠETKO V mm

Kóta po hrany	Vzdialenosť
A po ľavú hranu R7	8 478
Svetlá medzera R7 - R1	5 248,5
Ľavá hrana R7 po modrý L-bok	6 122
Pravá hrana R1 po premietnutý L-bok	173,5
Pravá hrana R1 po C	7 173,5
B po dolnú hranu R2	7 687
Svetlá medzera R2 - R4	7 973
Horná hrana R4 po D	2 675

Rozdiel oproti osiam: medzi R7 a R1 je po osiach 5 598,5 mm, ale medzi hranami 5 248,5 mm. Rozdiel 350 mm tvorí polovica šírky každého rebra.

Kontrola šírky:
 $8\,478 + 350 + 5\,248,5 + 350 + 7\,173,5 = 21\,600$.
Kontrola hĺbky:
 $7\,687 + 350 + 7\,973 + 350 + 2\,675 = 19\,035$.

Rozsah kót: ide o presné rozdiely modelových línii a hrán navrhovaných rebier. Modrá čiara nie je zameraná hrana vyliateho betónu.

*Šírka 350 mm nie je staticky potvrdená pre túto štvoricu. Kóty 6 122 a 173,5 sú vodorovné priemety k L-boku; nepreukazujú napojenie ani podopretie. Detaily napojenia zostávajú podľa listov ZK-01 a ZK-02 otvorené.

Zdroj spresnenia: označený výrez investora 16. 9. 2026 o 9:41:18. Mierka 1 : 100 pri tlači A3 na 100 %. Sivá pôvodná os je len pomocná.